


İşçi çizgilərin siyahısı

Vərəq	Adı	Qeyd	Vərəq	Adı	Qeyd
1	İşçi çizgilərin siyahısı. Ümumi məlumat.		65	Drenaj sistemi profili (D67-Q134; Q133-Q137)	
2	Drenaj sistemi planı(əvvəli)		66	Drenaj sistemi profili (D68-Q138; Q138-Q15; D70-Q139)	
3-30	Drenaj sistemi planı(davamı)		67	Drenaj sistemi profili (Q127-Q13; D64-Q131)	
31	Drenaj sistemi planı(sonu)		68	Drenaj sistemi profili (Q72-Q139; D73-Q140; D74-Q142)	
32	Drenaj sistemi profili (D1-Q1; Q1-Q9; Q9-Q14)		69	Drenaj sistemi profili (D75-Q143)	
33	Drenaj sistemi profili (Q14-Q17; Q17-Q21; Q22-Q21)		70	Drenaj sistemi profili (D76-Q145; D77-Q146)	
34	Drenaj sistemi profili (D2-Q3; D3-Q29; D4-Q28)		71	Drenaj sistemi profili (D78-Q149; D79-Q148)	
35	Drenaj sistemi profili (D5-Q29; D6-Q30; D7-Q31; D8-Q32)		72	Drenaj sistemi profili (D80-Q152; D81-Q155)	
36	Drenaj sistemi profili (D9-Q33; D10-Q34; D11-Q36)		73	Drenaj sistemi profili (D82-Q156; Q156-Q17; D83-Q160)	
37	Drenaj sistemi profili (D14-Q39; D15-Q39)		74	Drenaj sistemi profili (D84-Q162)	
38	Drenaj sistemi profili (D16-Q43; D17-Q43)		75	Drenaj sistemi profili (D85-Q159; Q159-Q18)	
39	Drenaj sistemi profili (D18-Q47; D19 Q45; Q45-Q47; Q48-Q51)		76	Drenaj sistemi profili (D86-Q165)	
40	Drenaj sistemi profili (Q49-Q51; D22-Q55)		77	Drenaj sistemi profili (D87-Q168; Q165-Q19)	
41	Drenaj sistemi profili (D23-Q53; Q53-Q55)		78	Drenaj sistemi profili (D88-Q170; D89-Q169; D90-Q169; D91-Q171; D93-Q172; D94-Q172; D95-Q174; D92-Q173 Drenaj sistemi profili (D96-Q177; D97-Q175; D98-Q176; D147-Q176)	
42	Drenaj sistemi profili (Q24-Q59; D25-Q57)		79	Drenaj sistemi profili (D100-Q181)	
43	Drenaj sistemi profili (Q57-Q59; D26-Q64)		80	Drenaj sistemi profili (D101-Q178; Q176-Q21)	
44	Drenaj sistemi profili (D27-Q60; D28-Q61; D29-Q62; D30-Q64; D31-Q69)		81	Drenaj sistemi profili (D102-Q21; D103-Q183)	
45	Drenaj sistemi profili (D32-Q69; D33-Q72; D34-Q70)		82	Drenaj sistemi profili (D104-Q183; D105-Q184; D106-Q24)	
46	Drenaj sistemi profili (D35-Q75; D36-Q75)		83	Drenaj sistemi profili (D107-Q23; D108-Q22)	
47	Drenaj sistemi profili (D37-Q79; D38-Q77)		84		
Razlaşdırılmışdı	Tarix				
	İmza				
Soyad					
Vəzifə					
INV.NƏŞEVƏZİNƏ					
IMZA VƏ TARIX					
INVENTAR №					

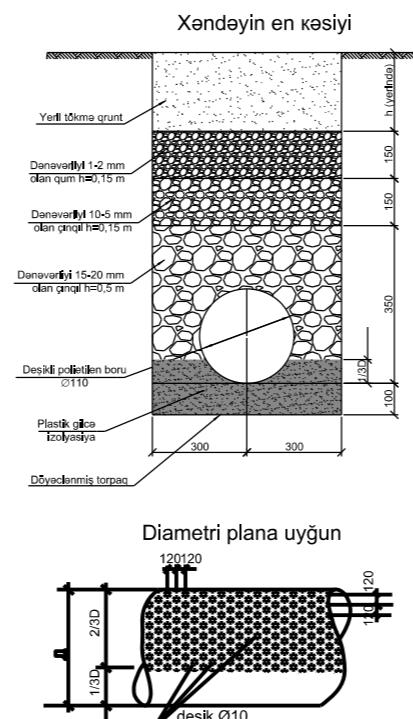


İstinad və əlavə edilən sənədlərin cədvəli

İşarəsi	Adı	Qeyd
	Əlavə edilən sənədlər	
2021/AT-04-DS-9.2.1-S	Avadanlığın material və məmulatların spesifikasiyası	

ÜMUMİ GÖSTƏRİŞLƏR


- DS markalı işçi çizgiləri layihələndirmə tapşırığı və 1:1000 miqyasında tərtib olunmuş planalma əsasında layihələndirilmişdir.
- İşçi çizgiləri qüvvədə olan norma, qayda və standartlara müvafiq işlənib.
- Layihələndirilən su xətləri polietilen nəzərdə tutulmuşdur.
- Torpaq işlərinə başlamazdan əvvəl tikinti meydancası ərazisindən kommunikasiyaları keçən, marağın idarə və təşkilatların nümayəndələrini sahəyə dəvət etməli, qazma işlərini onların iştirakı (nəzarəti) ilə aparmalı.

2021/AT-04-DS-9.2.1					
Suraxanı rayonunun inzibati ərazisində Zığ gölünün ətrafında yerləşən ərazilərdə yeni yaşlılıqların salınması və damcılı suvarma sisteminin qurulması					
Dəyiş.	Dəy.s	Vərəq	Sən.Nö	İmza	Tarix
LBM	T.Ağayev				
İşlədi	N.Məmmədov				
Yoxladı	A. Aliyev				
Normanəz.	Y. Sitnikova				
İşçi çizgilərin siyahısı. Ümumi məlumat.					
Drenaj sistemi					
mərhələ	vərəq	vərəqlər			
İL	1	84			

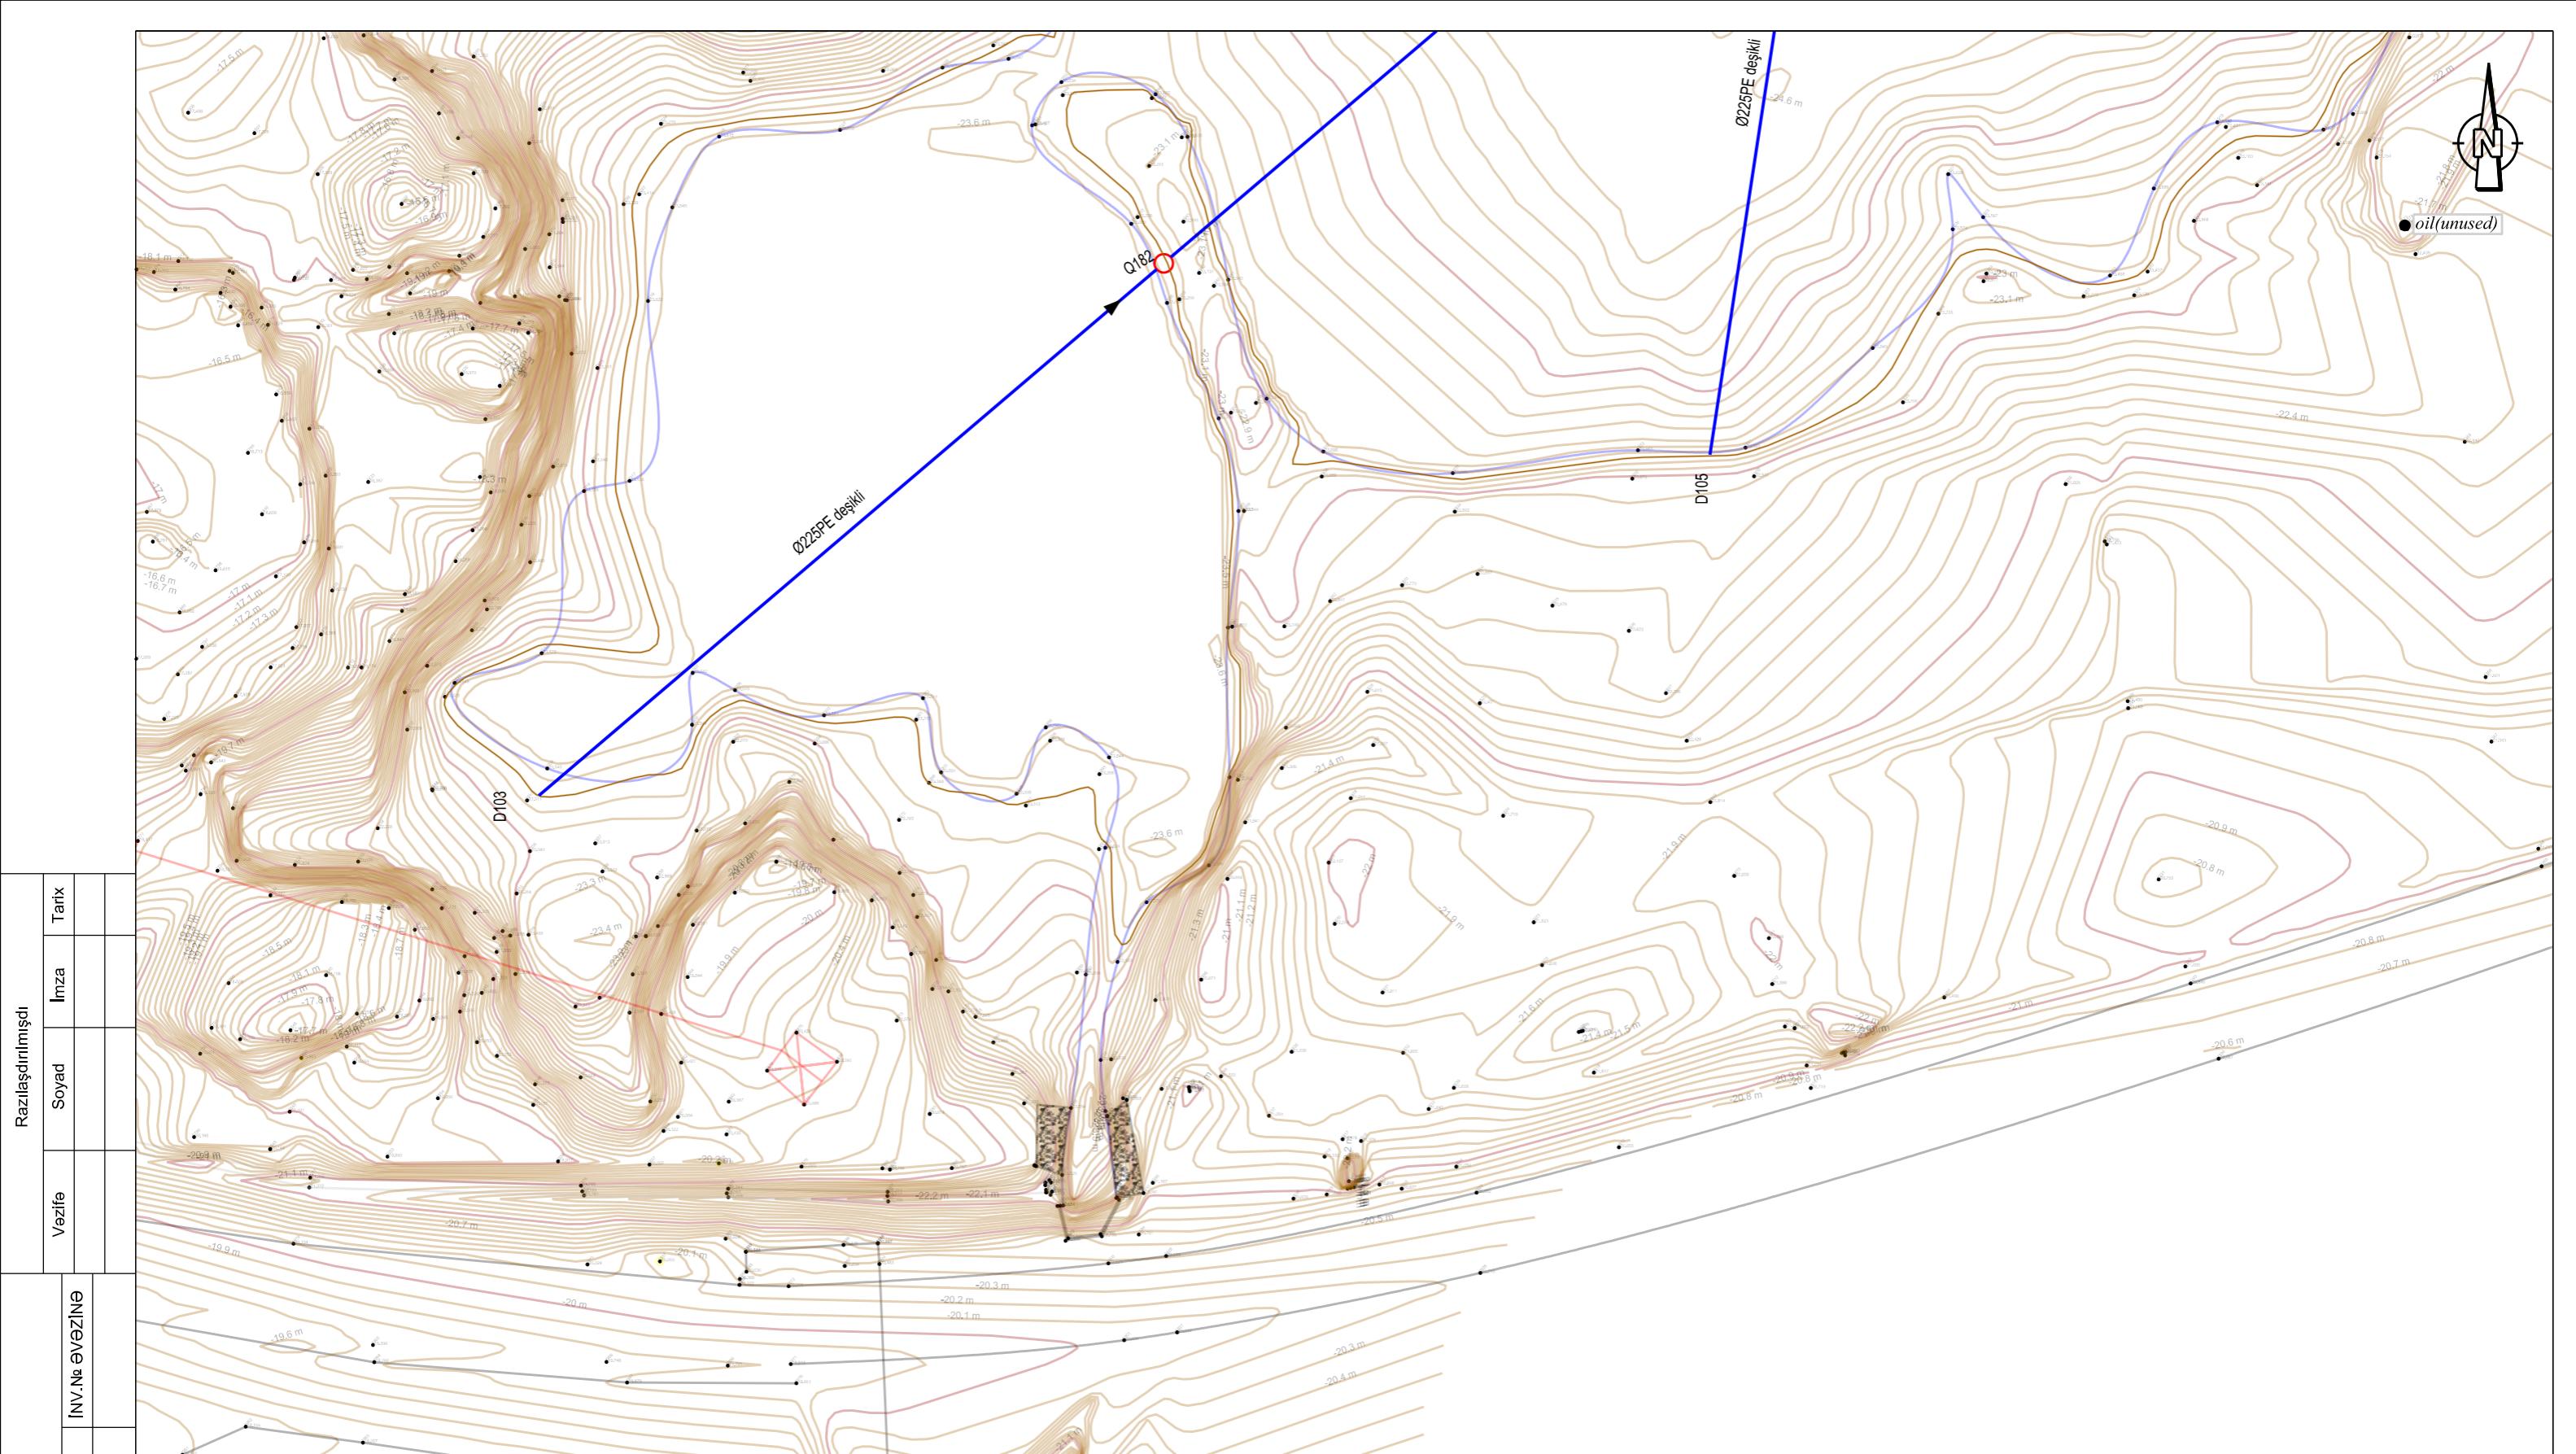


INVENTAR №	IMZA VƏ TARİX	INV.NƏŞEVƏZİNƏ	Razlaşdırılmışlı		
			Vəzifə	Soyad	İmza
			Tarix		

Cizgilərin birləşmə sxemi

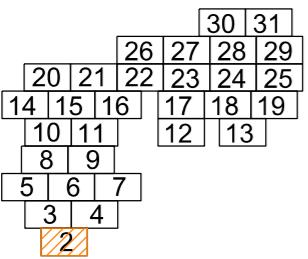

Şerti işaretlər

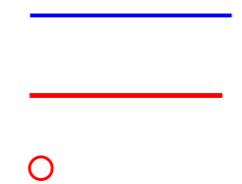

Ø225 HDPE

Ø315 HDPE

Baxış quyusu

2021/AT-04-DS-9.2.1


Suraxanı rayonunun inzibati ərazisində Zığ gölünün ətrafında
yerləşən ərazilərdə yeni yaşlılıqların salınması və damcılı suvarma
sisteminin qurulması

Dəyiş.	Dəy.s	Vərəq	Sən.Nə	İmza	Tarix
LBM	T.Ağayev				
İşlədi	N.Məmmədov				
Yoxladı	A. Aliyev				
Normanəz.	Y. Sitnikova				

Drenaj sistemi


mərhələ	vərəq	vərəqlər
İL	2	84

Drenaj sistemi planı(əvvəli)

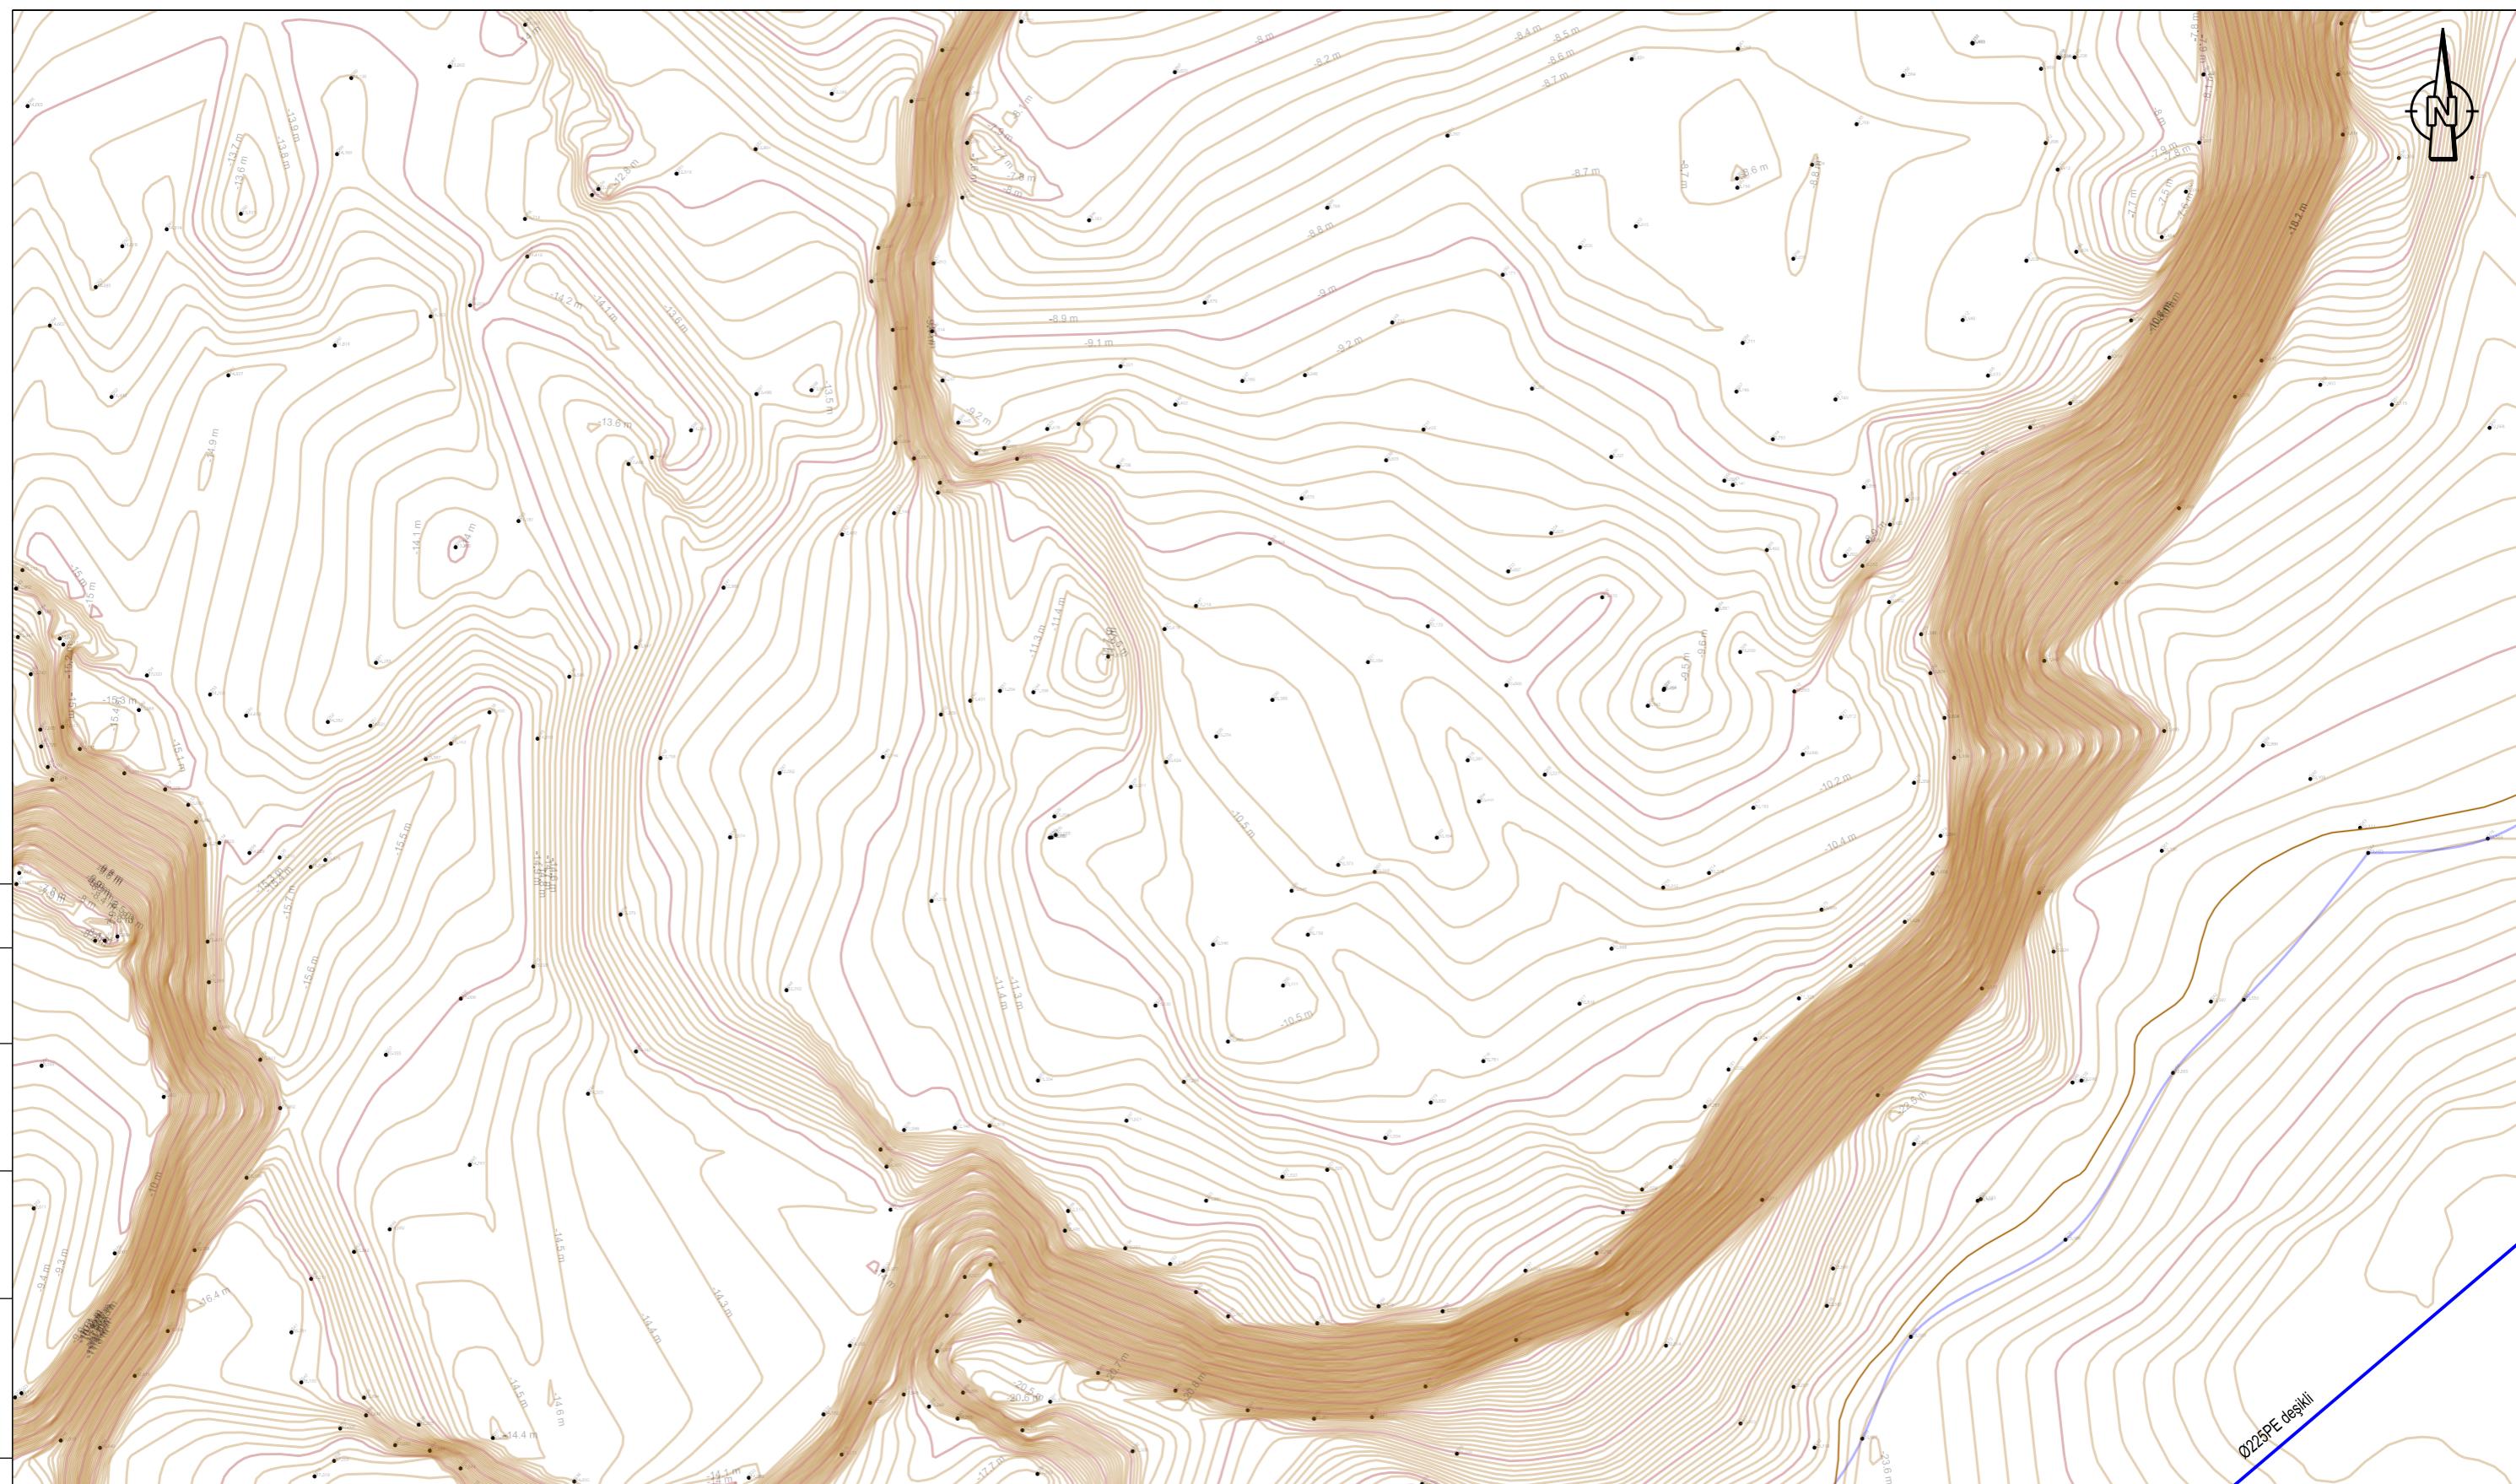

Razılışdırılmış						
INVENTAR №	IMZA VƏ TARİX	INN.№ ƏVƏZNƏ	Vəzifə	Soyad	İmza	Tarix

Cizgilərin birləşmə sxemi

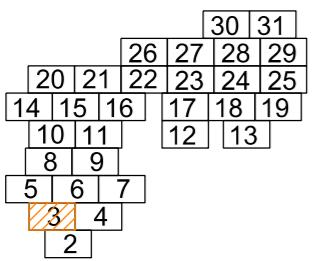

Şərti işarələr

Ø225 HDPE

Ø315 HDPE

Baxış quyusu



2021/AT-04-DS-9.2.1


Tarix Suraxanı rayonunun inzibati ərazisində Zığ gölünün ətrafında yerləşən ərazilərdə yeni yaşlılıqların salınması və damcılı suvarma sisteminin qurulması

Dəyiş.	Dəy.s	Vərəq	Sən.Nö	İmza
LBM	T.Ağayev			
İşlədi	N.Məmmədov			
Yoxladı	A. Aliyev			
Normanəz.	Y. Sitnikova			

Drenaj sistem


Drenaj sistemi planı(davamı)

EIB HYDROTRANS ENGINEERING
ENGINEERING CENTER FOR DESIGN OF WATER AND TRANSPORT INFRASTRUCTURE
SI Vİ NOVİLATİF İNFRASTRUKTURALARIN LİYAHOLINDİRİLMESİ İÇİN MİHONÖKLÜ MİHİC

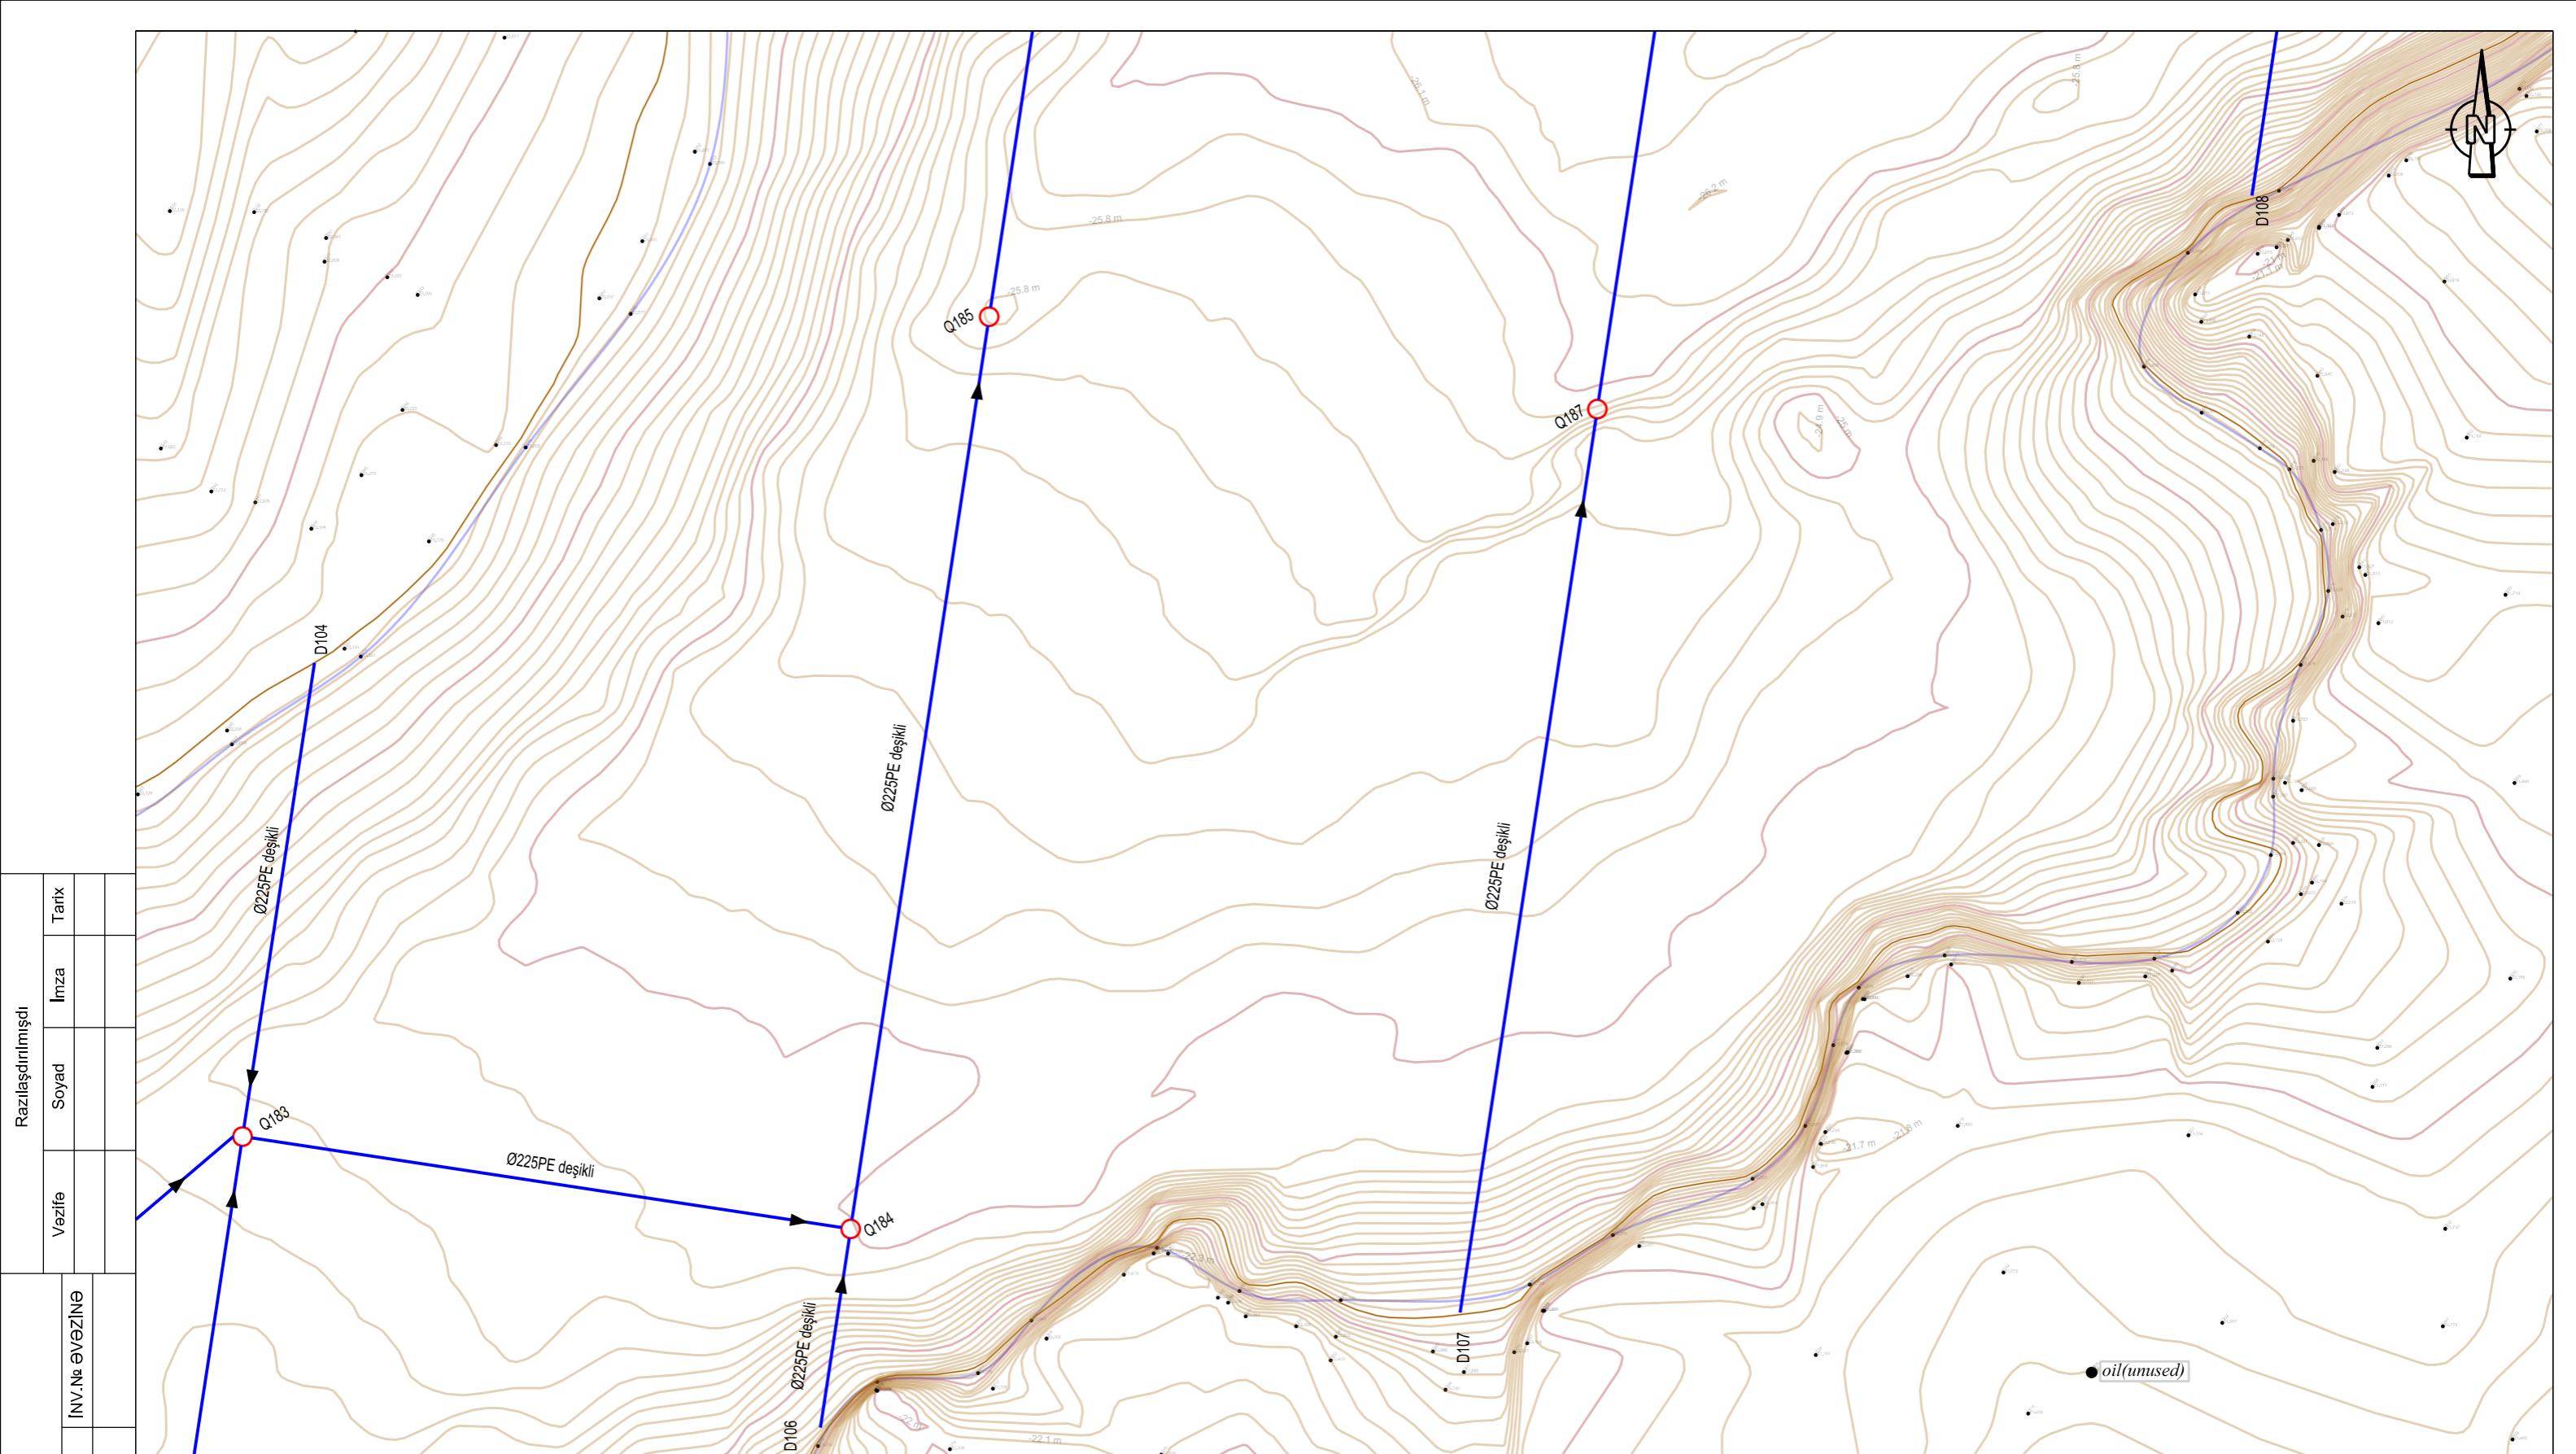


INVENTAR №	IMZA VƏ TARİX	INV.NƏŞƏZİNƏ	Razlaşdırılmışdı		
			Vəzifə	Soyad	İmza

Cizgilərin birləşmə sxemi

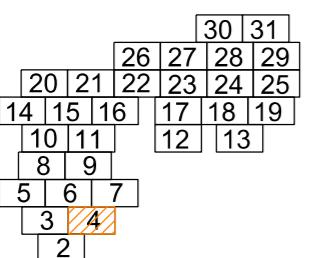

Şerti işarələr

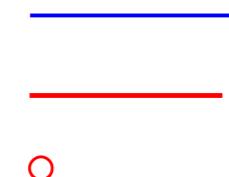

Ø225 HDPE

Ø315 HDPE

Baxış quyusu

2021/AT-04-DS-9.2.1

Suraxanı rayonunun inzibati ərazisində Zığ gölünün ətrafında
yerləşən ərazilərdə yeni yaşillılıqların salınması və damcılı suvarma
sisteminin qurulması

Dəyiş.	Dəy.s	Vərəq	Sən.Nö	İmza	Tarix
LBM		T.Ağayev			
İşlədi		N.Məmmədov			
Yoxladı		A. Aliyev			
Normanəz		Y. Sitnikova			

Drenaj sistemi


mərhələ vərəq vərəqlər

İL 4 84


Drenaj sistemi planı(davamı)

EIB HYDROTRANS ENGINEERING

SÜNÜZ MÜŞAVİRLƏRİN LİFİKLƏNDİRİLMƏSI İZBİ MƏHİNBƏK MƏRCİ

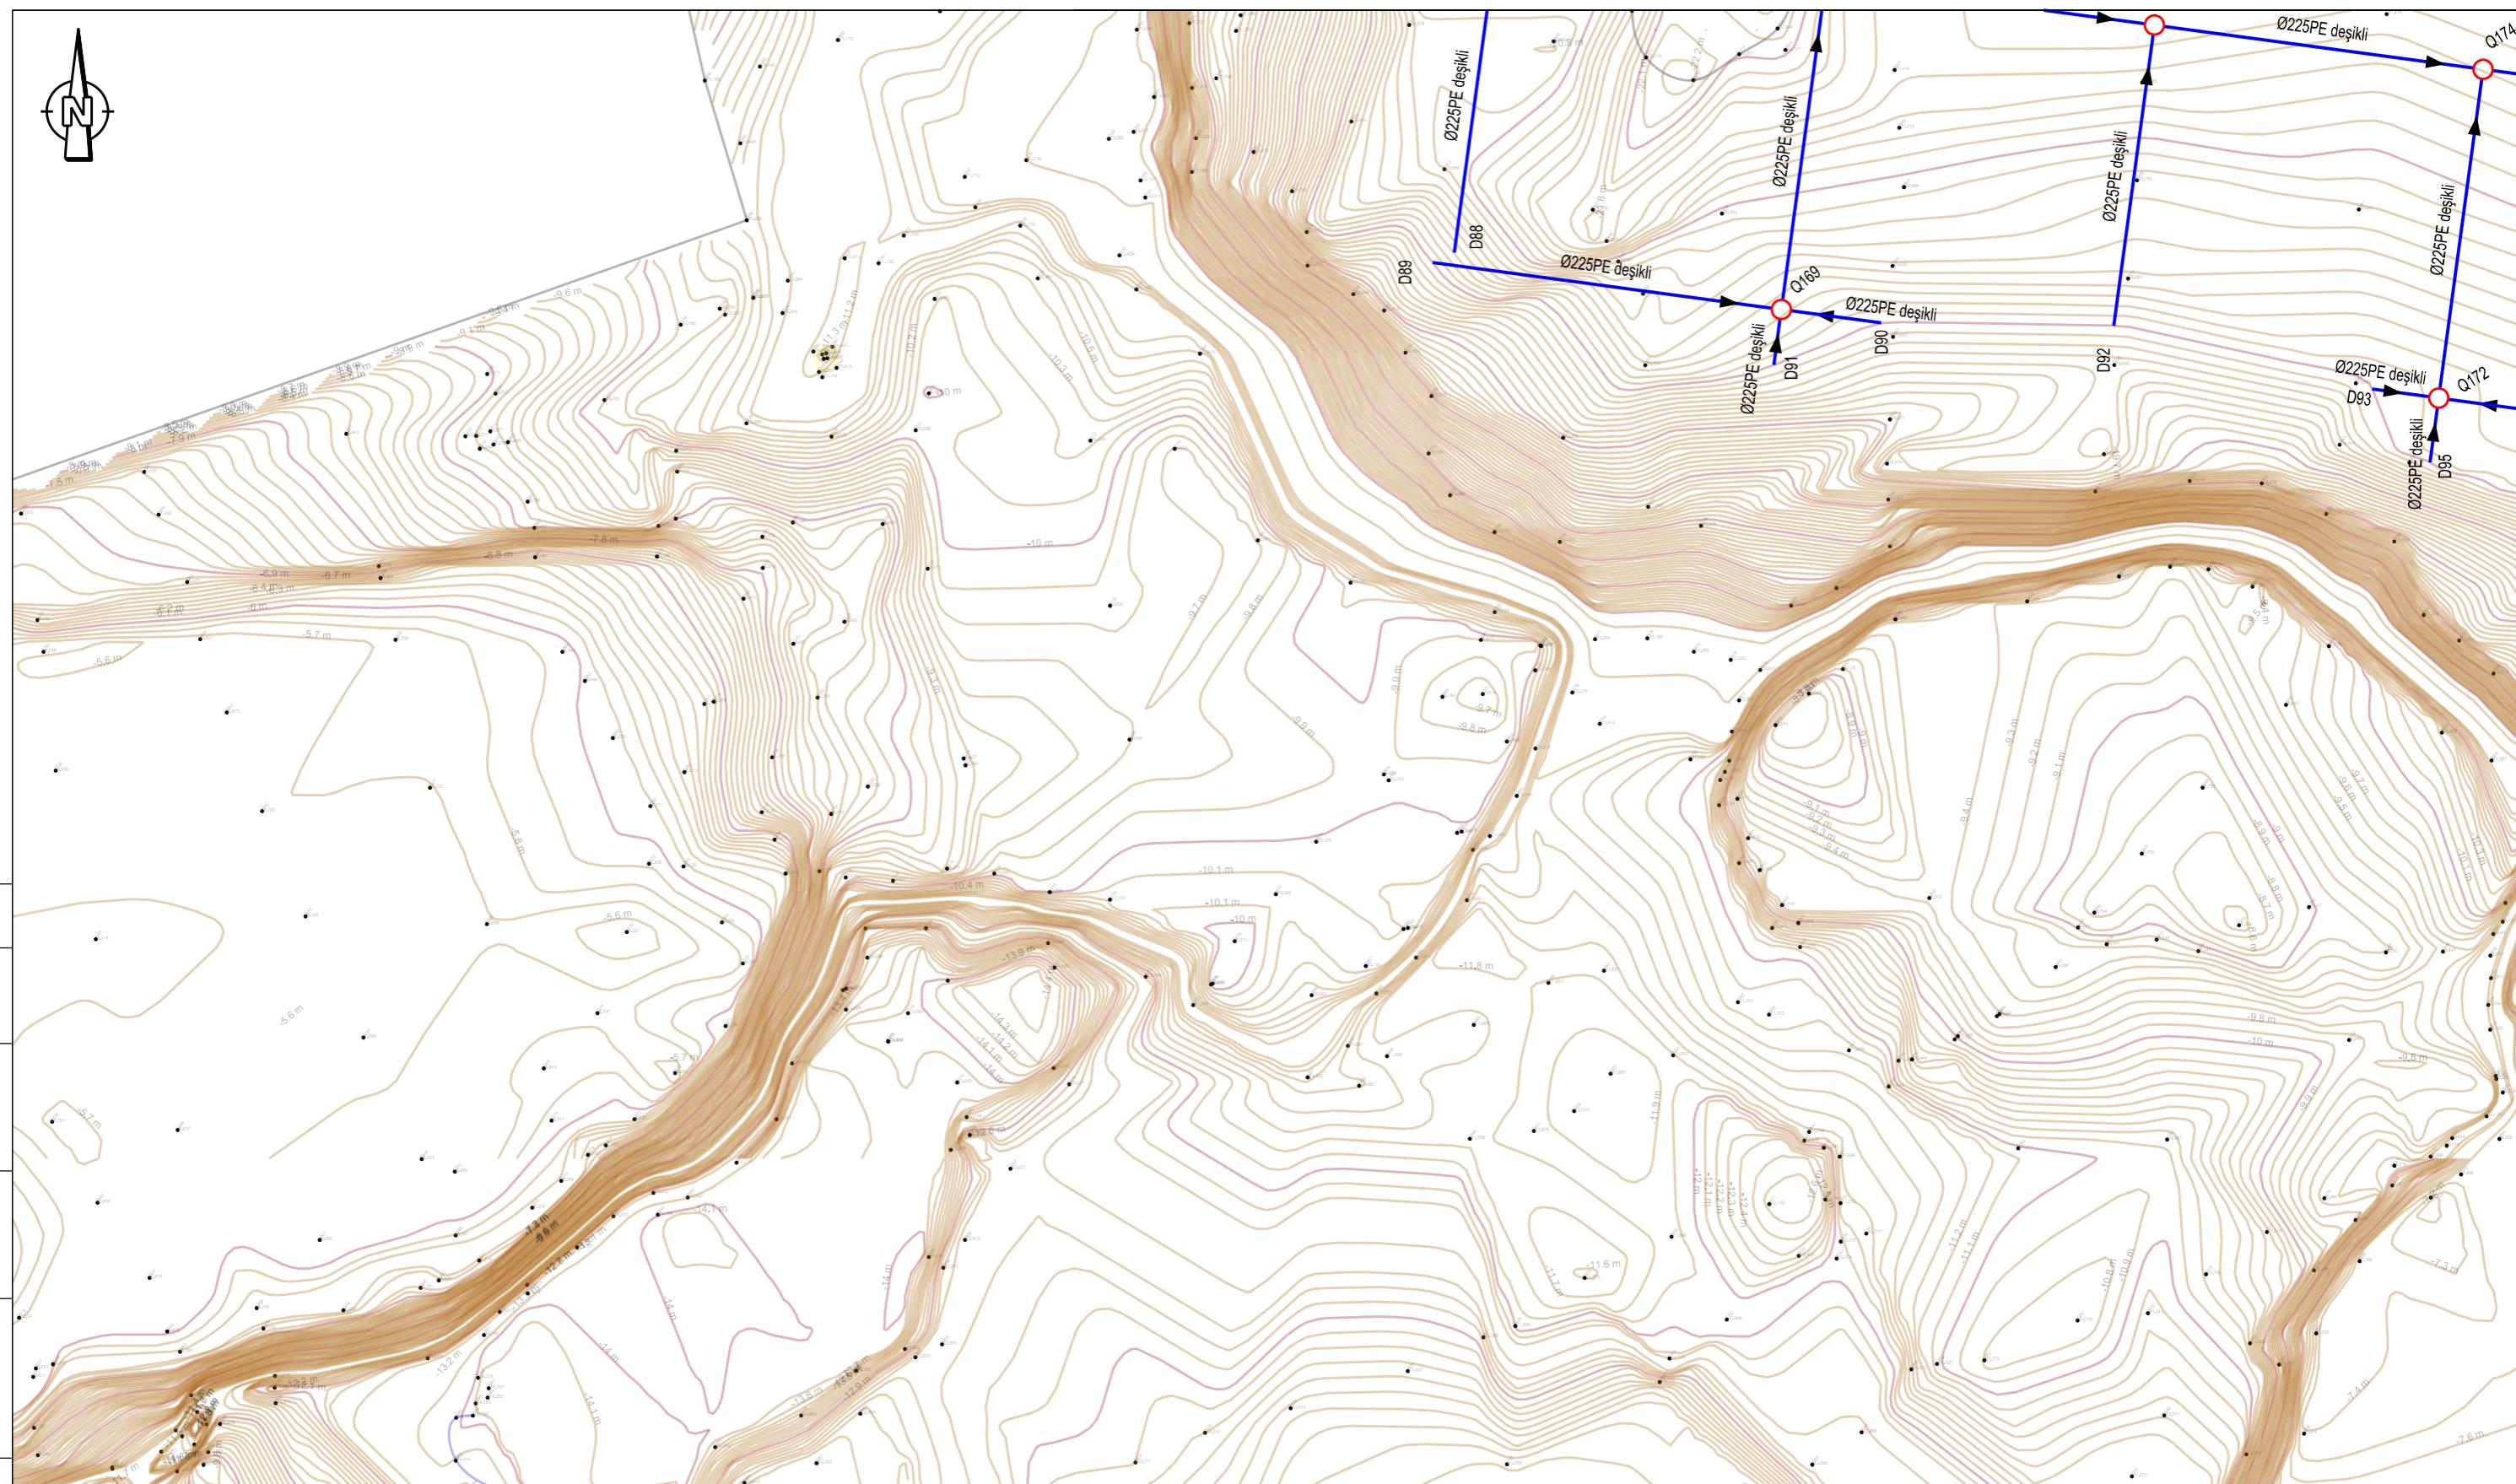

Cizgilərin birləşmə sxemi

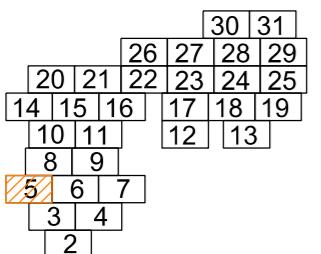

Şərti işarələr

Ø225 HDPE

Ø315 HDPE

Baxış quyusu

www.nature.com/scientificreports/

○

2021/AT-04-DS-9.2.1


Suraxanı rayonunun inzibati ərazisində Zığ gölünün ətrafında
yerləşən ərazilərdə yeni yaşlılıqların salınması və damcılı suvarma
sisteminin qurulması

Dəyiş.	Dəy.s	Vərəq	Sən.Nö	İmza	T
LBM		T.Ağayev			
İşlədi		N.Məmmədov			
Yoxladı		A. Aliev			
Normanəz.		Y. Sıtnikova			


Drenaj sistemi

naj sistemi planı(davamı)

mərhələ	vərəq	vərəqlər
İL	5	84

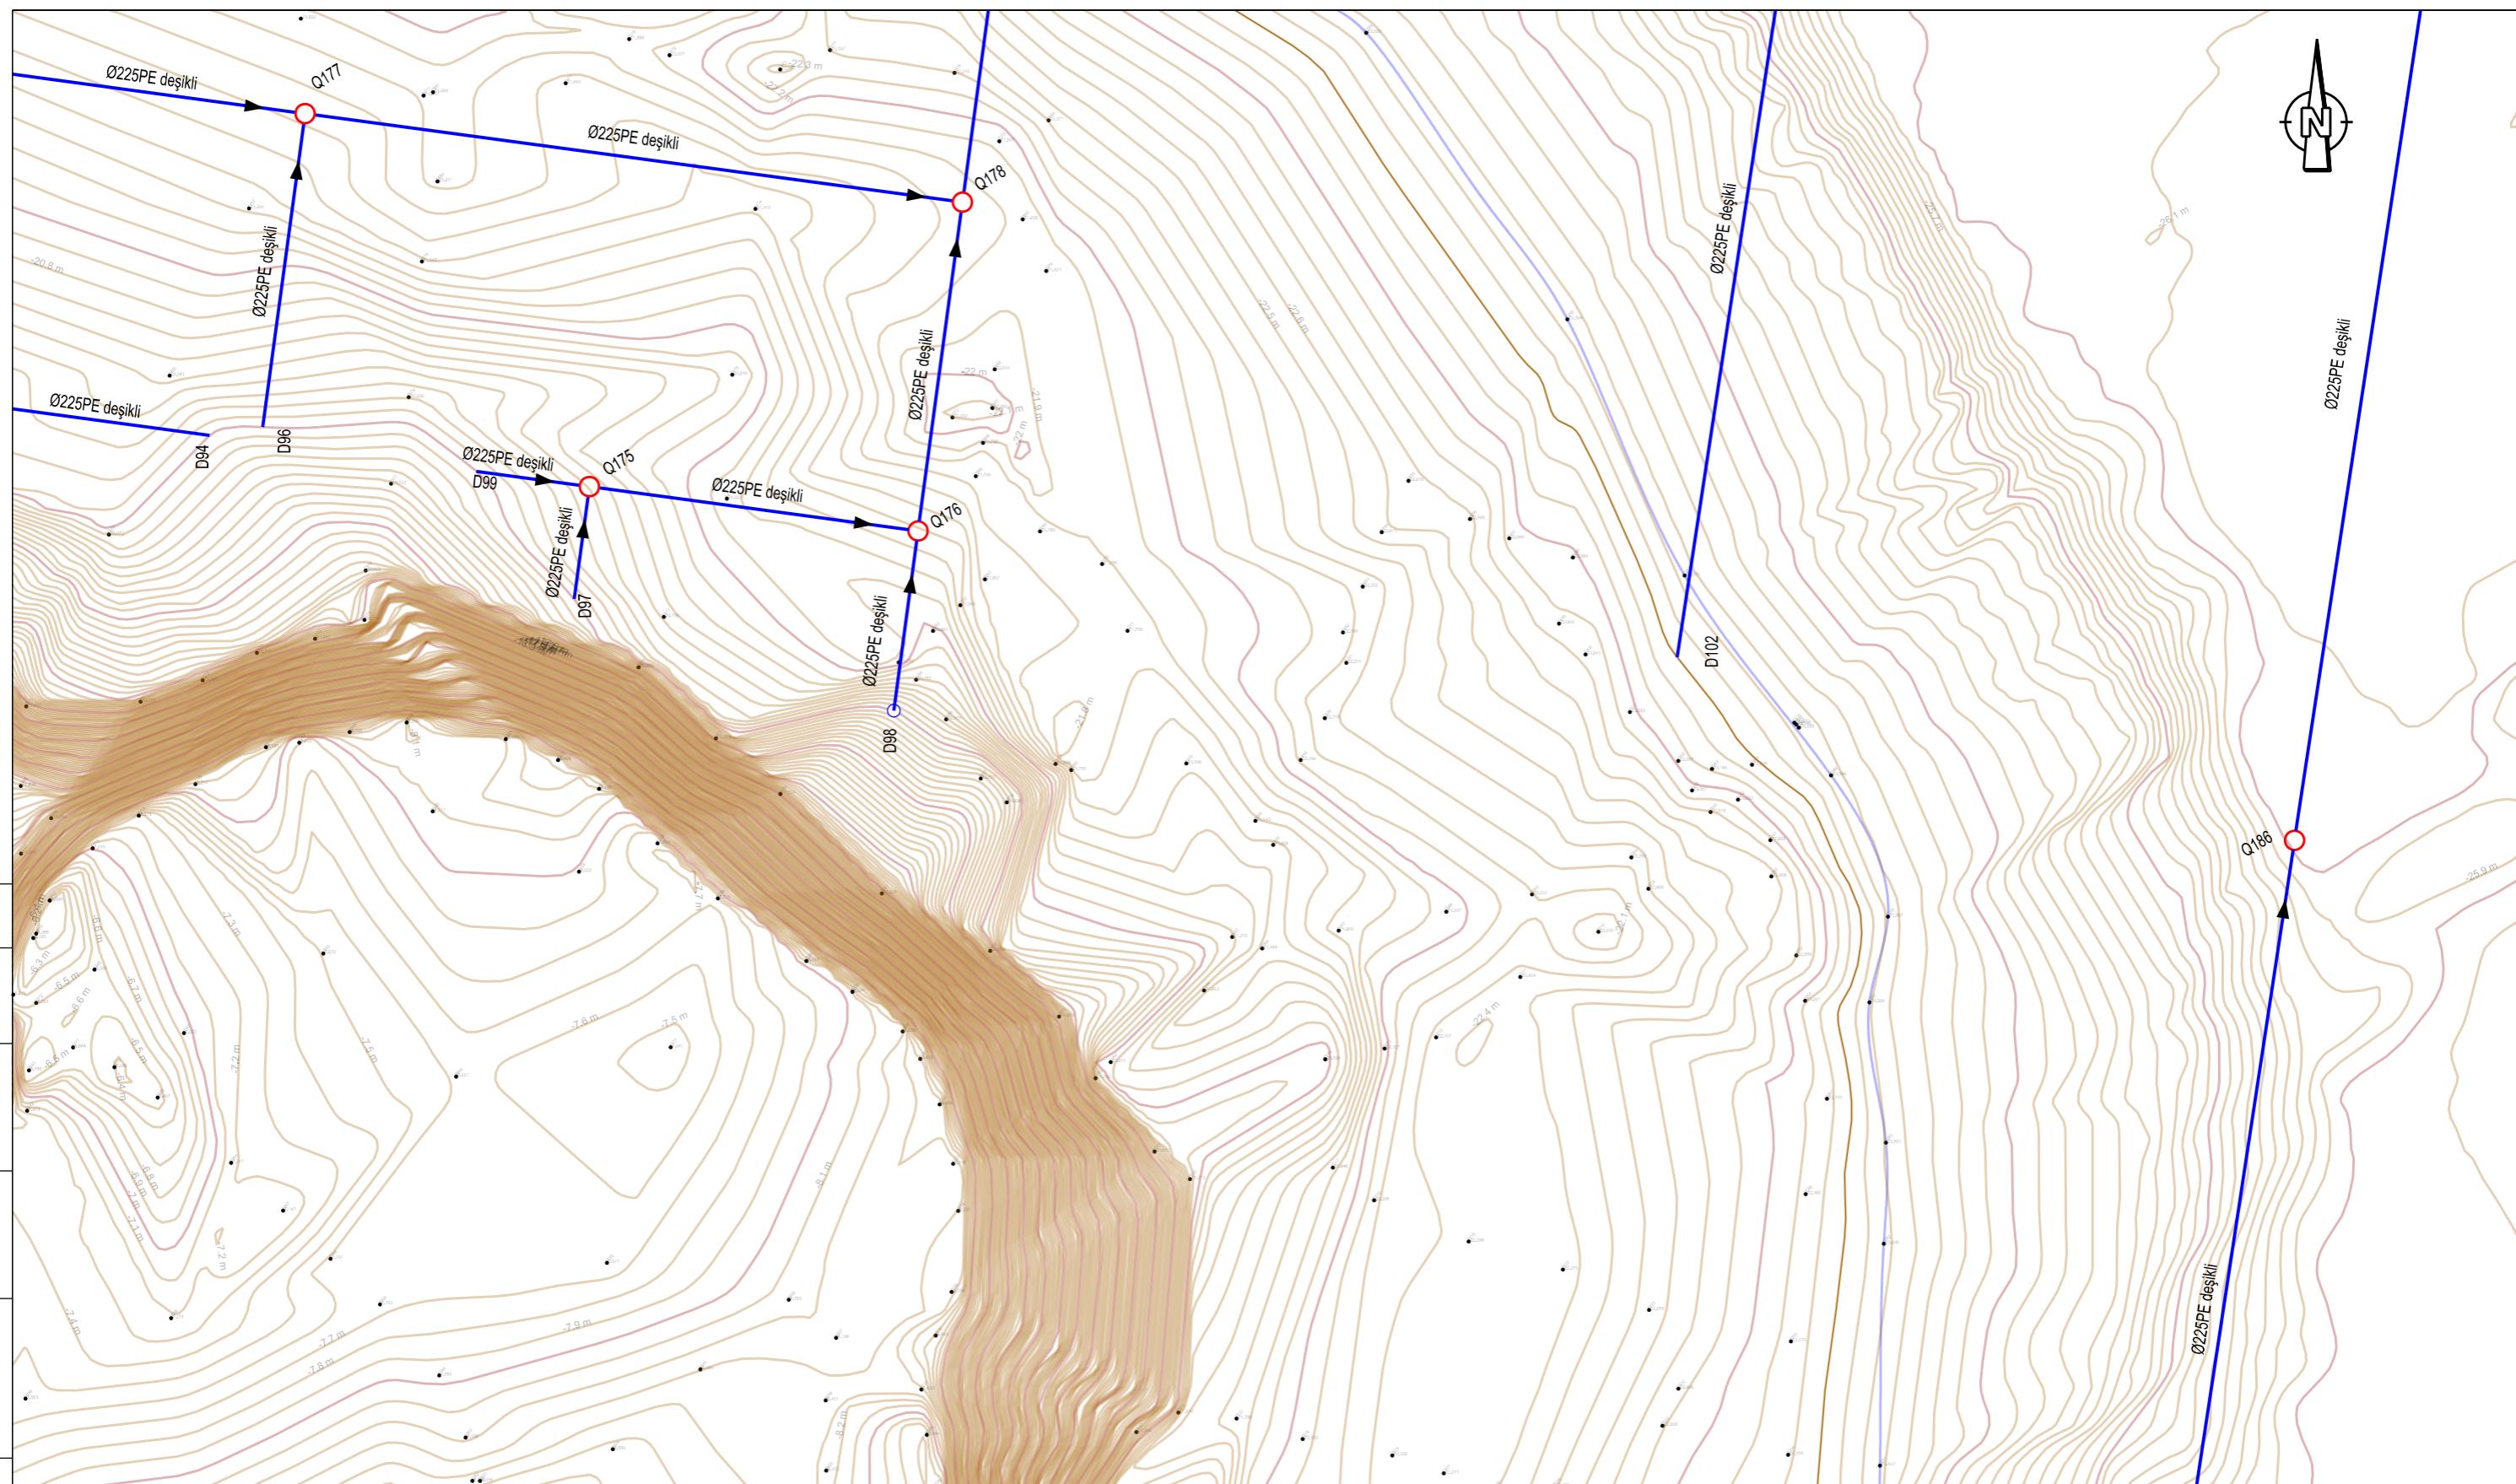

Cizgilərin birləşmə sxemi

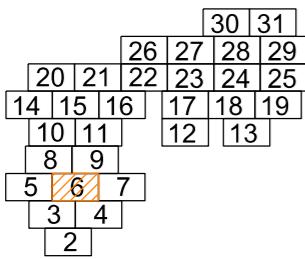


Şərti işarələ

Ø225 HD

Ø315 HD


Baxış quy

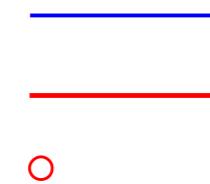

2021/AT-04-DS-9.2.1


Tarix Suraxanı rayonunun inzibati ərazisində Zığ gölünün ətrafında yerləşən ərazilərdə yeni yaşlılıqların salınması və damcılı suvarma sisteminin qurulması

							2021/AT-04-DS-9.2.1		
						Suraxanı rayonunun inzibati ərazisində Zığ gölünün ətrafında yerləşən ərazilərdə yeni yaşlılıqların salınması və damcılı suvarma sisteminin qurulması			
Dəyiş.	Dəy.s	Vərəq	Sən.Nö	İmza	Tarix		mərhələ	vərəq	vərəqlər
LBM	T.Ağayev					Drenaj sistemi	İL	6	84
İşlədi	N.Məmmədov								
Yoxladı	A. Aliyev					Drenaj sistemi planı(davamı)			
Normanəz.	Y. Sitnikova								

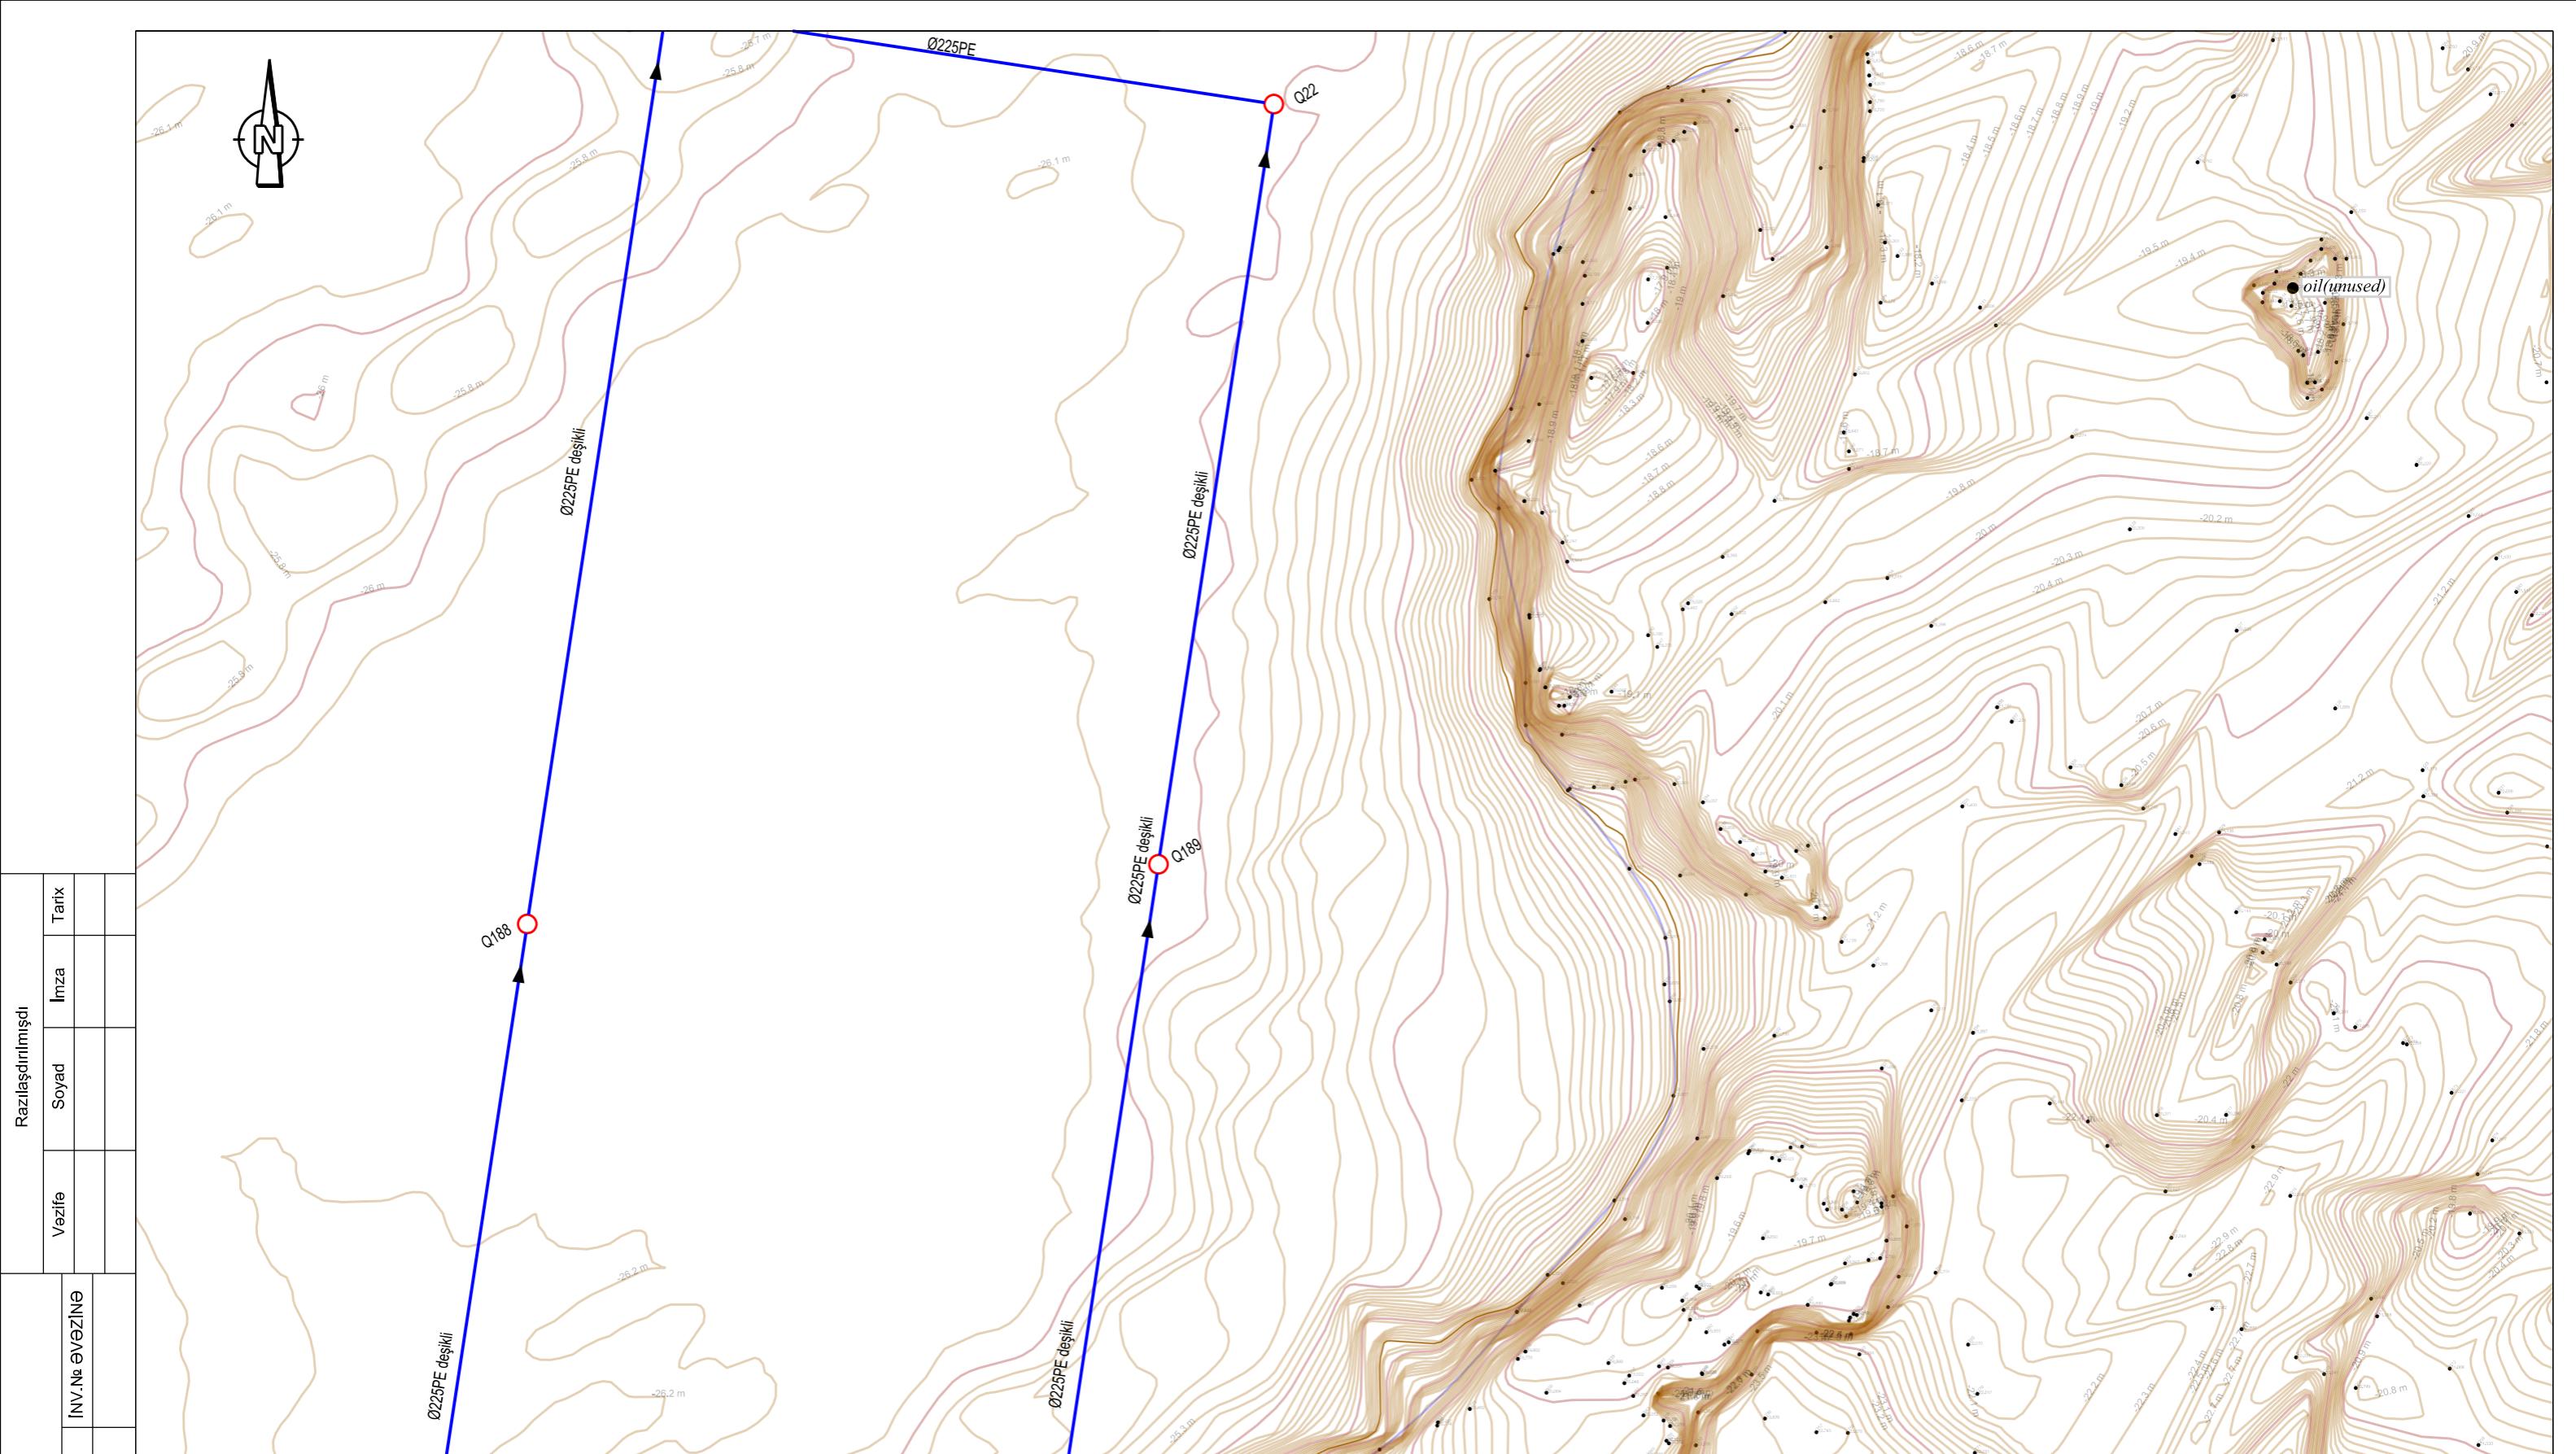

Razılışdırılmışdı			
Vəzifə	Soyad	İmza	Tarix
INVENTAR №	INV.Nº ƏVƏZİNƏ		

Cizgilərin birləşmə sxemi

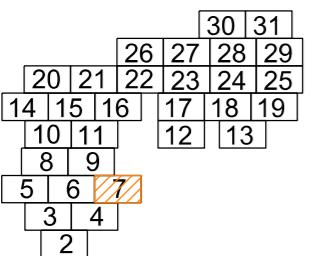


Şerti işaretlər



Ø225 HDPE



Ø315 HDPE

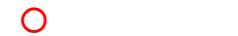


Baxış quyusu

2021/AT-04-DS-9.2.1

Suraxanı rayonunun inzibati ərazisində Zığ gölünün ətrafında
yerləşən ərazilərdə yeni yaşlılıqların salınması və damcılı suvarma
sisteminin qurulması

Dəyiş.	Dəy.s	Vərəq	Sən.Nº	İmza	Tarix
LBM		T.Ağayev			
İşlədi		N.Məmmədov			
Yoxladı		A. Aliyev			
Normanəz.		Y. Sitnikova			


Drenaj sistemi planı(davamı)

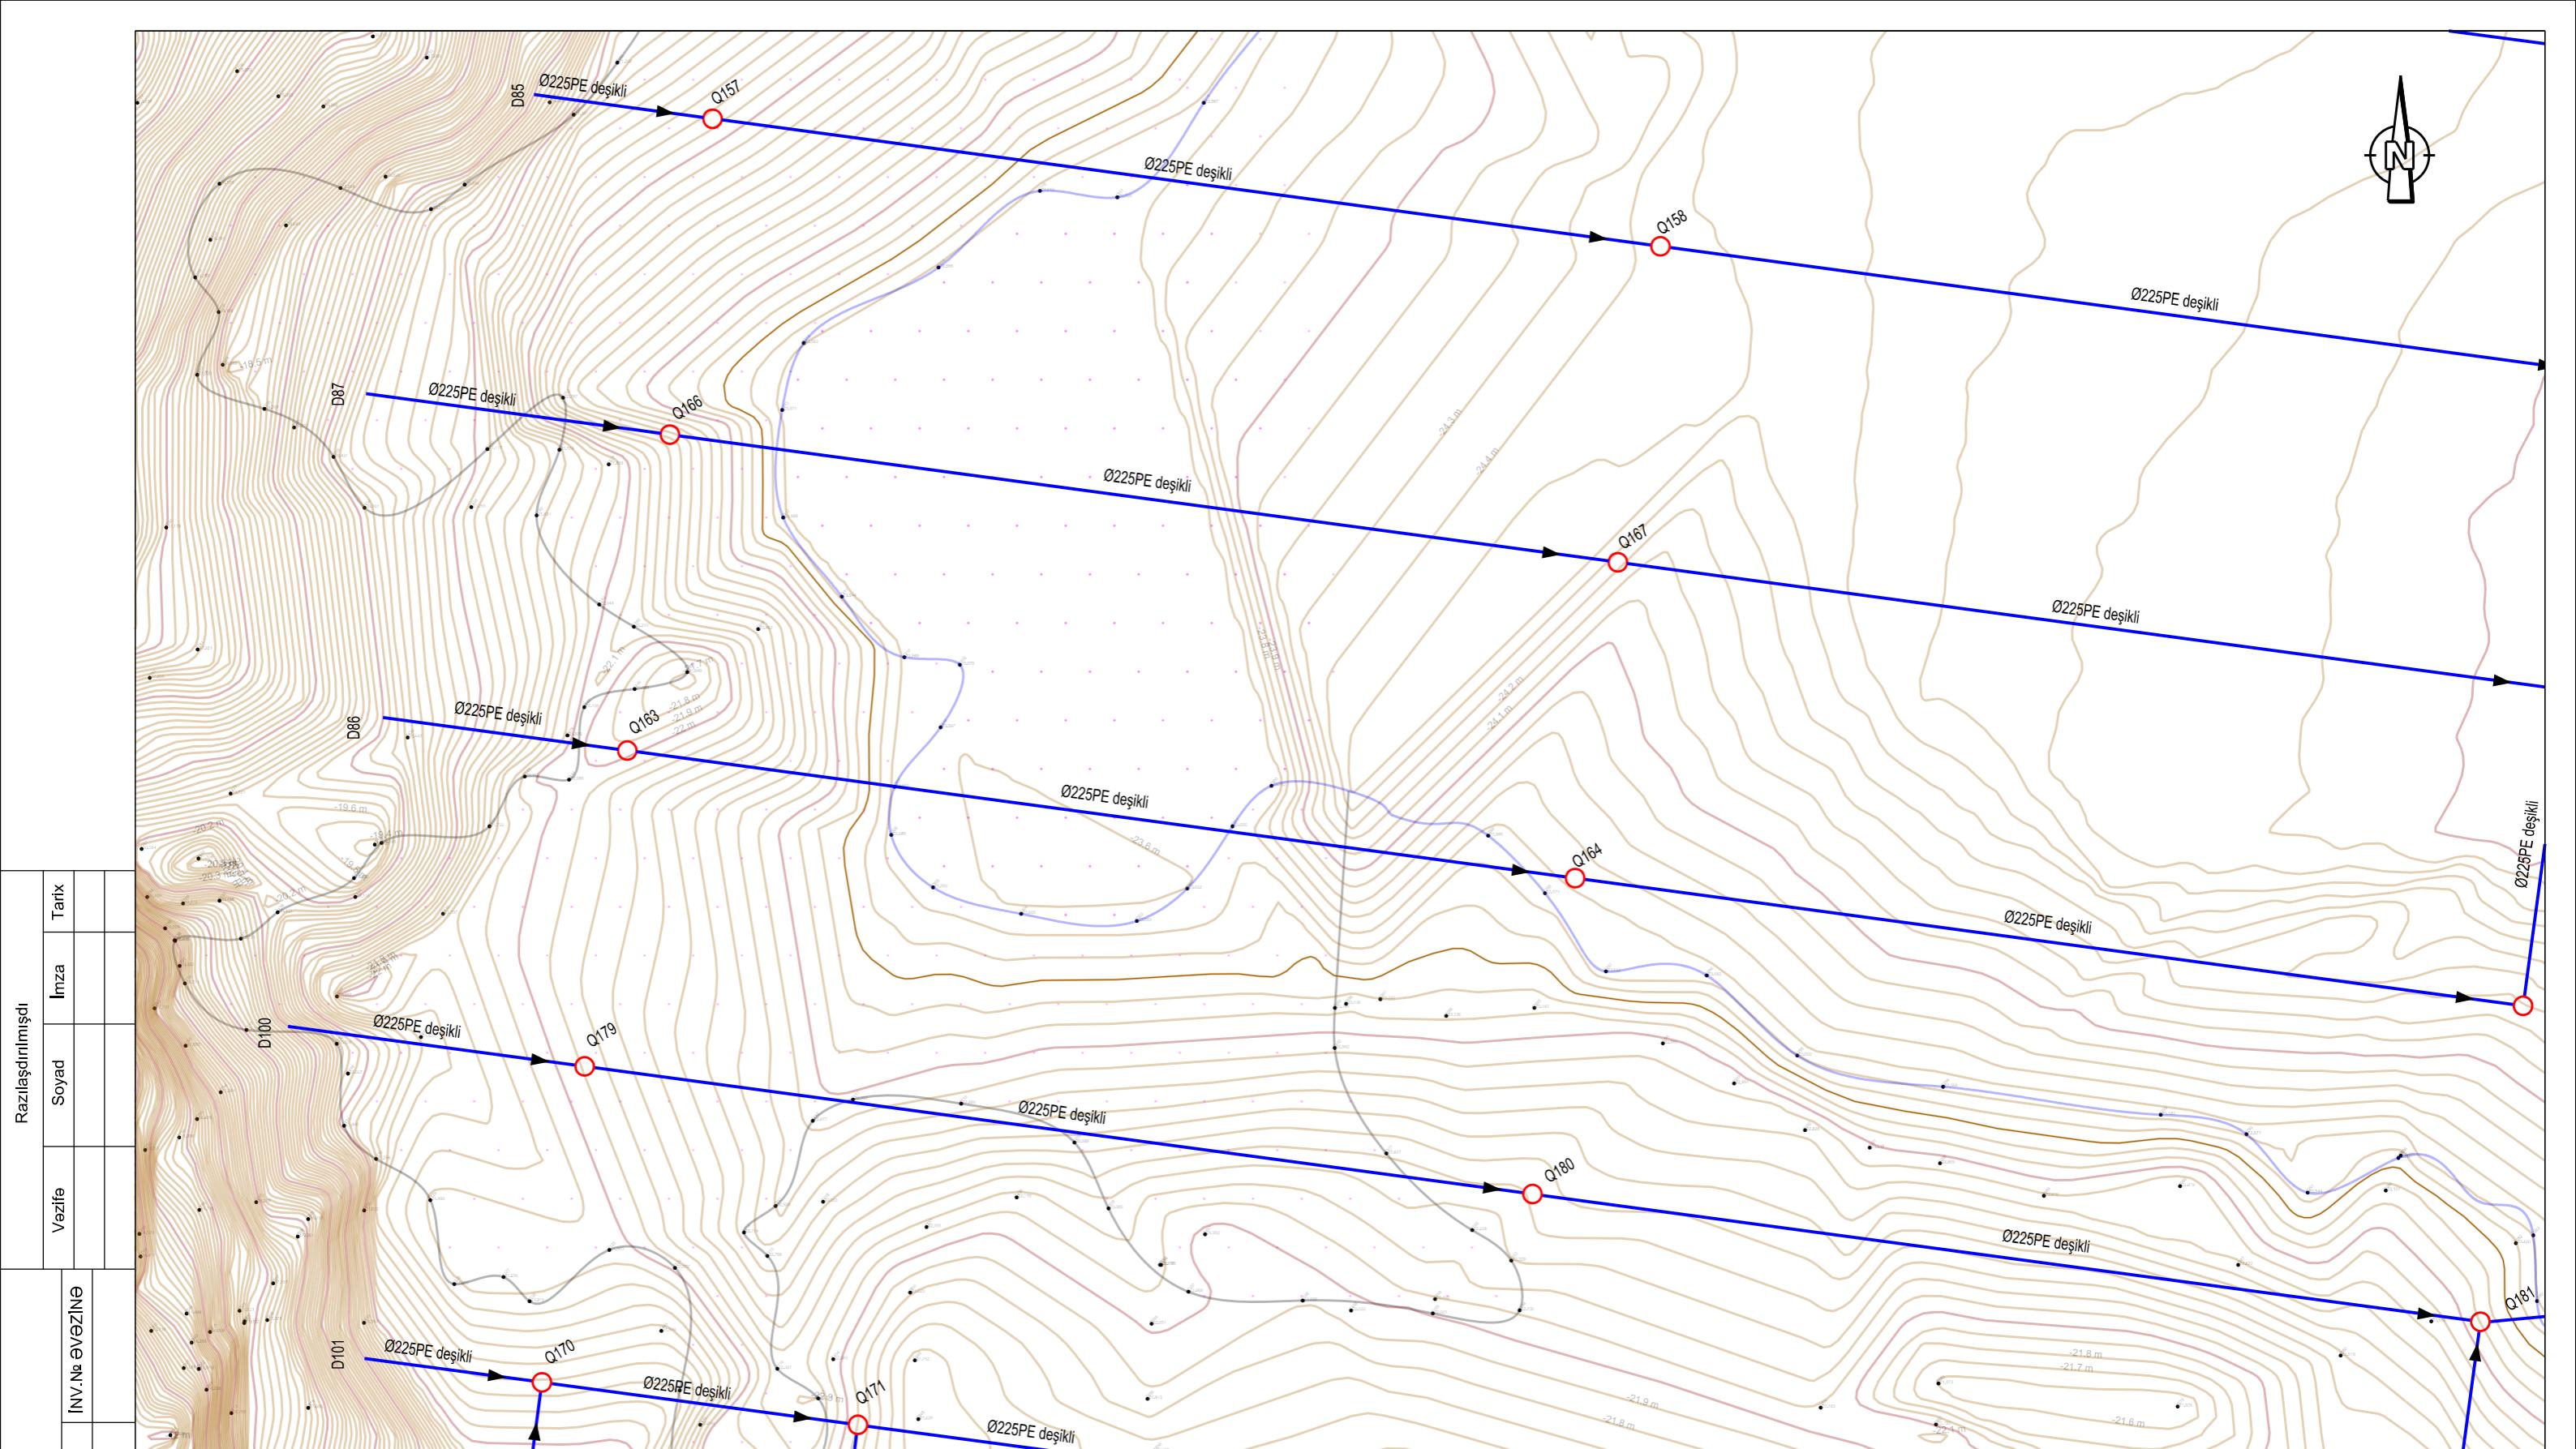


Razlaşdırılmışlı	Vəzifə	Soyad	İmza	Tarix

INVENTAR №	IMZA VƏ TARIX	INV.NƏŞVƏZİNƏ

Cizgilərin birləşmə sxemi

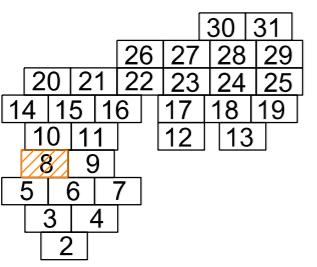

Şerti işarələr

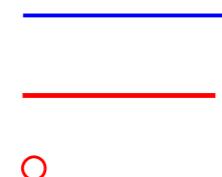

Ø225 HDPE

Ø315 HDPE

Baxış quyusu


2021/AT-04-DS-9.2.1

Suraxanı rayonunun inzibati ərazisində Zığ gölünün ətrafında
yerləşən ərazilərdə yeni yaşlılıqların salınması və damcılı suvarma
sisteminin qurulması


Dəyiş.	Dəy.s	Vərəq	Sən.Nə	İmza	Tarix
LBM	T.Ağayev				
İşlədi	N.Məmmədov				
Yoxladı	A. Aliyev				
Normanəz.	Y. Sitnikova				

Drenaj sistemi planı(davamı)

EIB HYDROTRANS ENGINEERING
ENGINEERING CENTER FOR DESIGN OF WATER AND TRANSPORT INFRASTRUCTURE
SU VƏ NƏqliyyat İnfrastrukturlarının Layihələndirilməsi Üzrə Mərkəzlək Növbəti

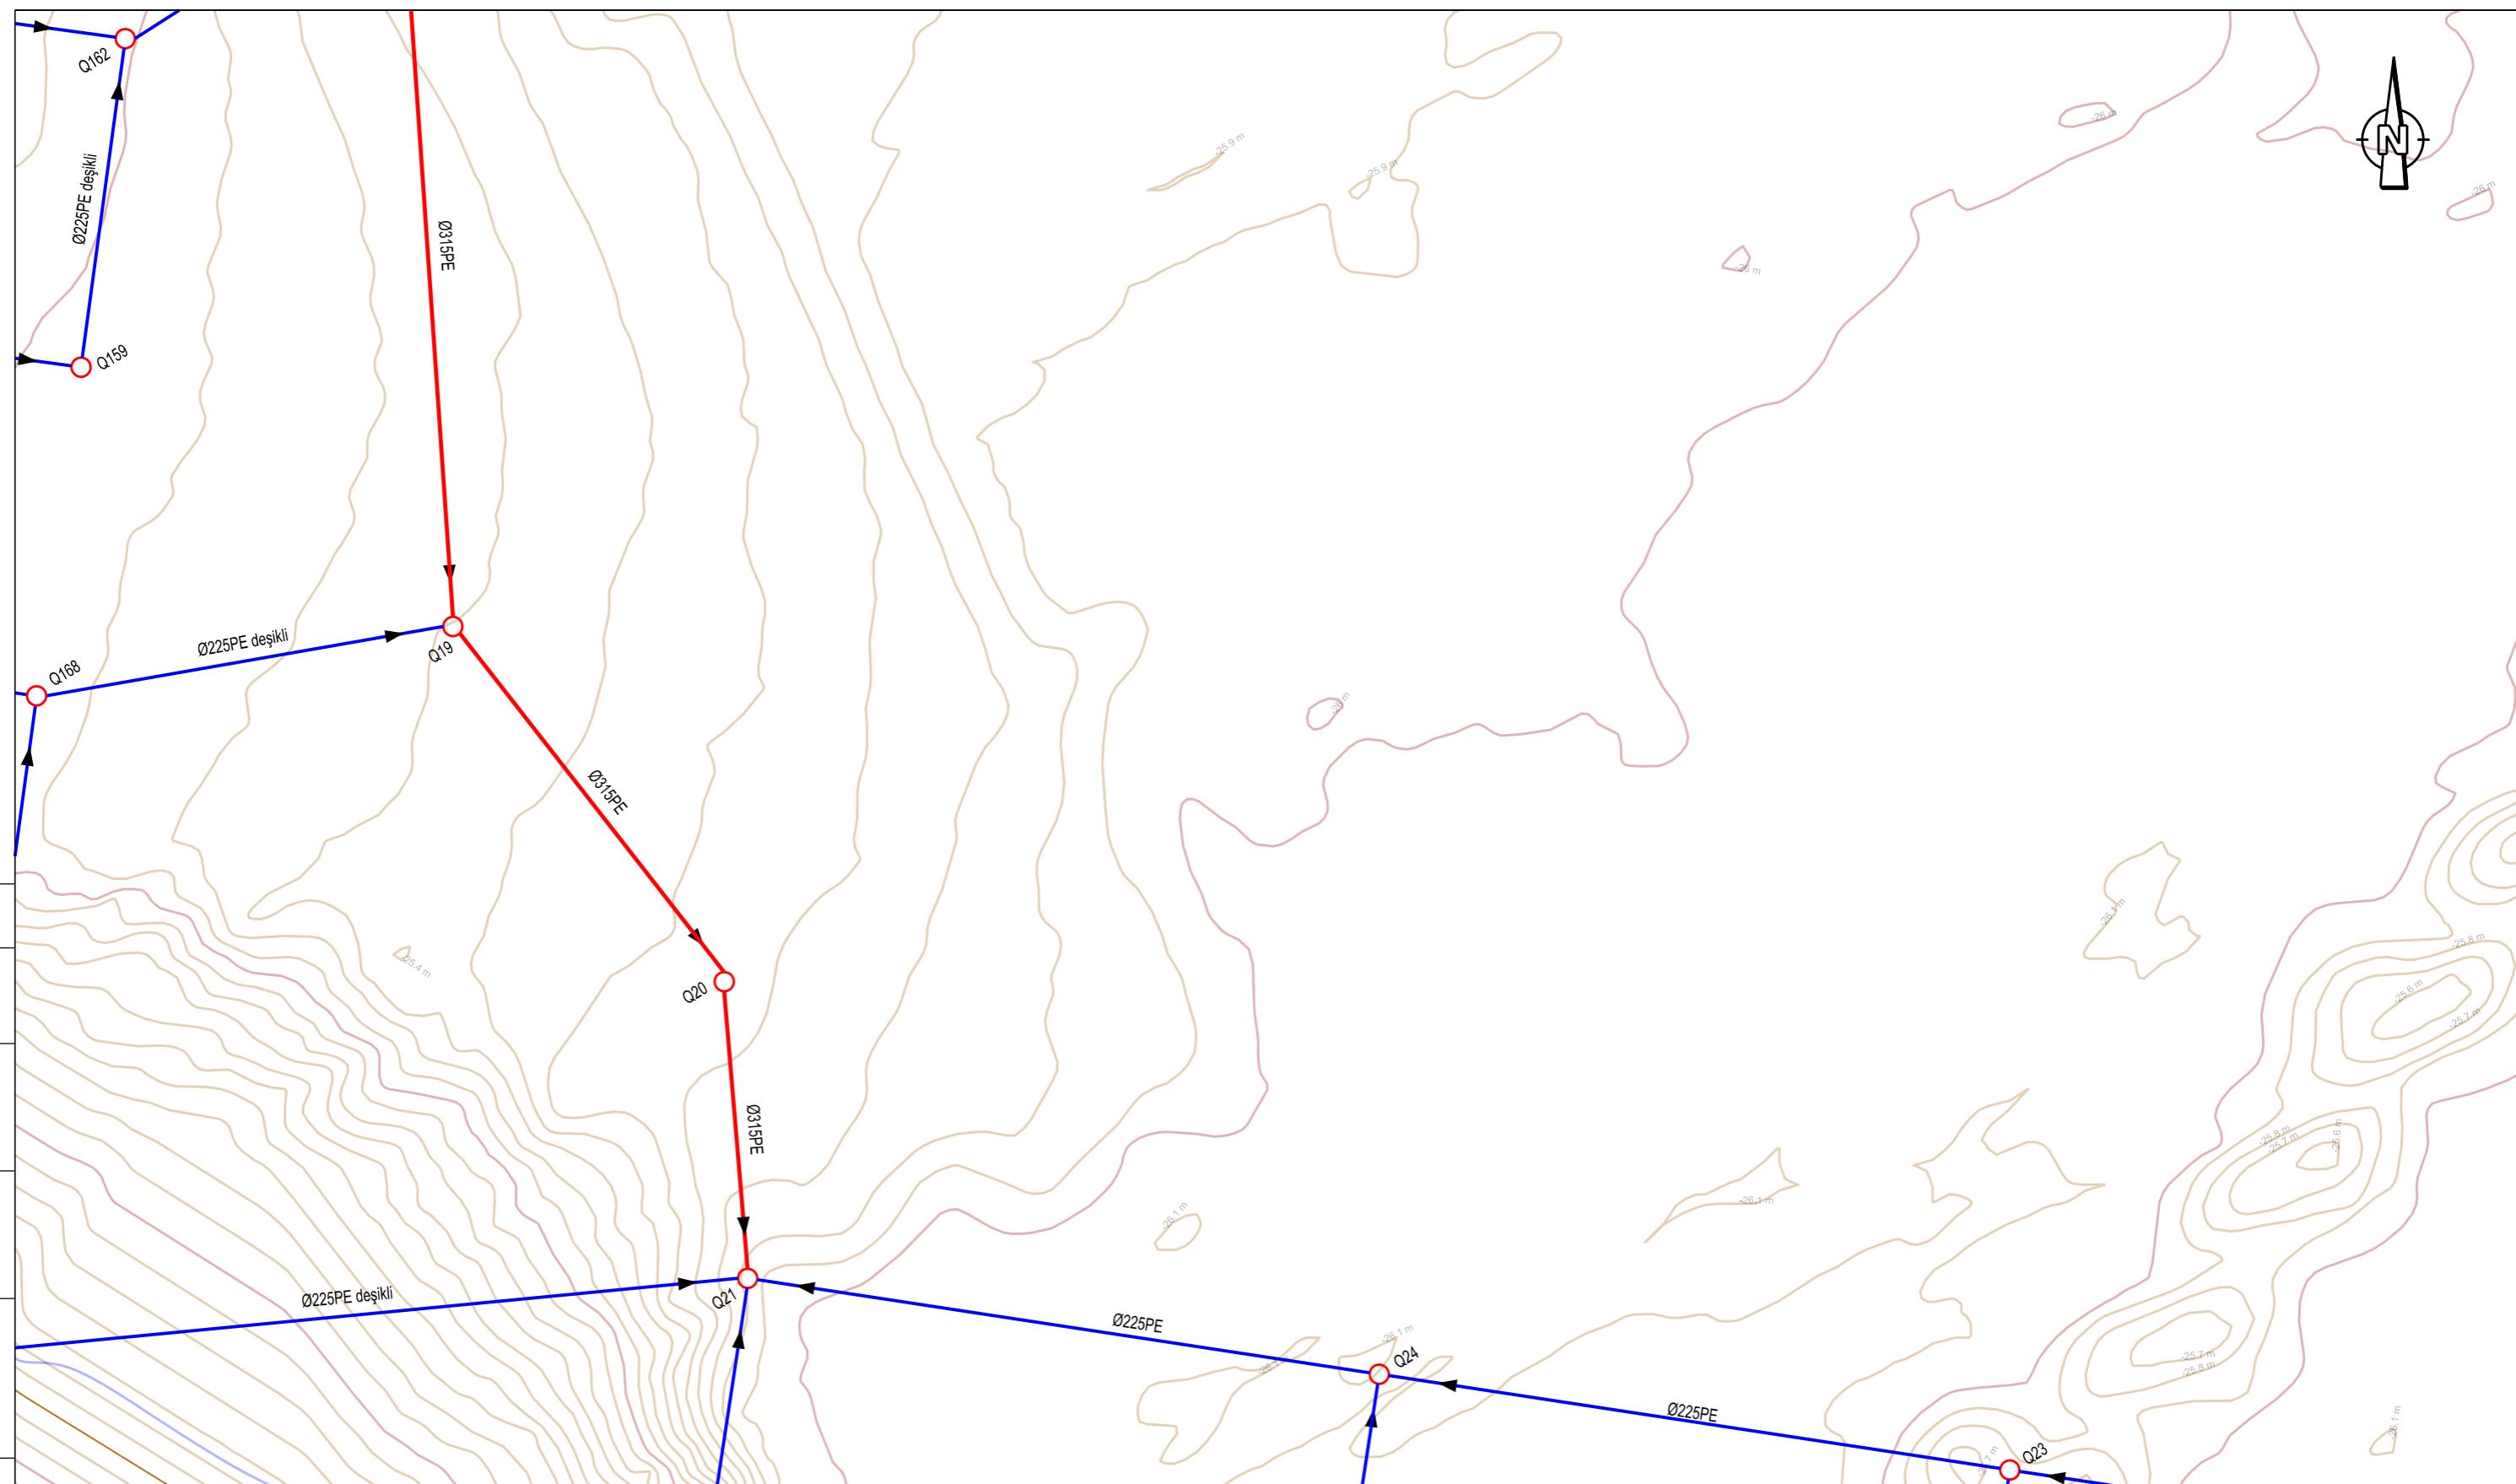

Cizgilərin birləşmə sxemi

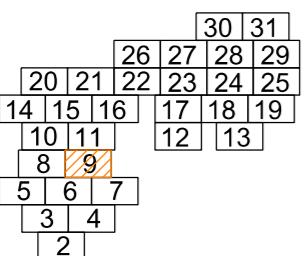

Şərti işarələ

Ø225 HDP

Ø315 HDP

Baxış quyu


2021/AT-04-DS-9.2.1

Tarix Suraxanı rayonunun inzibati ərazisində Zığ gölünün ətrafında yerləşən ərazilərdə yeni yaşlılıqların salınması və damcılı suvarma sisteminin qurulması


Dəyiş.	Dəy.s	Vərəq	Sən.Nö	İmza
LBM	T.Ağayev			
İşlədi	N.Məmmədov			
Yoxladı	A. Aliyev			
Normanəz.	Y. Sitnikova			

Drenaj sistemi

EIB HYDROTRANS ENGINEERING
ENGINEERING CENTER FOR DESIGN OF WATER AND TRANSPORT INFRASTRUCTURE
SU VOQLIQYAT INFRASTRUKTURALARIN LAYHHLIQDILMISIGI OZGI MUMHOSILIK MUSHK

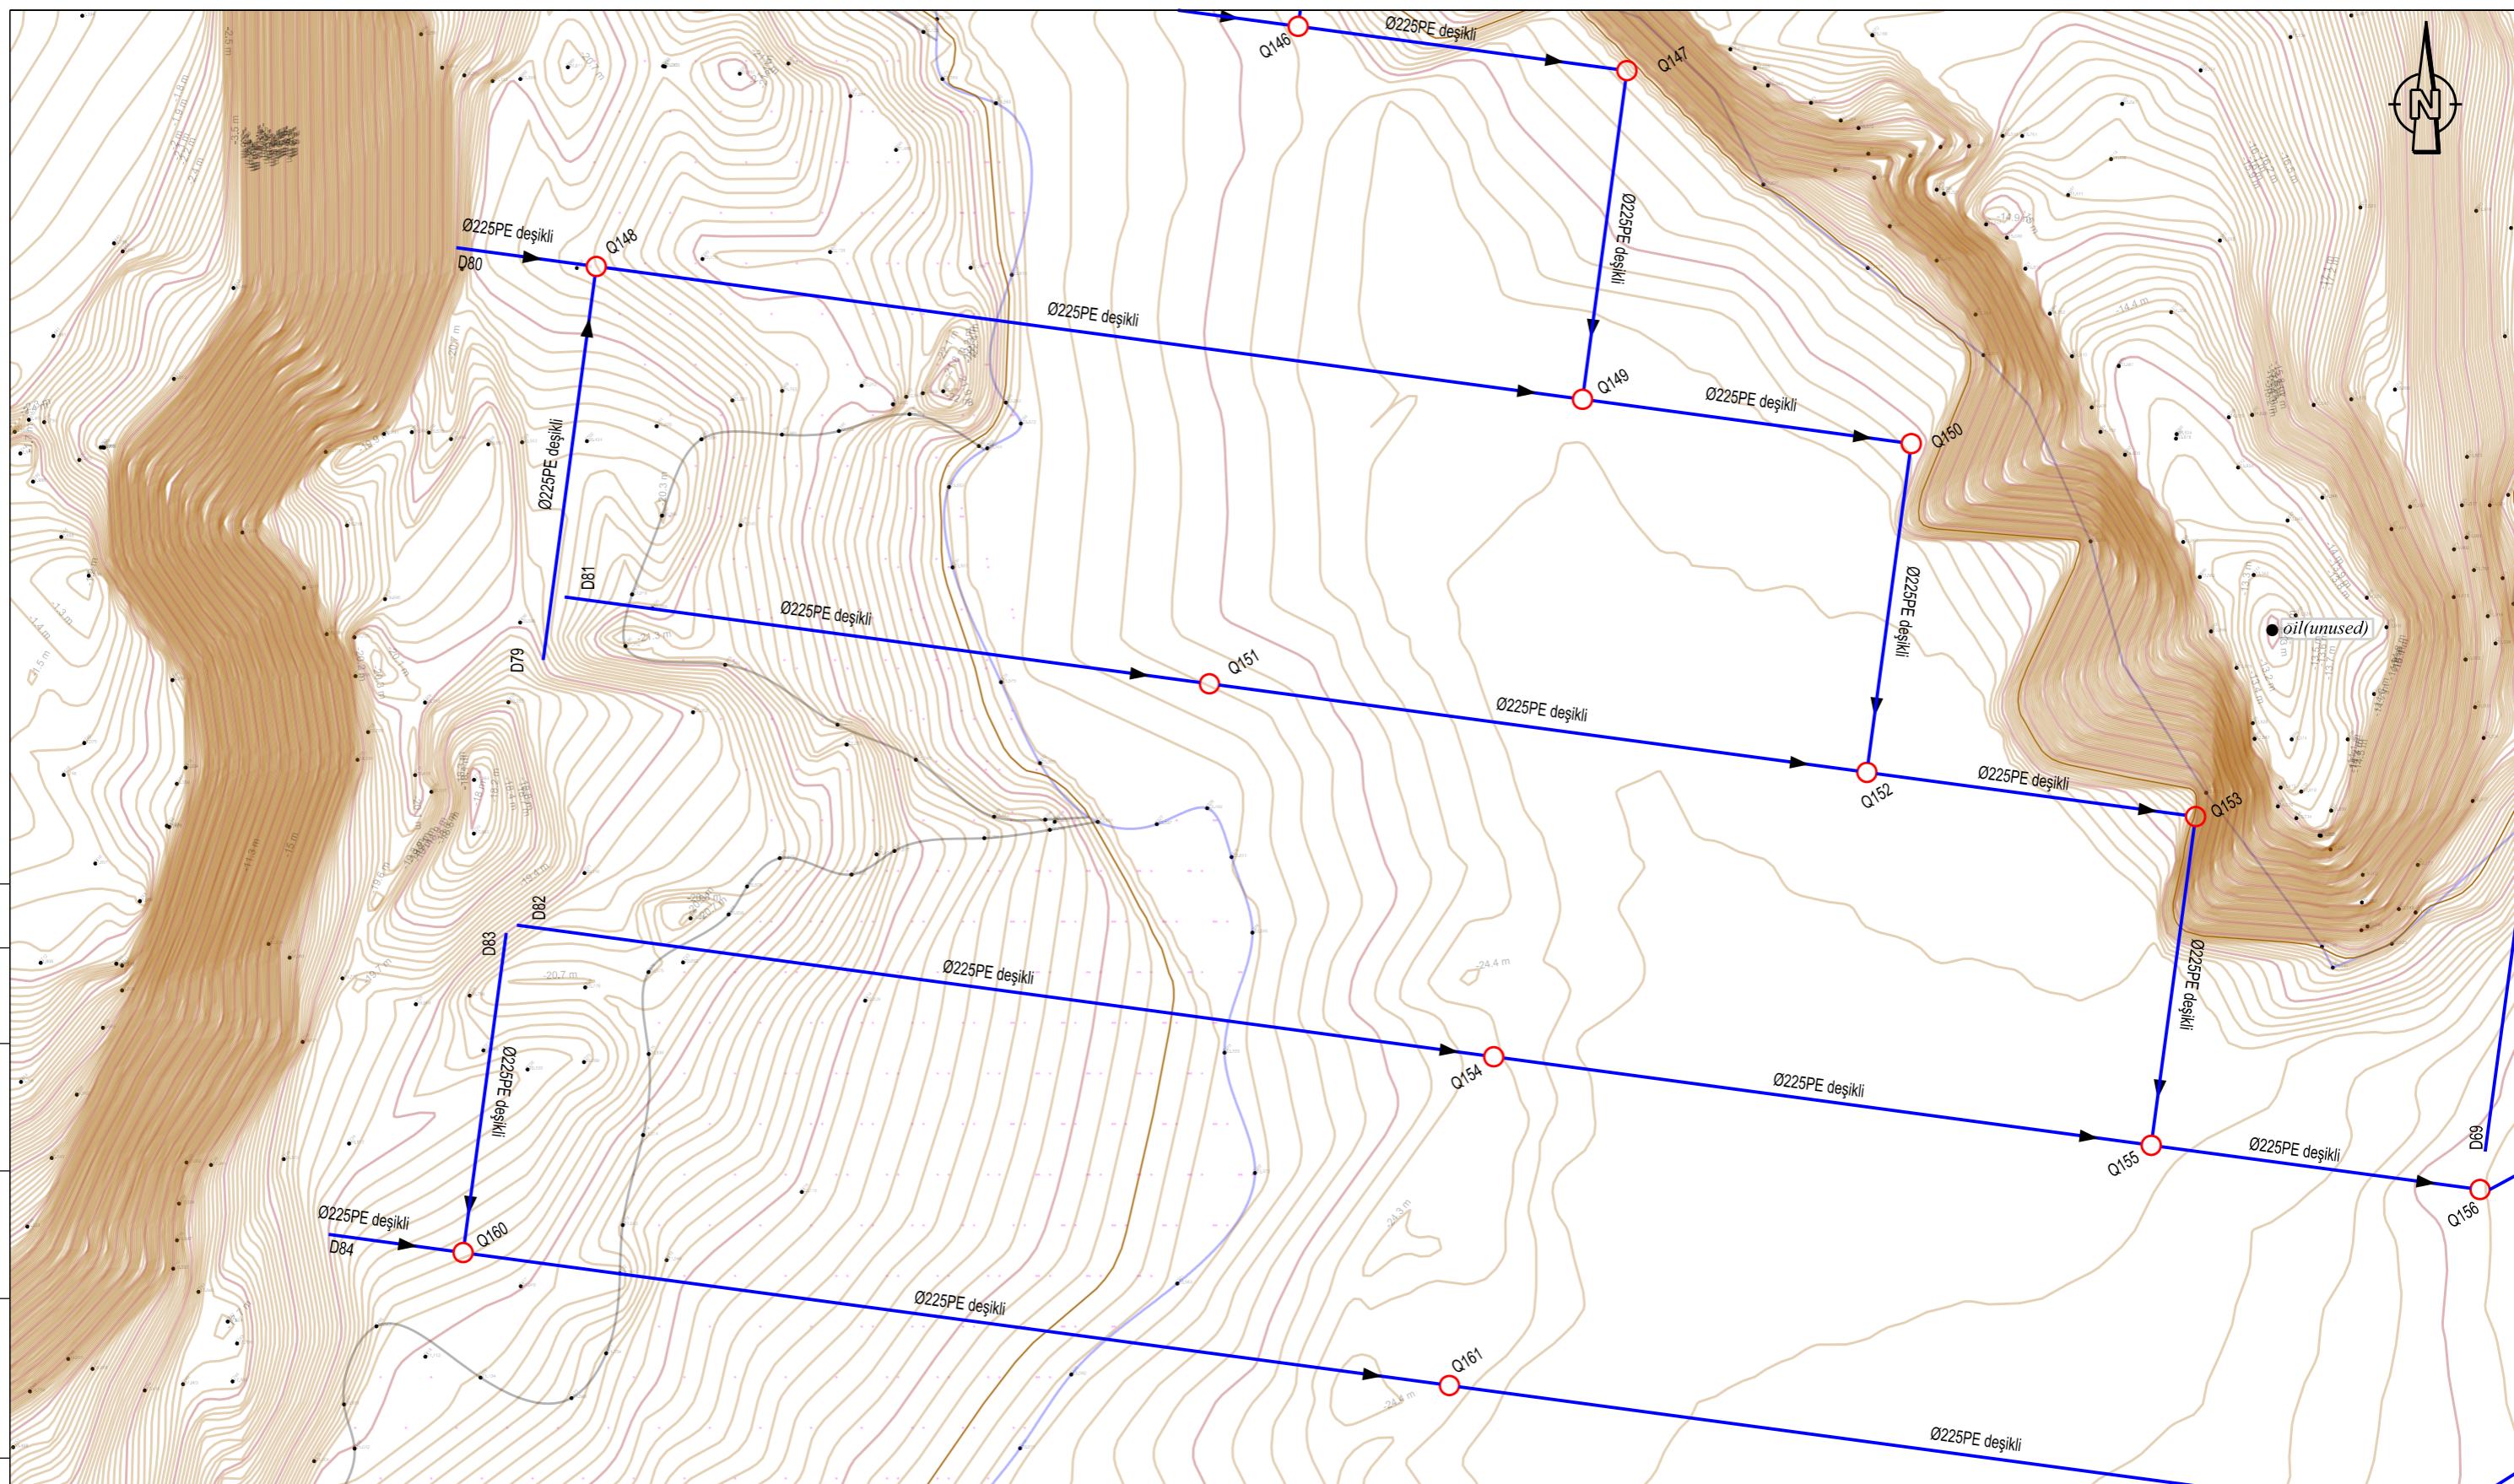

Cizgilərin birləşmə sxemi

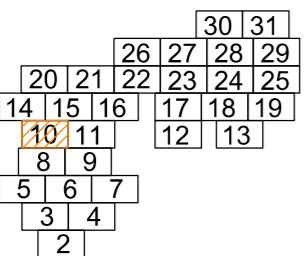

Şərti işaretələr

Ø225 HDPE

Ø315 HDPE

Baxış quyusu



2021/AT-04-DS-9.2.1


Suraxanı rayonunun inzibati ərazisində Zığ gölünün ətrafında yerləşən ərazilərdə yeni yaşlılıqların salınması və damcılı suvarma sisteminin qurulması

Dəyiş.	Dəy.s	Vərəq	Sən.Nö	İmza	T
LBM		T.Ağayev			
İşlədi		N.Məmmədov			
Yoxladı		A. Aliyev			
Normanəz.		Y. Sitnikova			

Drenaj sistemi

EIB HYDROTRANS ENGINEERING
ENGINEERING CENTER FOR DESIGN OF WATER AND TRANSPORT INFRASTRUCTURE
SUVA NOGIVET INFRASTRUCTURE IN LAVUOLTOHÜ MÖÖDÜ MUHAKÖNS Í MÖÖDÜ


Format A3

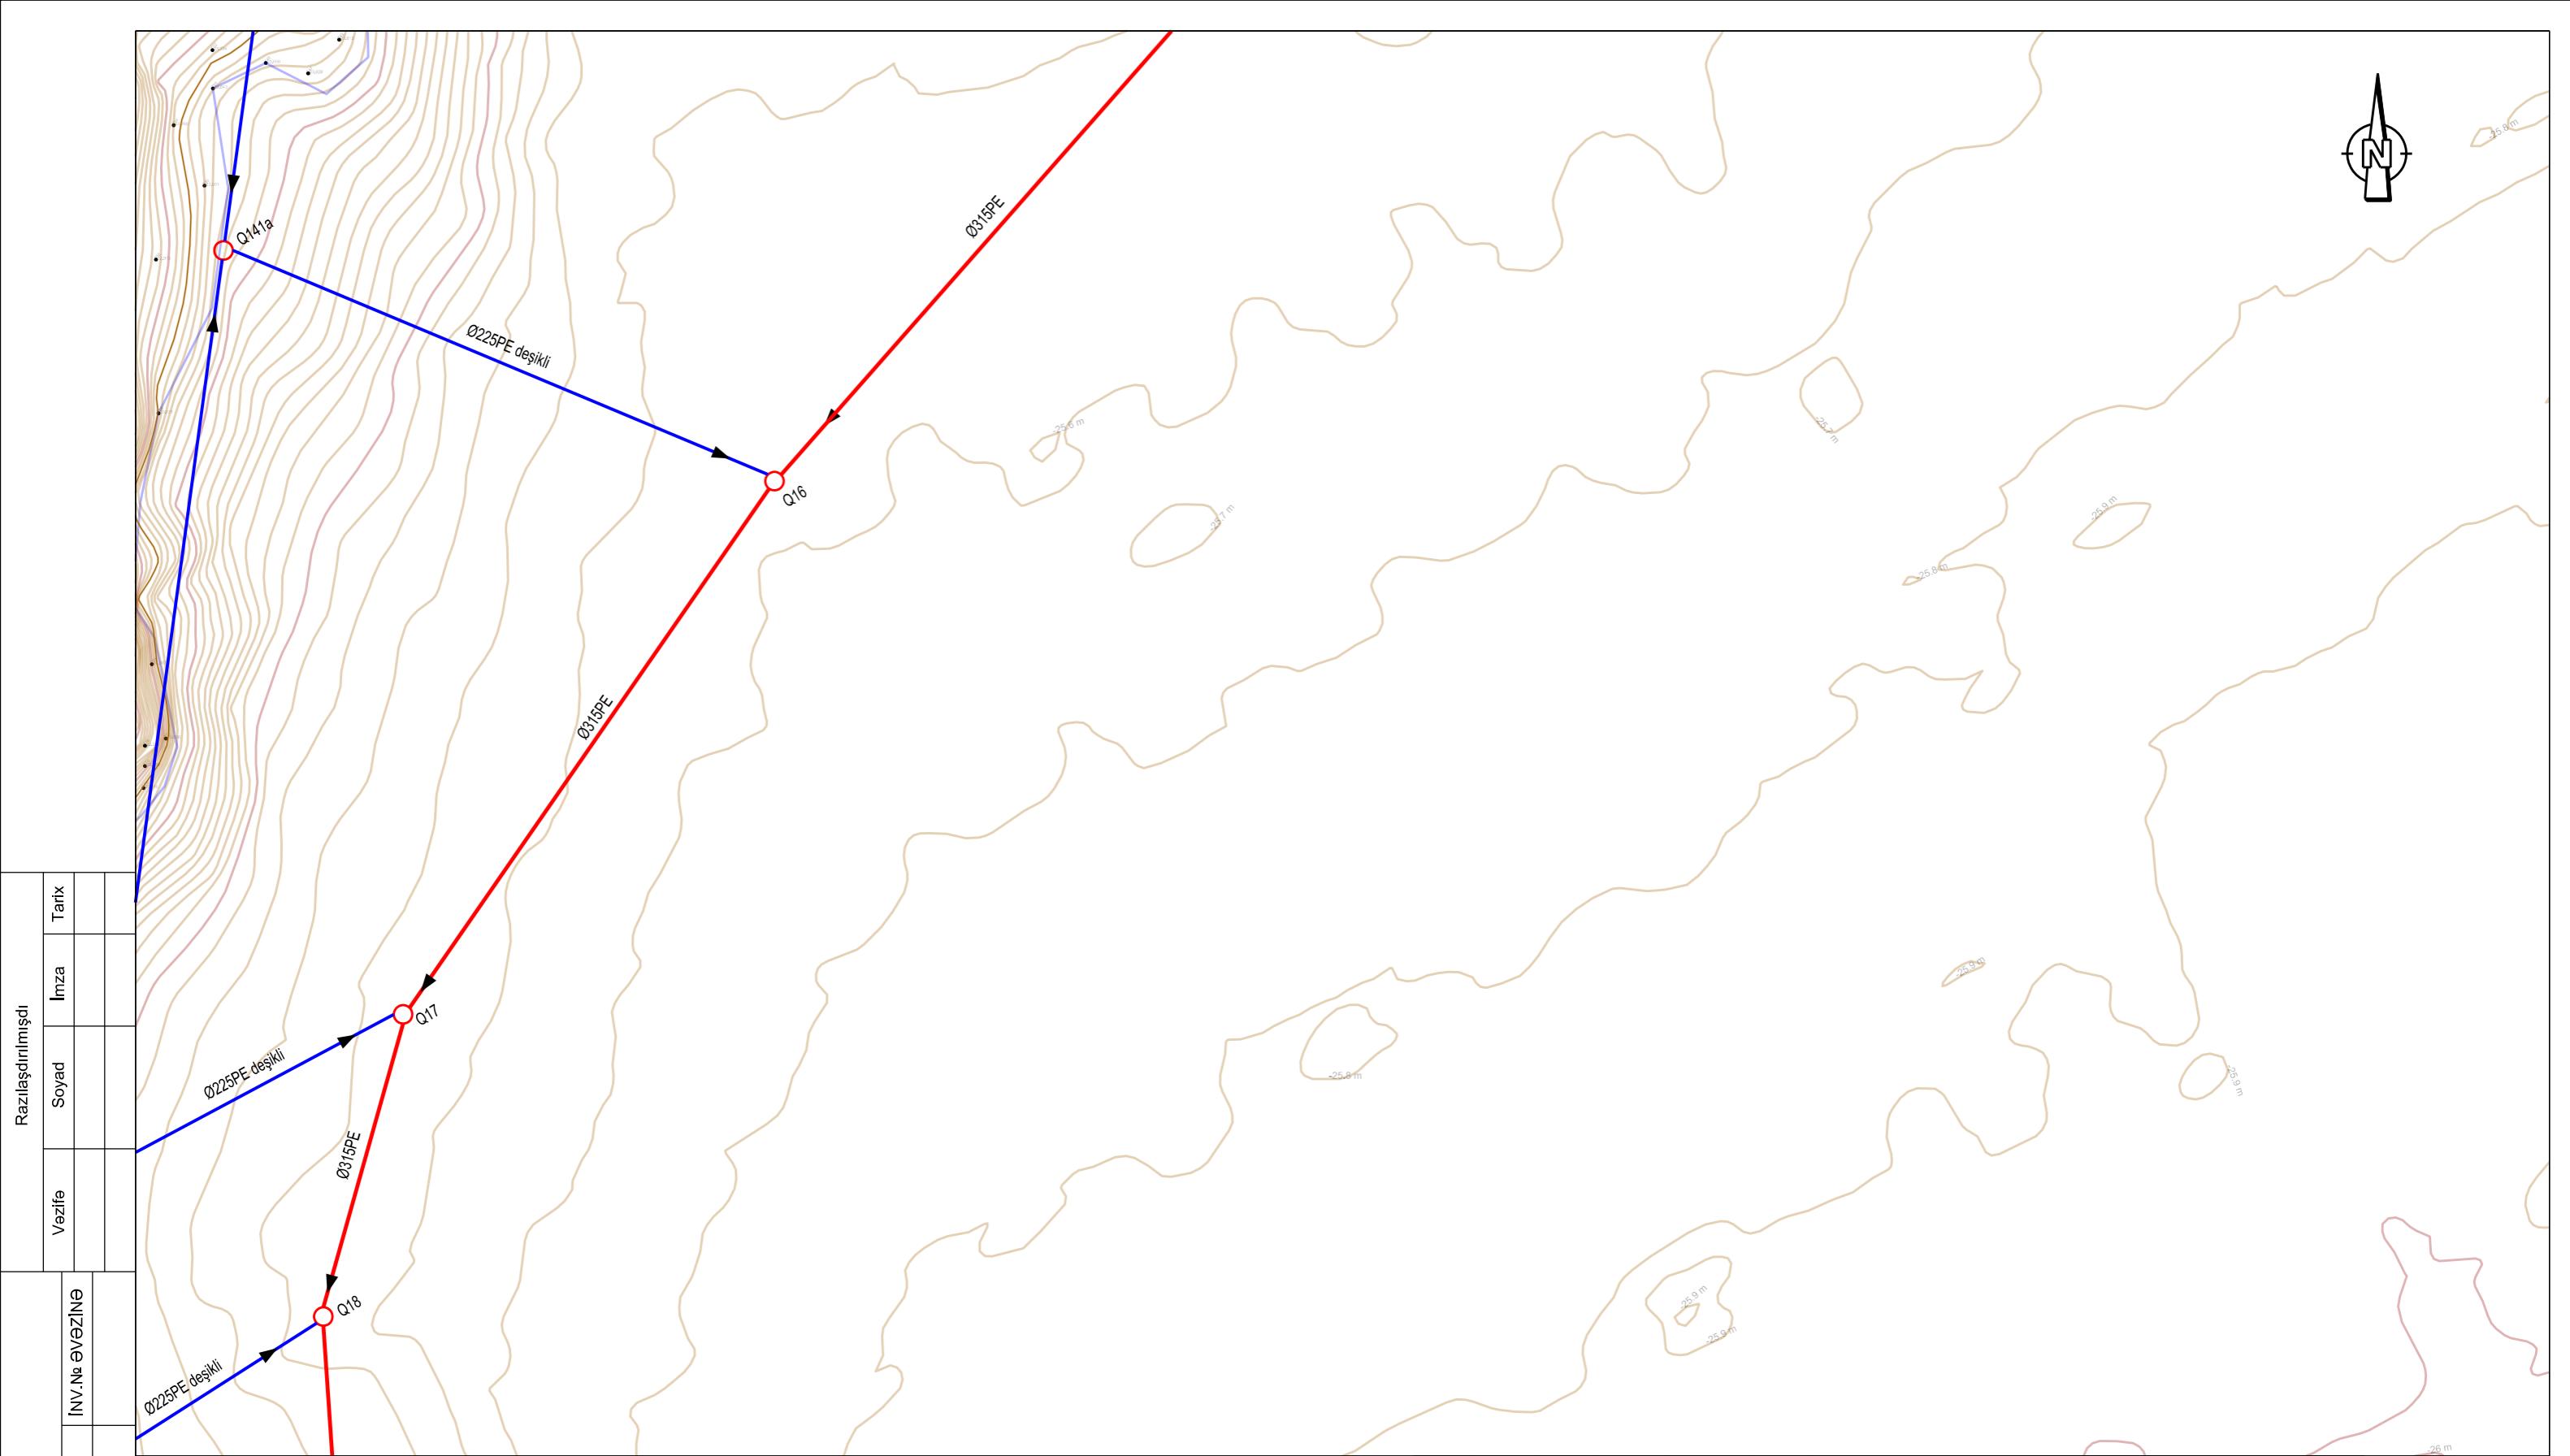

Razlaşdırılmışdı					
Vəzifə	Soyad	İmza	Tarix		

INVENTAR №	IMZA VƏ TARIX	INV.NƏŞEVƏZİNƏ

Cizgilərin birləşmə sxemi

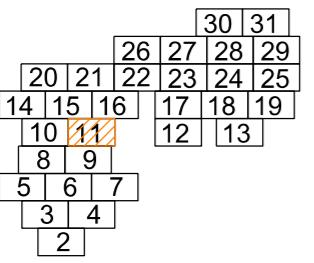

Şerti işarələr



Ø225 HDPE



Ø315 HDPE



Baxış quyusu

2021/AT-04-DS-9.2.1

Suraxanı rayonunun inzibati ərazisində Zığ gölünün ətrafında
yerləşən ərazilərdə yeni yaşlılıqların salınması və damcılı suvarma
sisteminin qurulması

Dəyiş.	Dəy.s	Vərəq	Sən.Nə	İmza	Tarix
LBM	T.Ağayev				
İşlədi	N.Məmmədov				
Yoxladı	A. Aliyev				
Normanəz.	Y. Sitnikova				

Drenaj sistemi


mərhələ vərəq vərəqlər

İL 11 84

Drenaj sistemi planı(davamı)


EIB HYDROTRANS ENGINEERING

SU VƏ NƏqliyyat İnfrastrukturlarının Lətişləndirilməsi Üzrə Məmənliklilik Mərkəzi

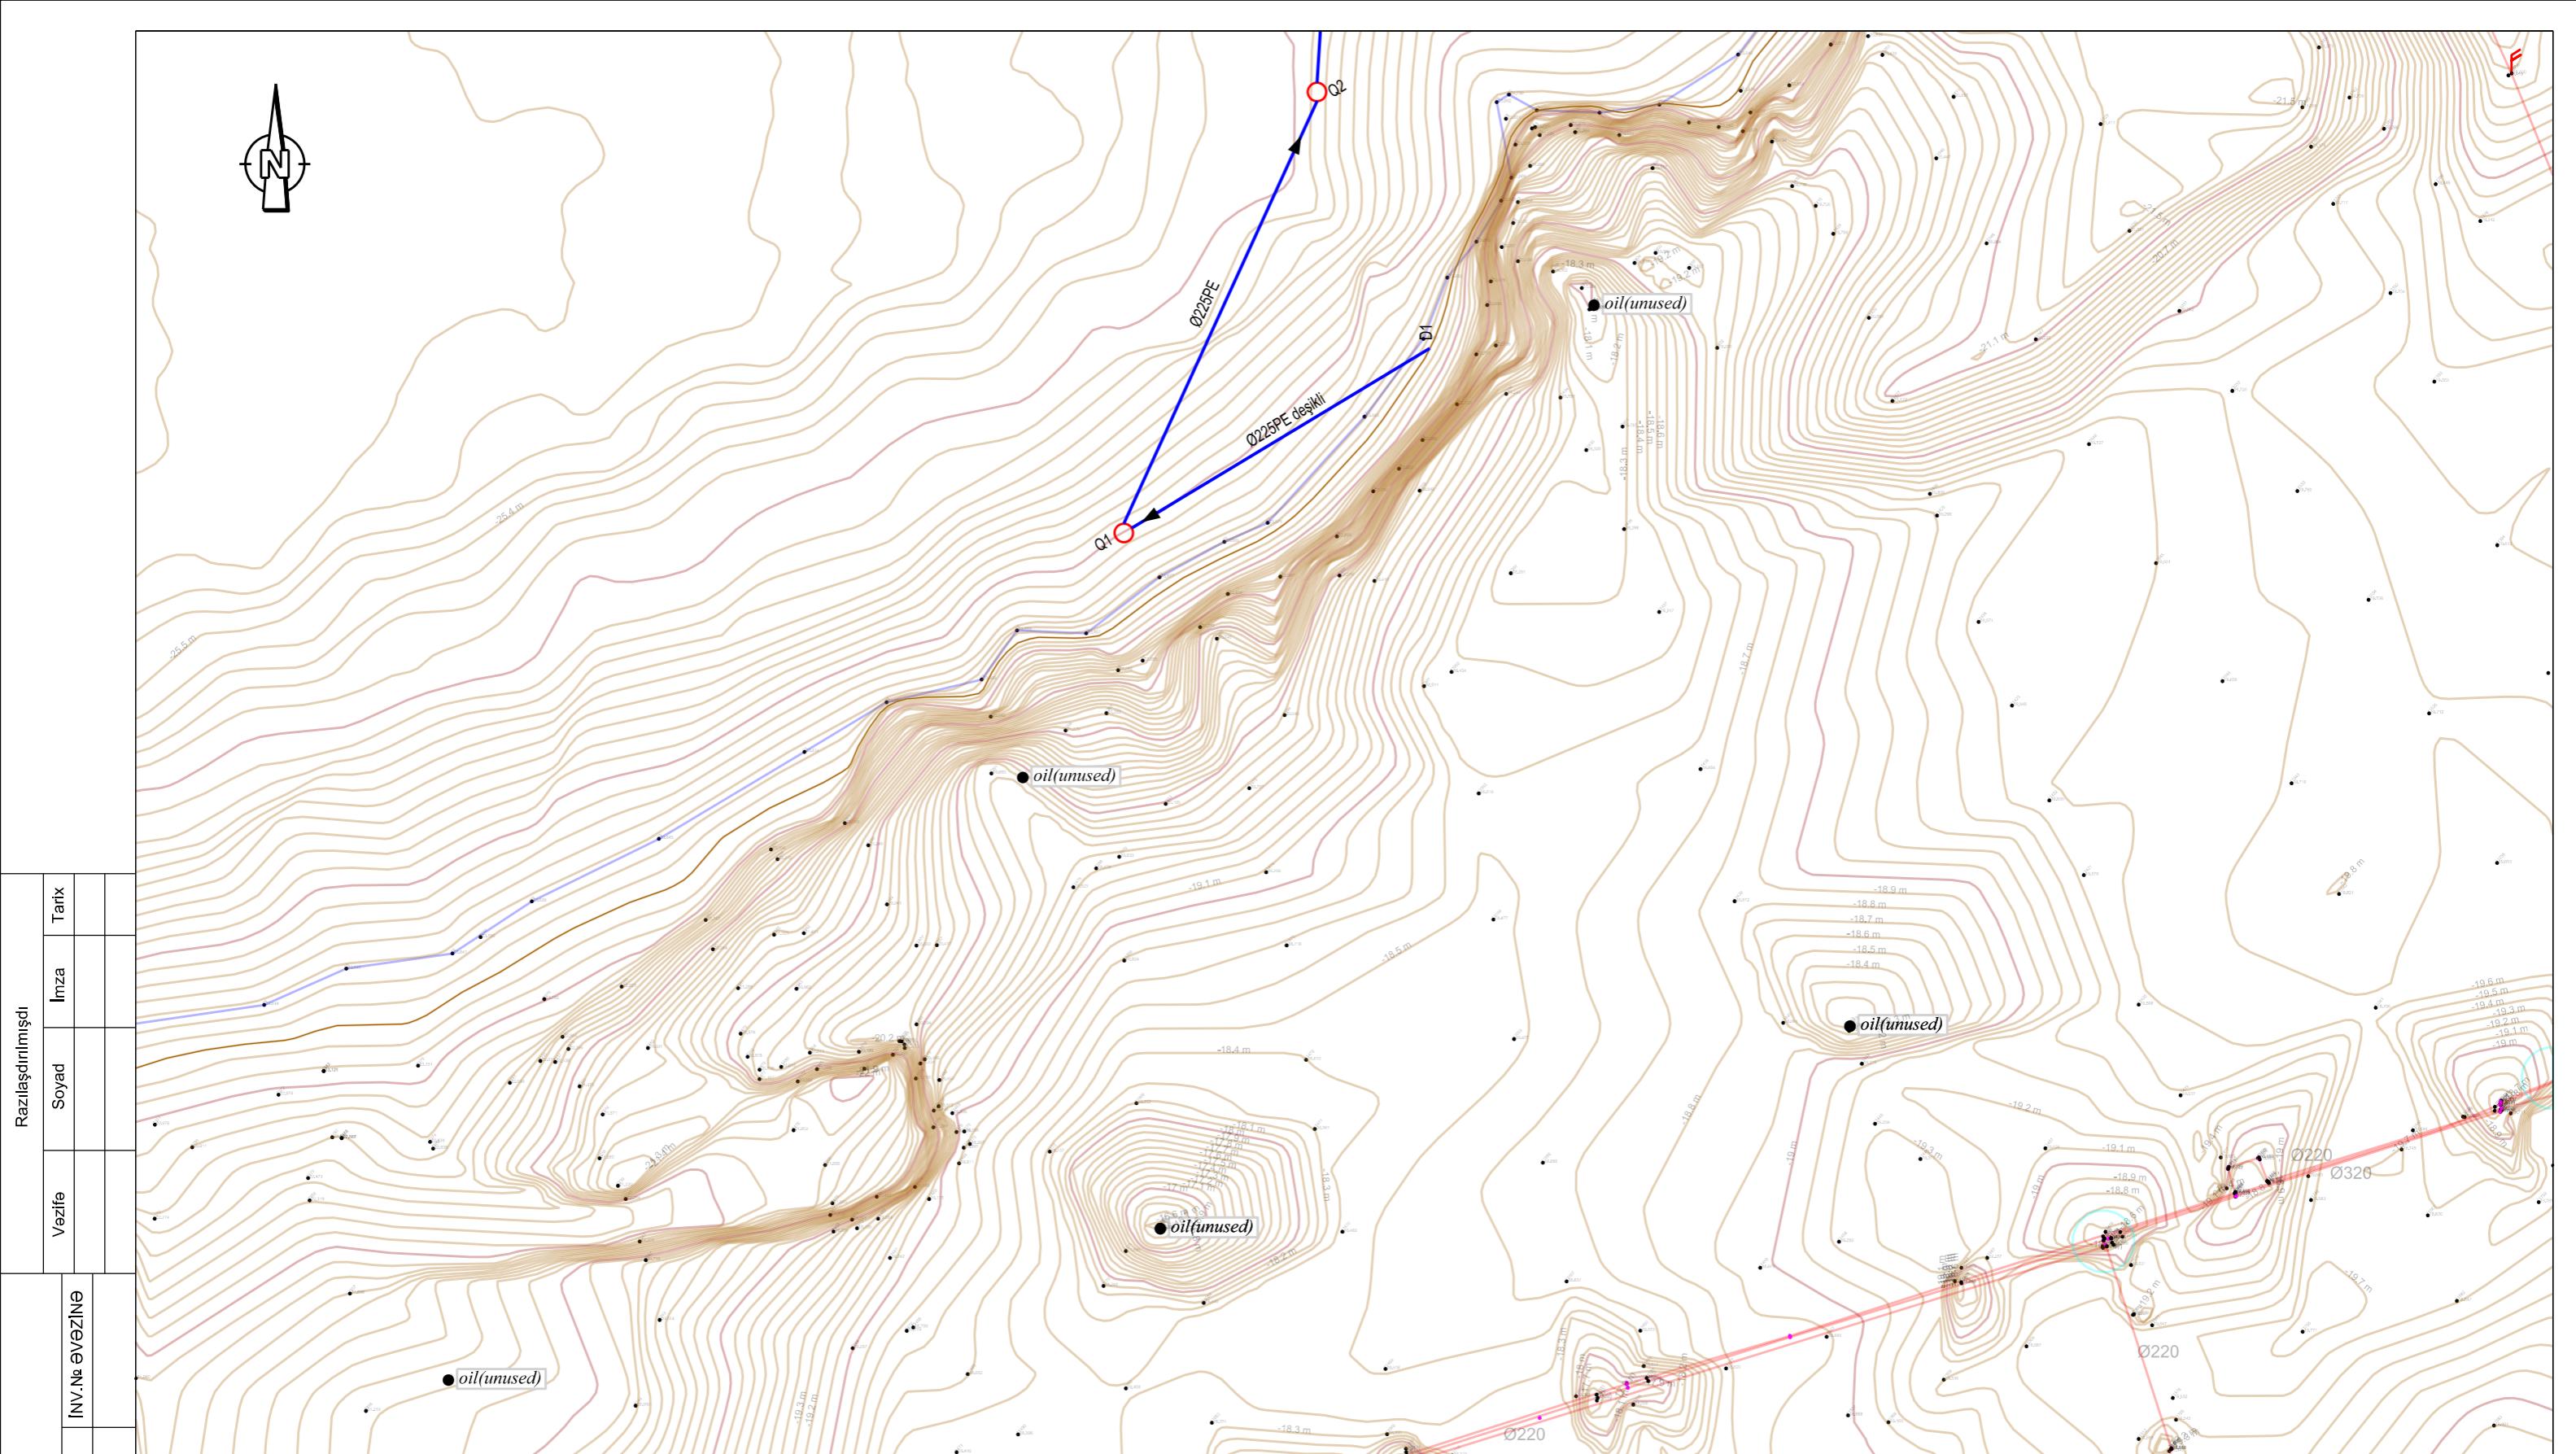

INVENTAR №	IMZA VƏ TARİX	INV.NƏŞVƏZİNƏ	Razlaşdırılmışdı
Vəzifə	Soyad	İmza	Tarix

Cizgilərin birləşmə sxemi

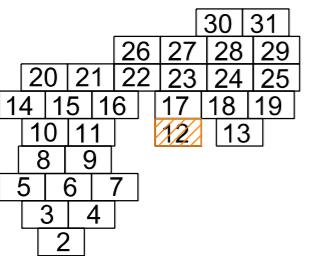

Şerti işaretlər



Ø225 HDPE



Ø315 HDPE




Baxış quyusu

2021/AT-04-DS-9.2.1


Suraxanı rayonunun inzibati ərazisində Zığ gölünün ətrafında
yerləşən ərazilərdə yeni yaşlılıqların salınması və damcılı suvarma
sisteminin qurulması

Dəyiş.	Dəy.s	Vərəq	Sən.Nö	İmza	Tarix
LBM	T.Ağayev				
İşlədi	N.Məmmədov				
Yoxladı	A. Aliyev				
Normanəz.	Y. Sitnikova				

Drenaj sistemi planı(davamı)

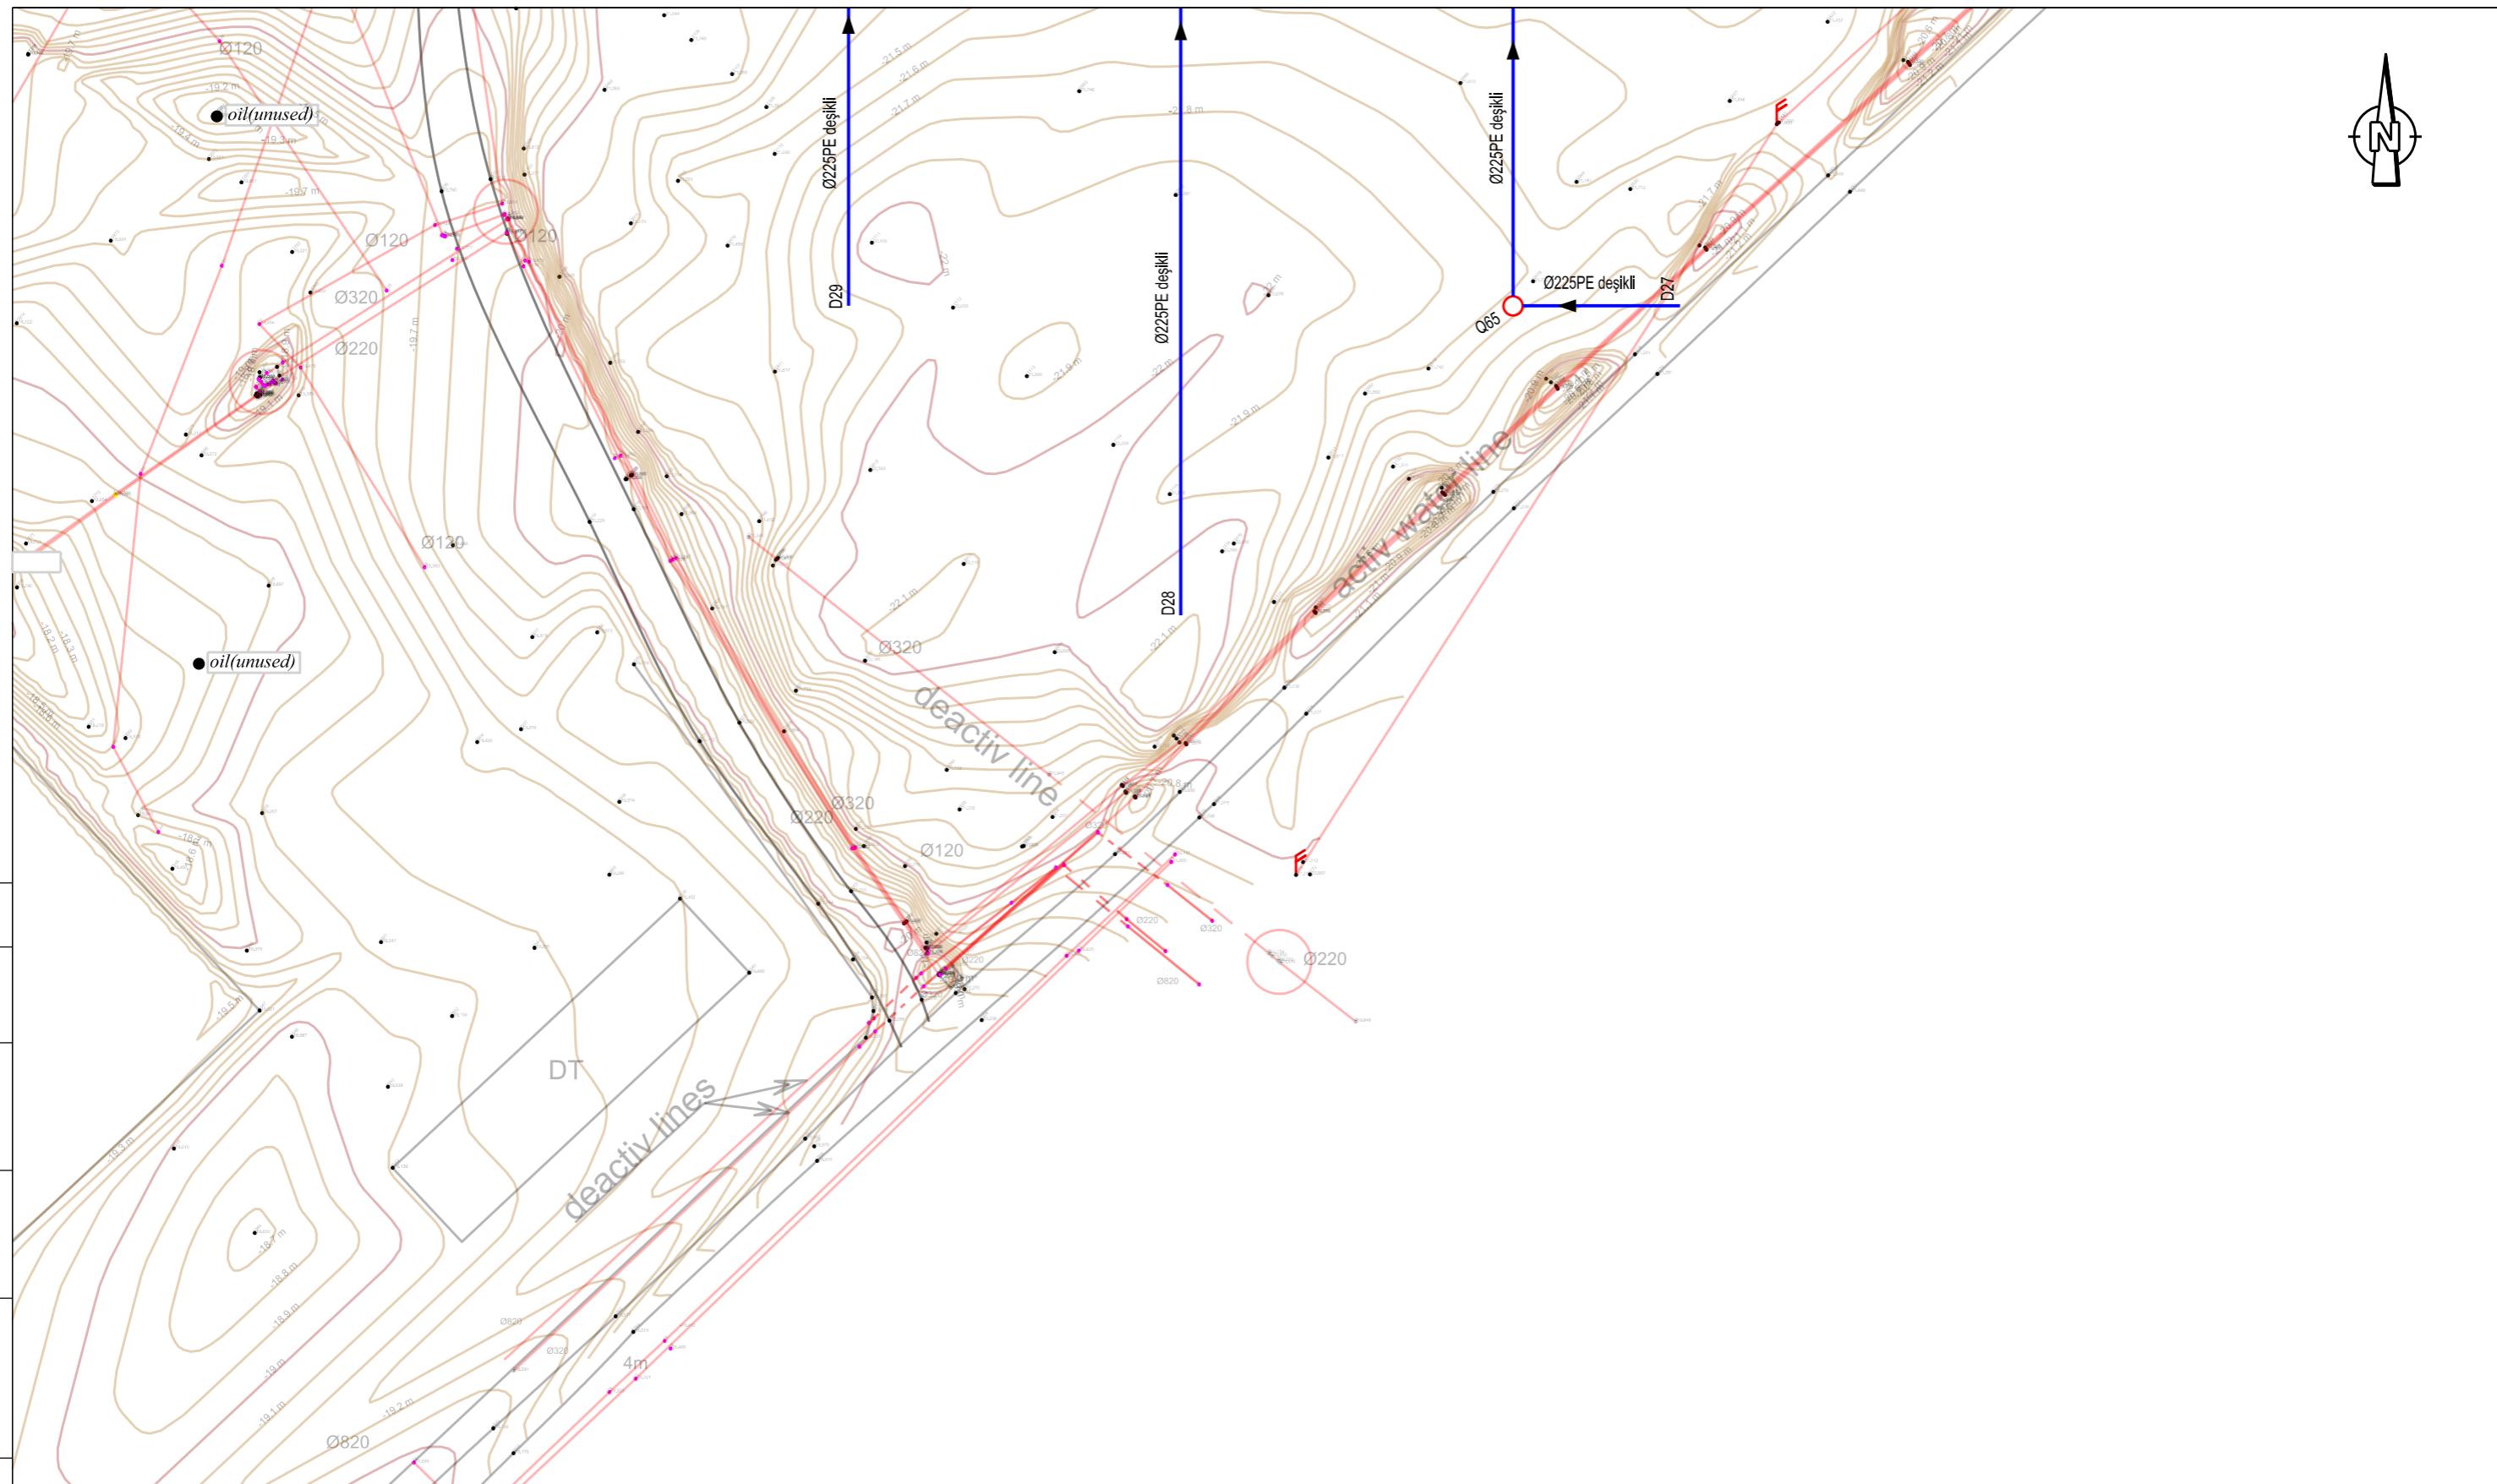

Cizgilərin birləşmə sxemi

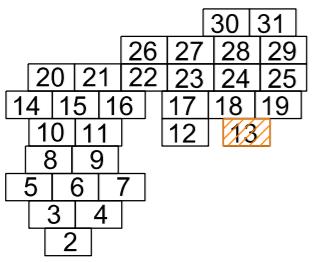

Şərti işarələ

Ø225 HDP

Ø315 HDP


Baxış quyu

— 1 —

○

2021/AT-04-DS-9.2.1


Suraxanı rayonunun inzibati ərazisində Zığ gölünün ətrafında
yerləşən ərazilərdə yeni yaşlılıqların salınması və damcılı suvarma
sisteminin qurulması

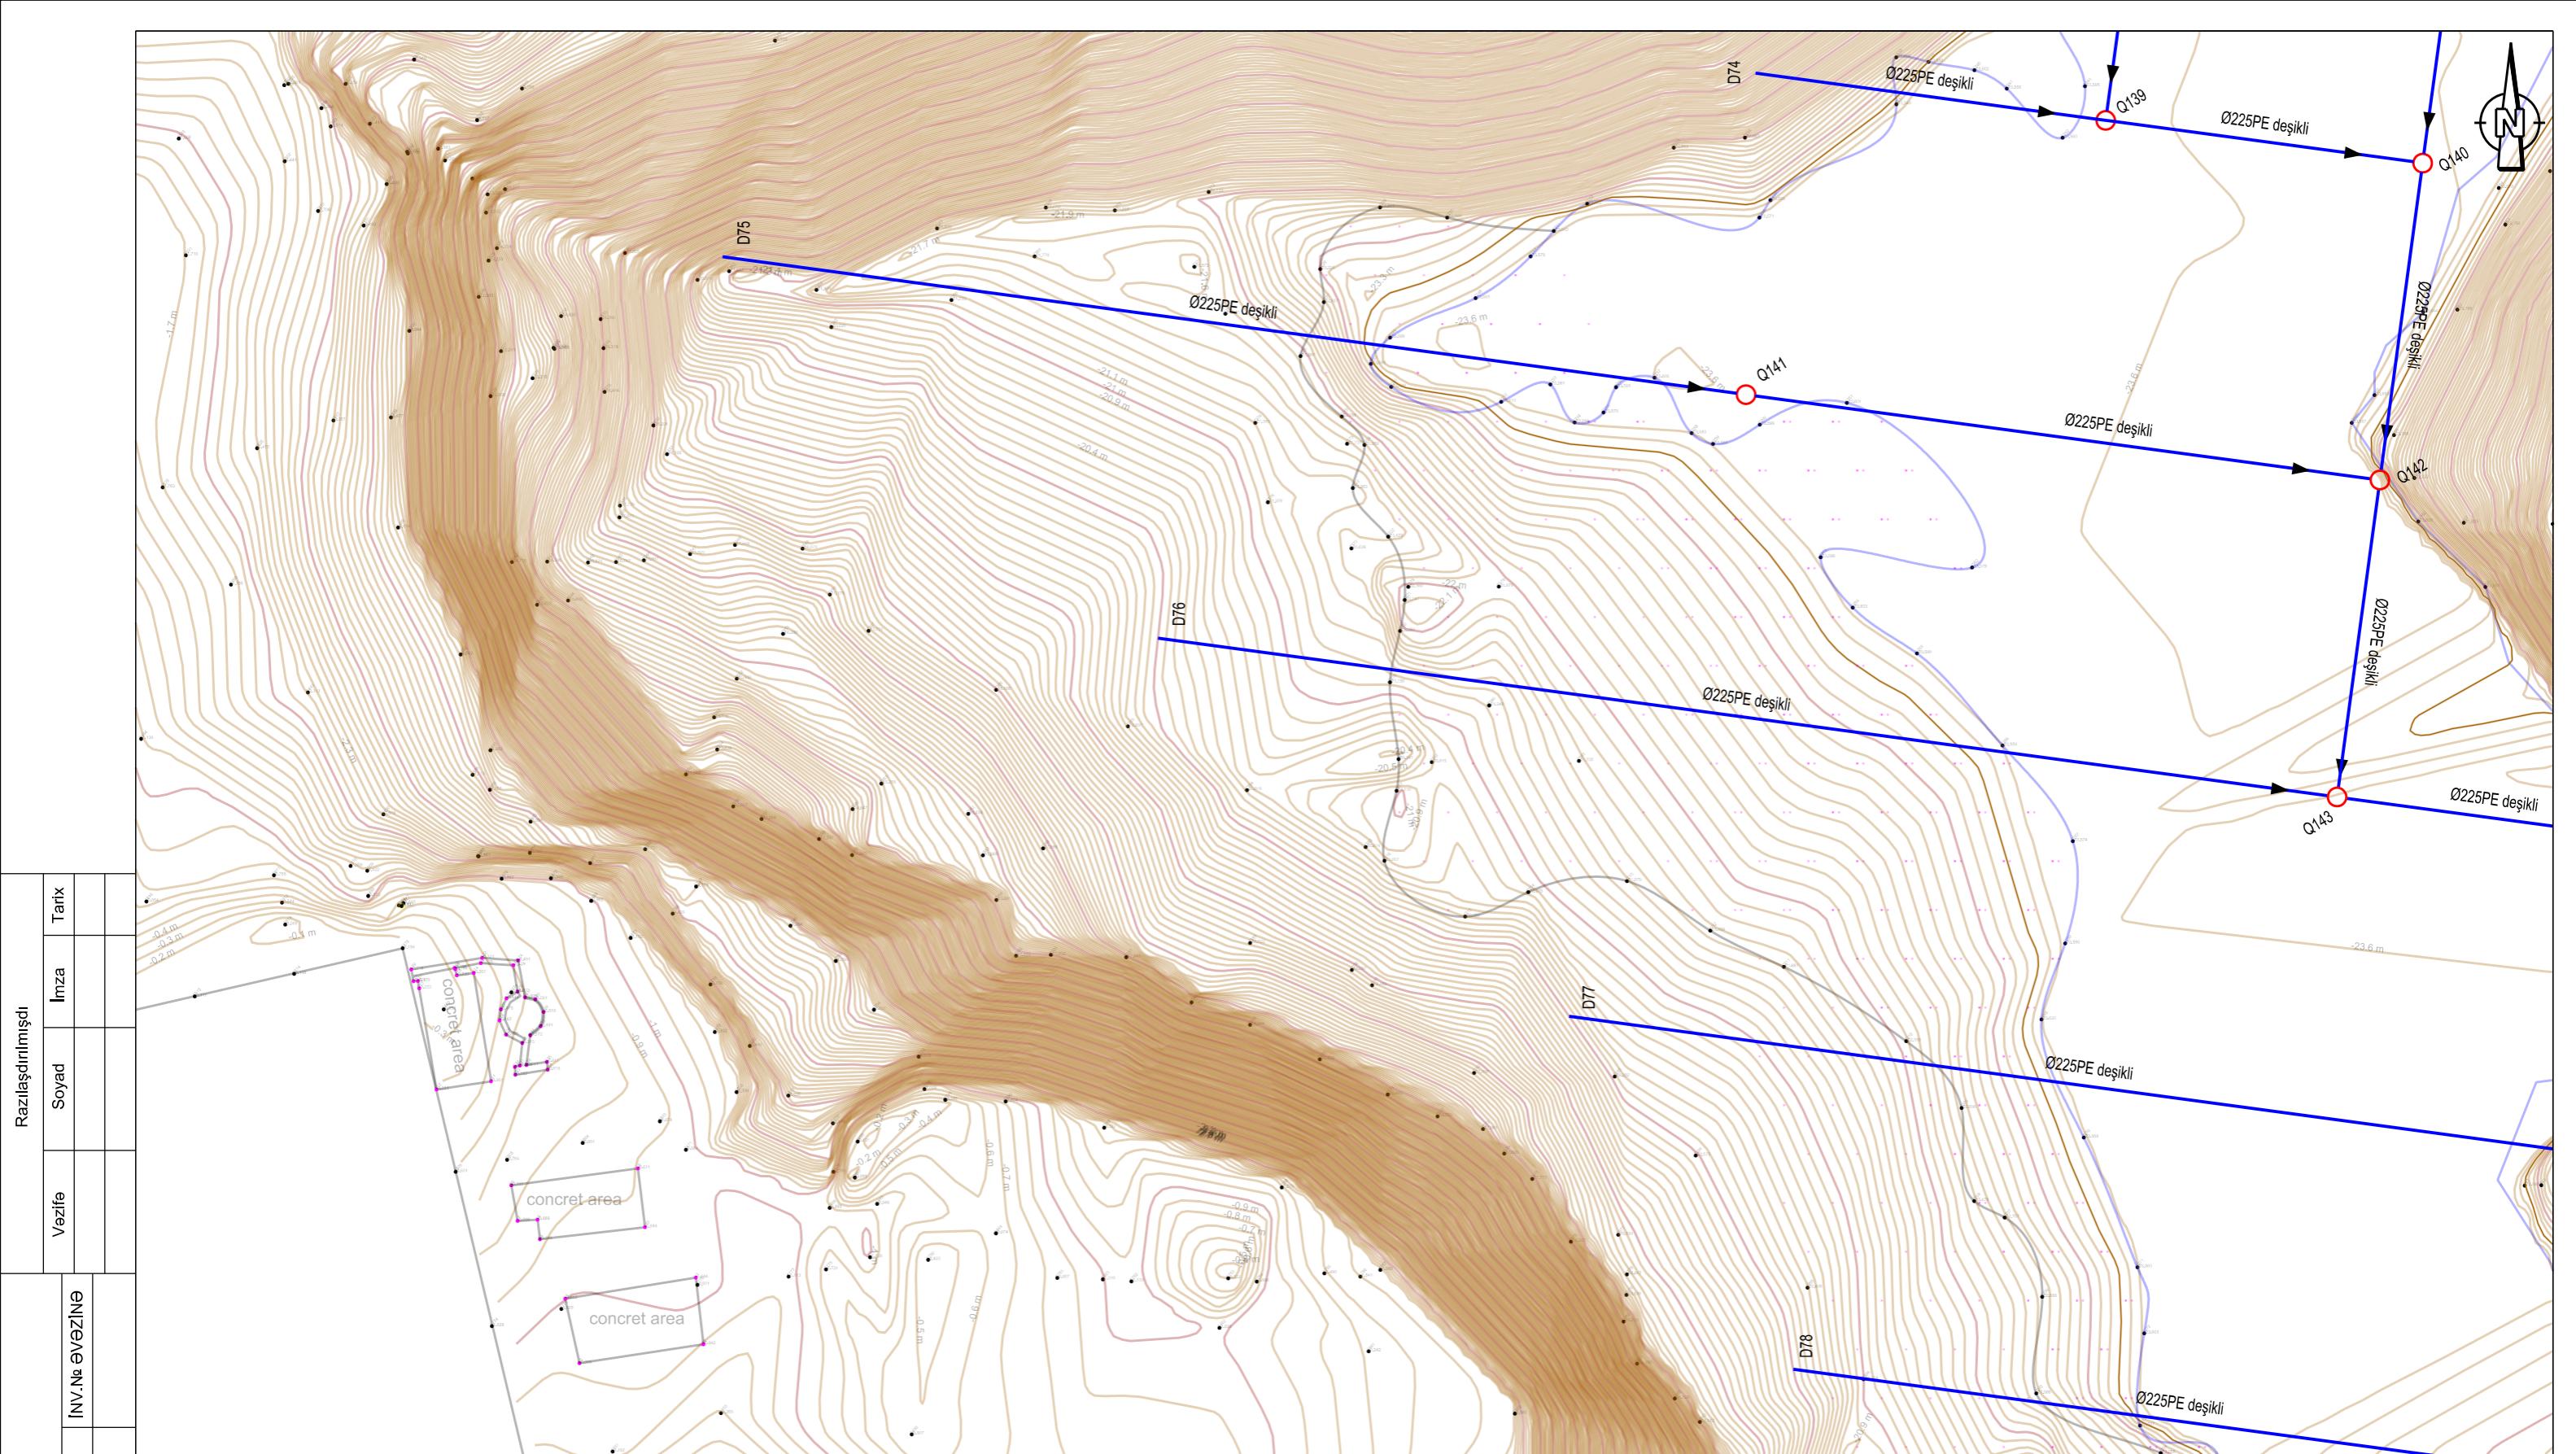

Razlaşdırılmışlı					
Vəzifə	Soyad	İmza	Tarix		

INVENTAR №	IMZA VƏ TARIX	INV.NƏŞEVƏZİNƏ

Cizgilərin birləşmə sxemi

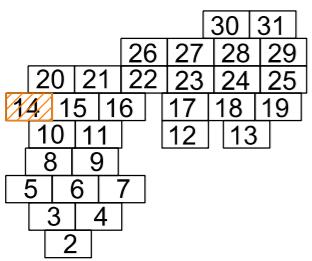

Şerti işarələr



Ø225 HDPE



Ø315 HDPE




Baxış quyusu

2021/AT-04-DS-9.2.1

Suraxanı rayonunun inzibati ərazisində Zığ gölünün ətrafında
yerləşən ərazilərdə yeni yaşlılıqların salınması və damcılı suvarma
sisteminin qurulması

Dəyiş.	Dəy.s	Vərəq	Sən.Nö	İmza	Tarix
LBM	T.Ağayev				
İşlədi	N.Məmmədov				
Yoxladı	A. Aliyev				
Normanəz.	Y. Sitnikova				

Drenaj sistemi planı(davamı)

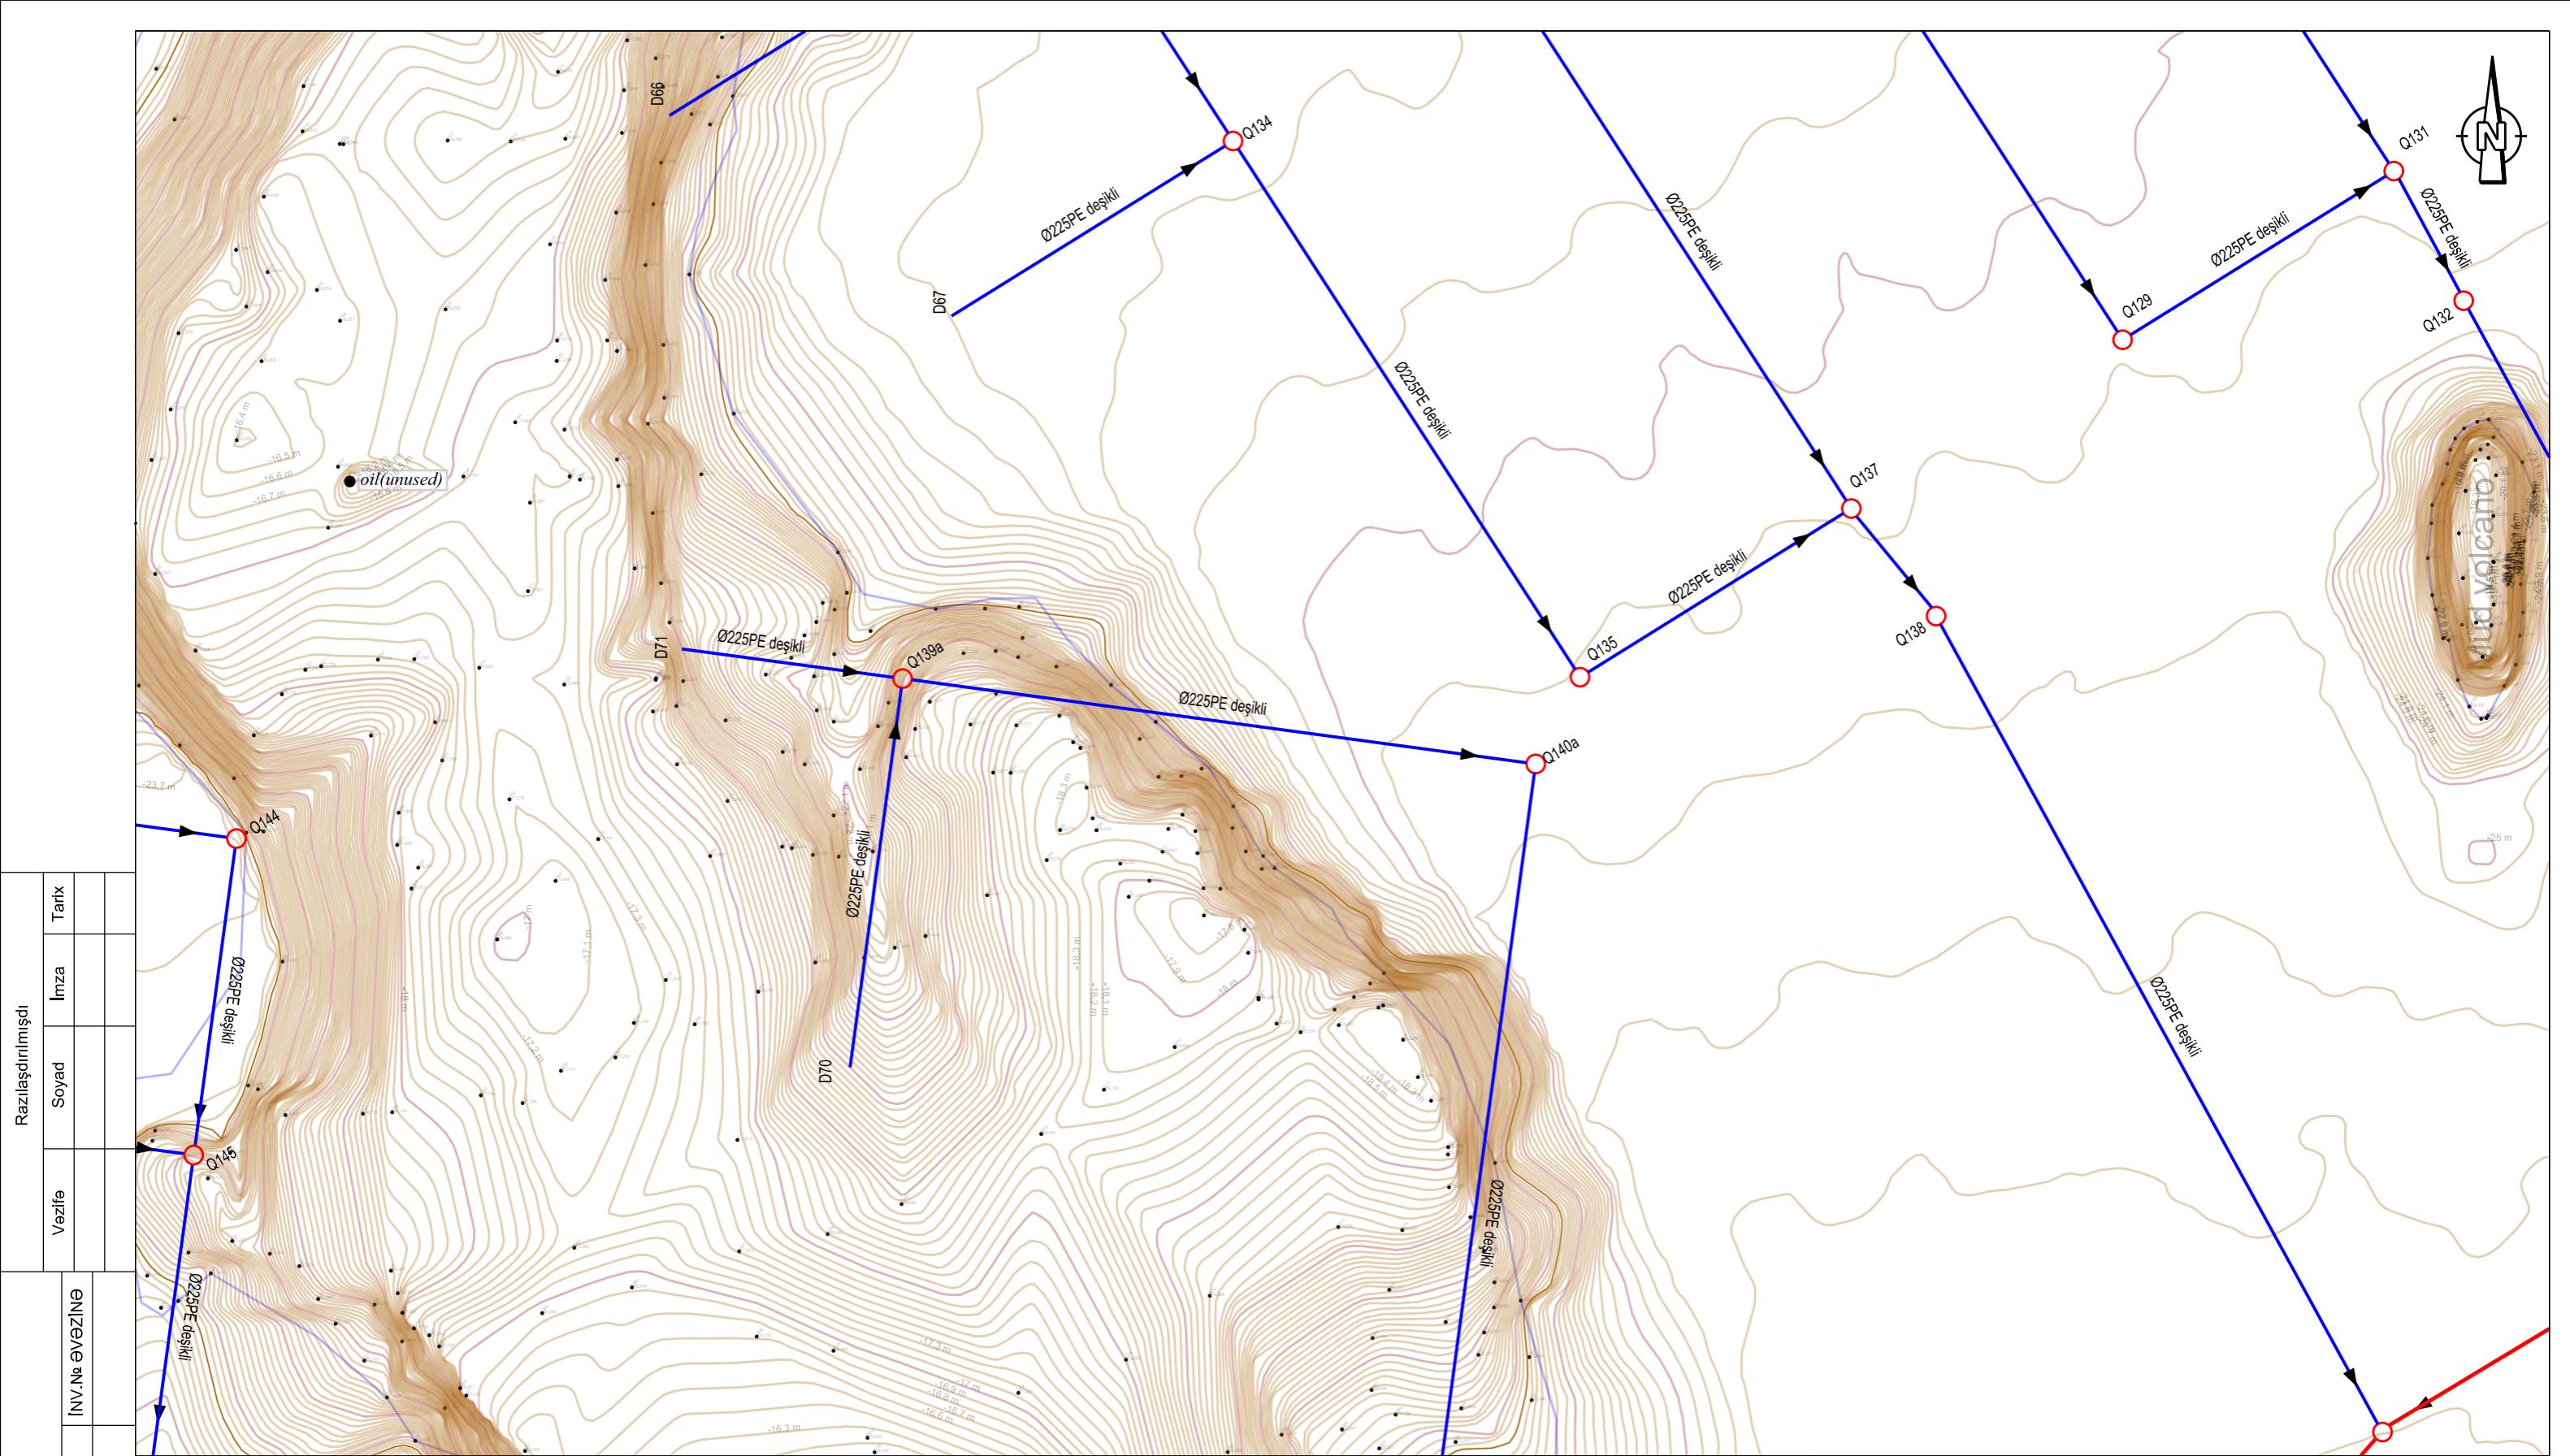


Razlılaşdırılmış

Vəzifə	Soyad	İmza	Tarix
--------	-------	------	-------

INVENTAR №	IMZA VƏ TARIX	INV. № ƏVƏZİNƏ
------------	---------------	----------------

Cizgilərin birləşmə sxemi

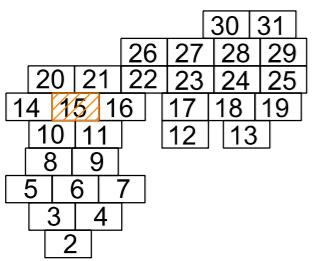

Şerti işarələr



Ø225 HDPE



Ø315 HDPE



Baxış quyusu

2021/AT-04-DS-9.2.1


Suraxanı rayonunun inzibati ərazisində Zığ gölünün ətrafında
yerləşən ərazilərdə yeni yaşlılıqların salınması və damcılı suvarma
sisteminin qurulması

Dəyiş.	Dəy.s	Vərəq	Sən.Nö	İmza	Tarix
LBM	T.Ağayev				
İşlədi	N.Məmmədov				
Yoxladı	A. Aliyev				
Normanəz.	Y. Sitnikova				

Drenaj sistemi

mərhələ	vərəq	vərəqlər
İL	15	84


Drenaj sistemi planı(davamı)

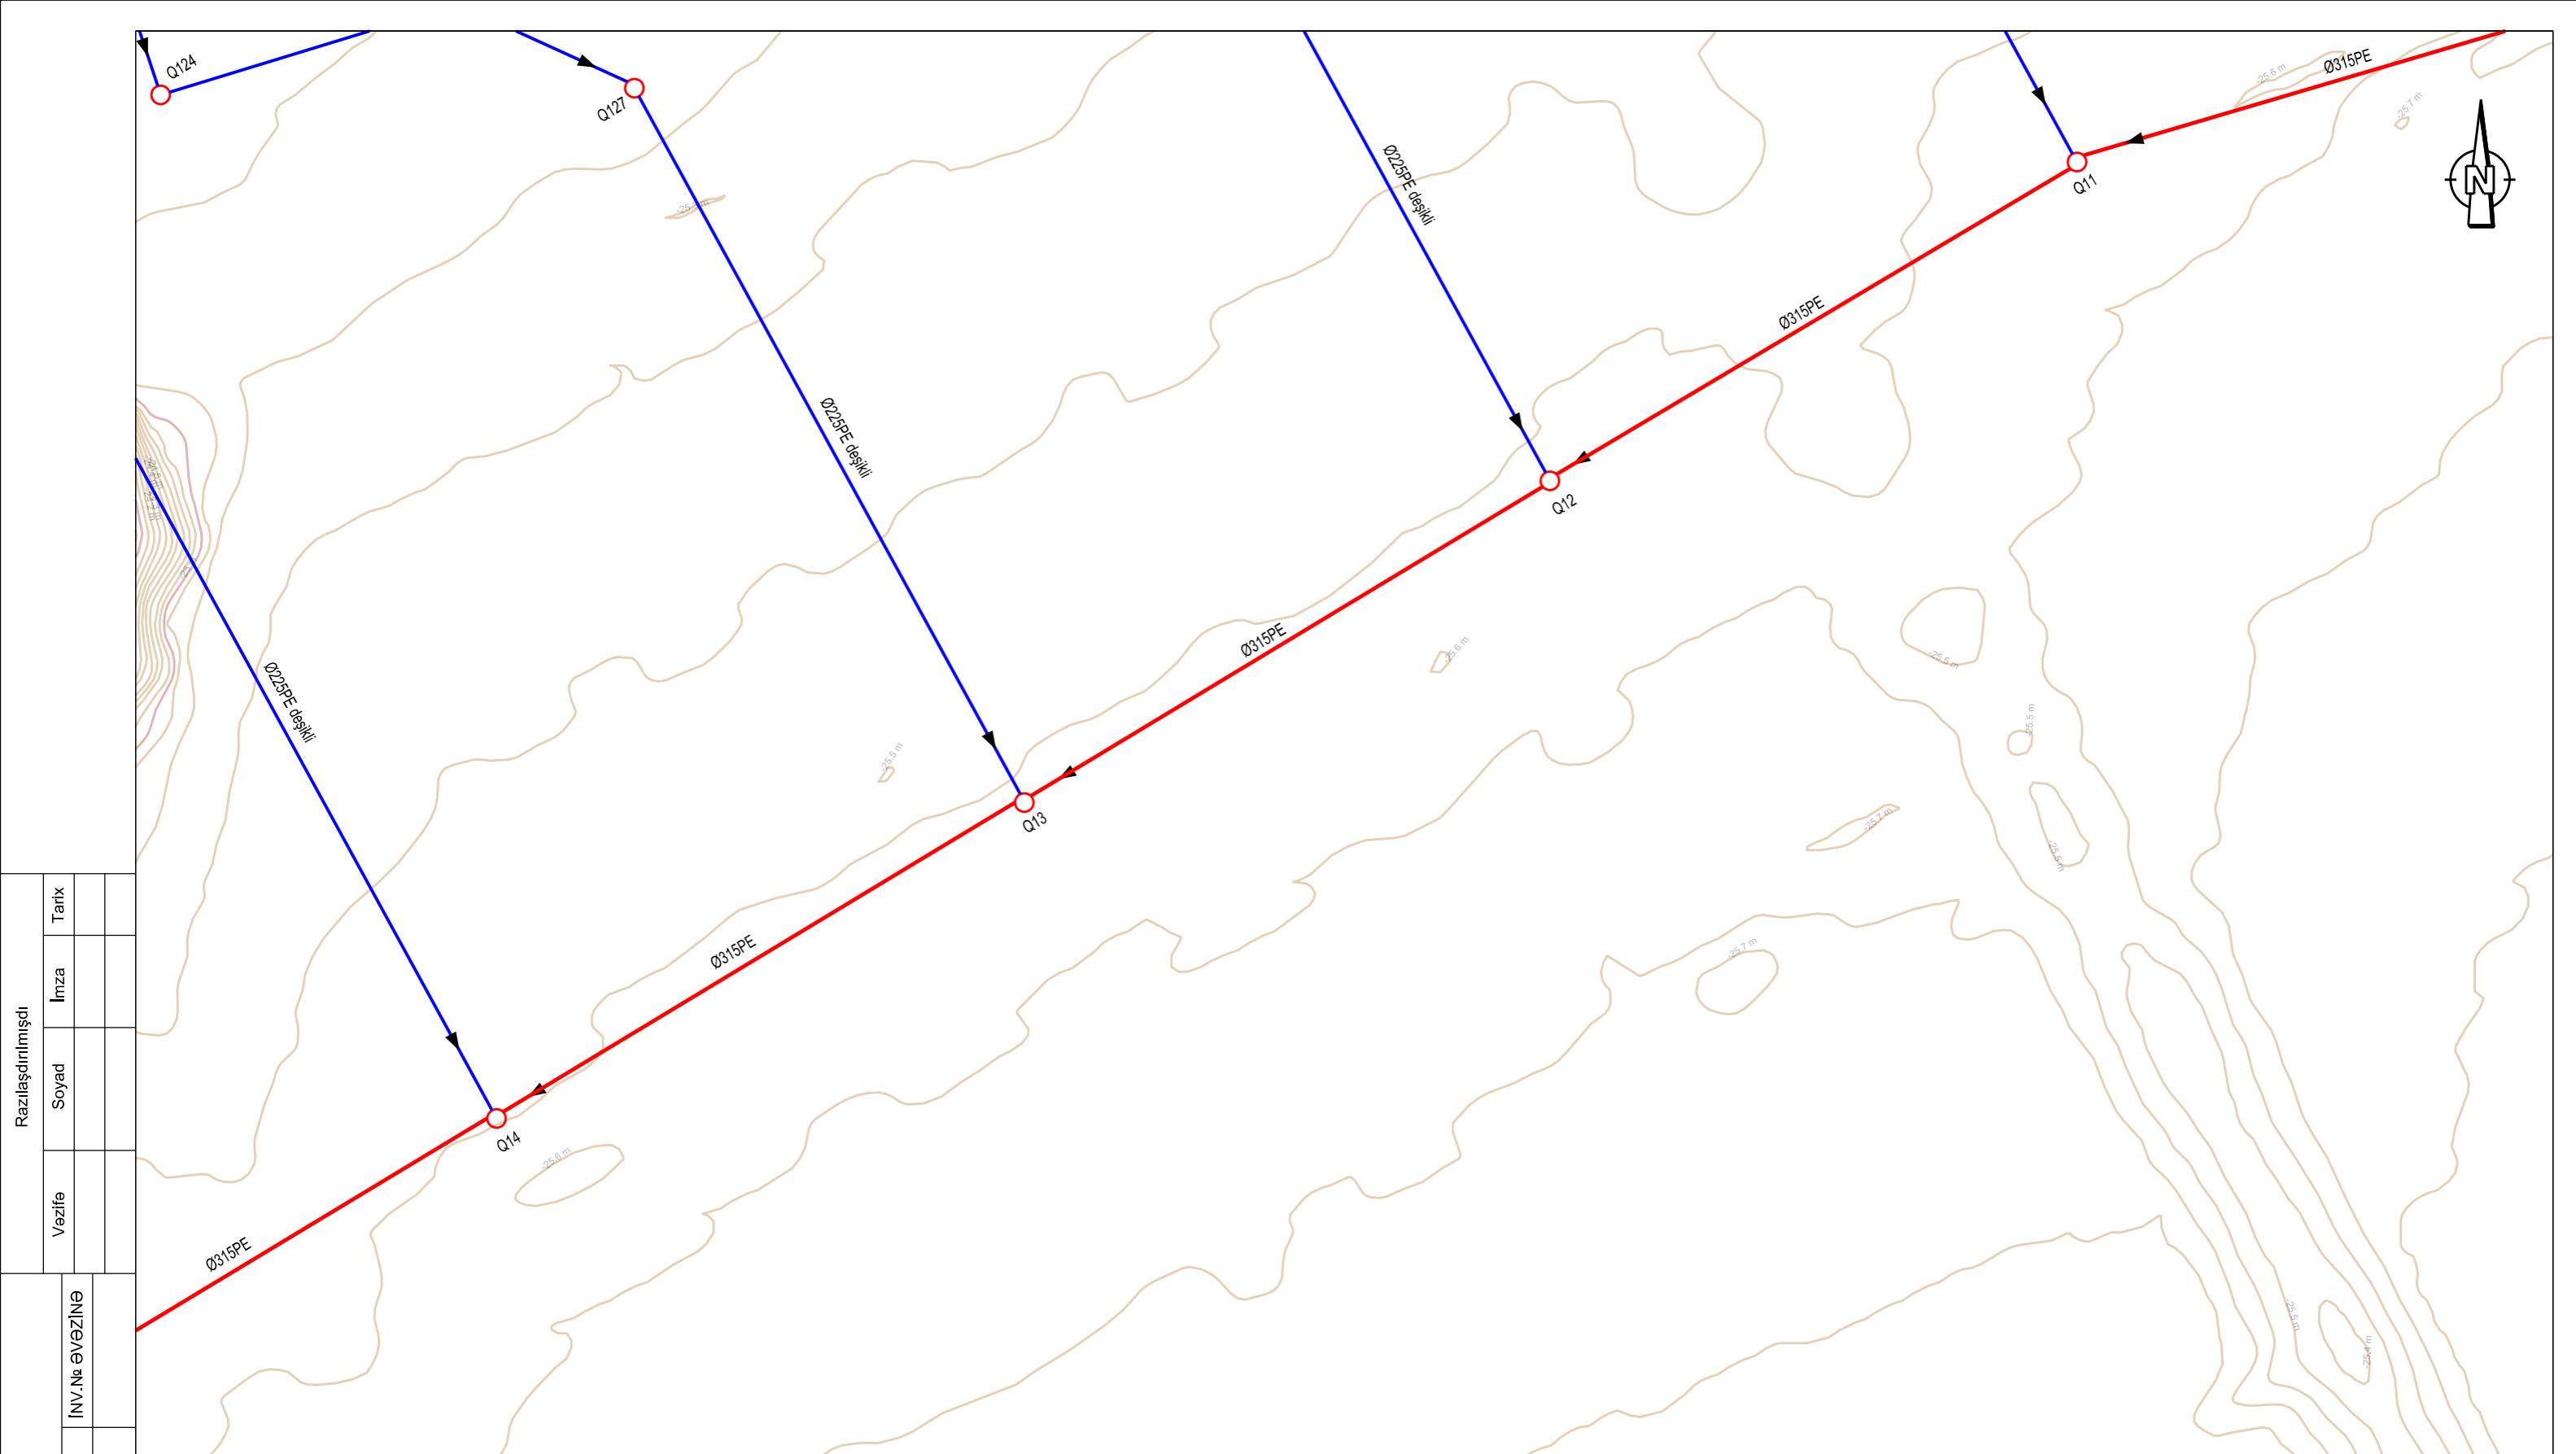

Razlaşdırılmışlı					
Vəzifə	Soyad	İmza	Tarix		

INVENTAR №	IMZA VƏ TARIX	INV.NƏ İMZƏZİNƏ

Cizgilərin birləşmə sxemi

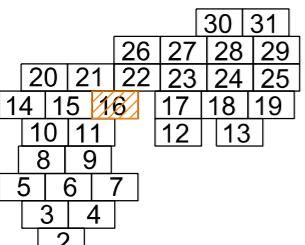

Şerti işarələr



Ø225 HDPE



Ø315 HDPE



Baxış quyusu

2021/AT-04-DS-9.2.1

Suraxanı rayonunun inzibati ərazisində Zığ gölünün ətrafında
yerləşən ərazilərdə yeni yaşilliqlərin salınması və damcılı suvarma
sisteminin qurulması

Dəyiş.	Dəy.s	Vərəq	Sən.Nö	İmza	Tarix
LBM	T.Ağayev				
İşlədi	N.Məmmədov				
Yoxladı	A. Aliyev				
Normanəz.	Y. Sitnikova				


Drenaj sistemi

mərhələ vərəq vərəqlər

İL 16 84


Drenaj sistemi planı(davamı)

EIB HYDROTRANS ENGINEERING

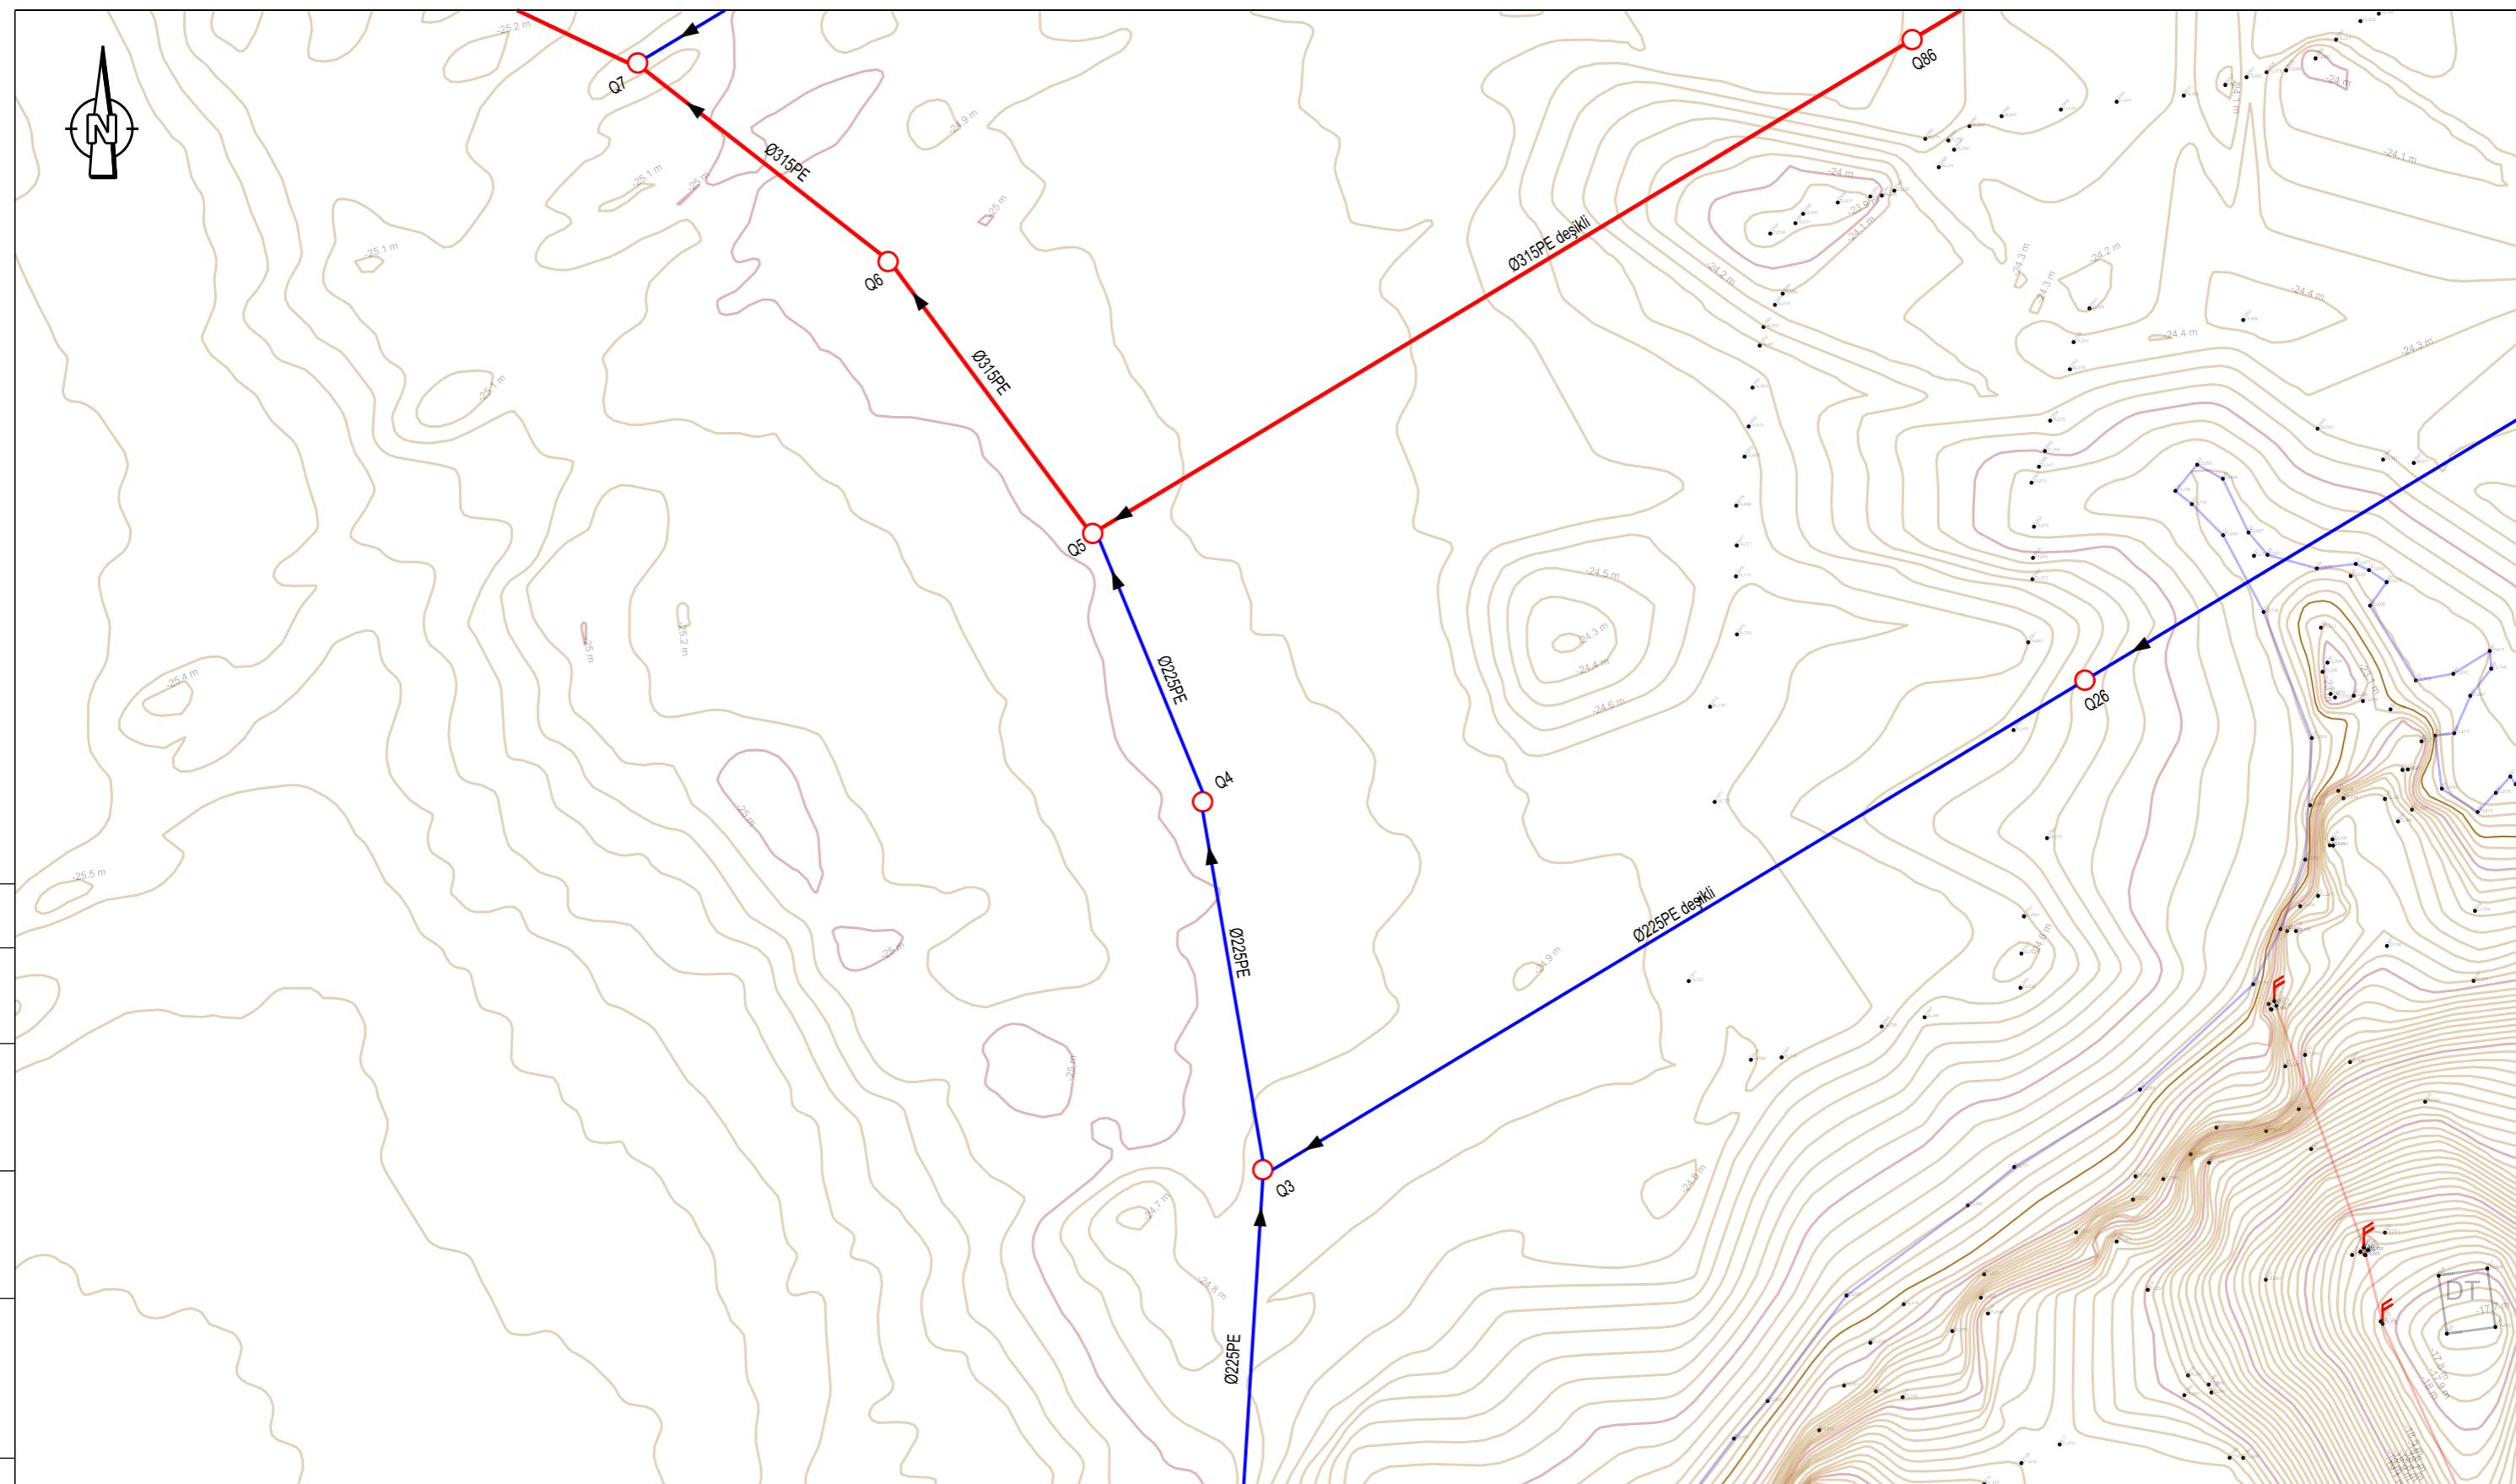

Razlaşdırılmış						
INVENTAR №	MZA VƏ TARİX	MV.Nö ƏVƏZİNƏ	Vəzifə			
				Soyad	İmza	Tarix

Cizgilərin birləşmə sxemi

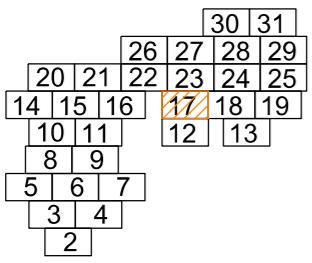

Şərti işarələr

Ø225 HDPE

Ø315 HDPE

Baxış quyusu



2021/AT-04-DS-9.2.1


**Suraxanı rayonunun inzibati ərazisində Zığ gölünün ətrafında
yerləşən ərazilərdə yeni yaşlılıqların salınması və damcılı suvarma
sisteminin qurulması**

Dəyiş.	Dəy.s	Vərəq	Sən.Nö	İmza
LBM	T.Ağayev			
İşlədi	N.Məmmədov			
Yoxladı	A. Aliyev			
Normanəz.	Y. Sıtnikova			

Drenaj sistemi


enai sistemi planı(davamlı)

 HYDROTRANS ENGINEERING
ENGINEERING CENTER FOR DESIGN OF WATER AND TRANSPORT INFRASTRUCTURE
SUO KUOLIVET INFRASTRUKTURILAINEN LAIHESIJÖNÖHÖ MÖÖÜ ÜPGÖ MIIHONÖÖ ÜMIIHÖ

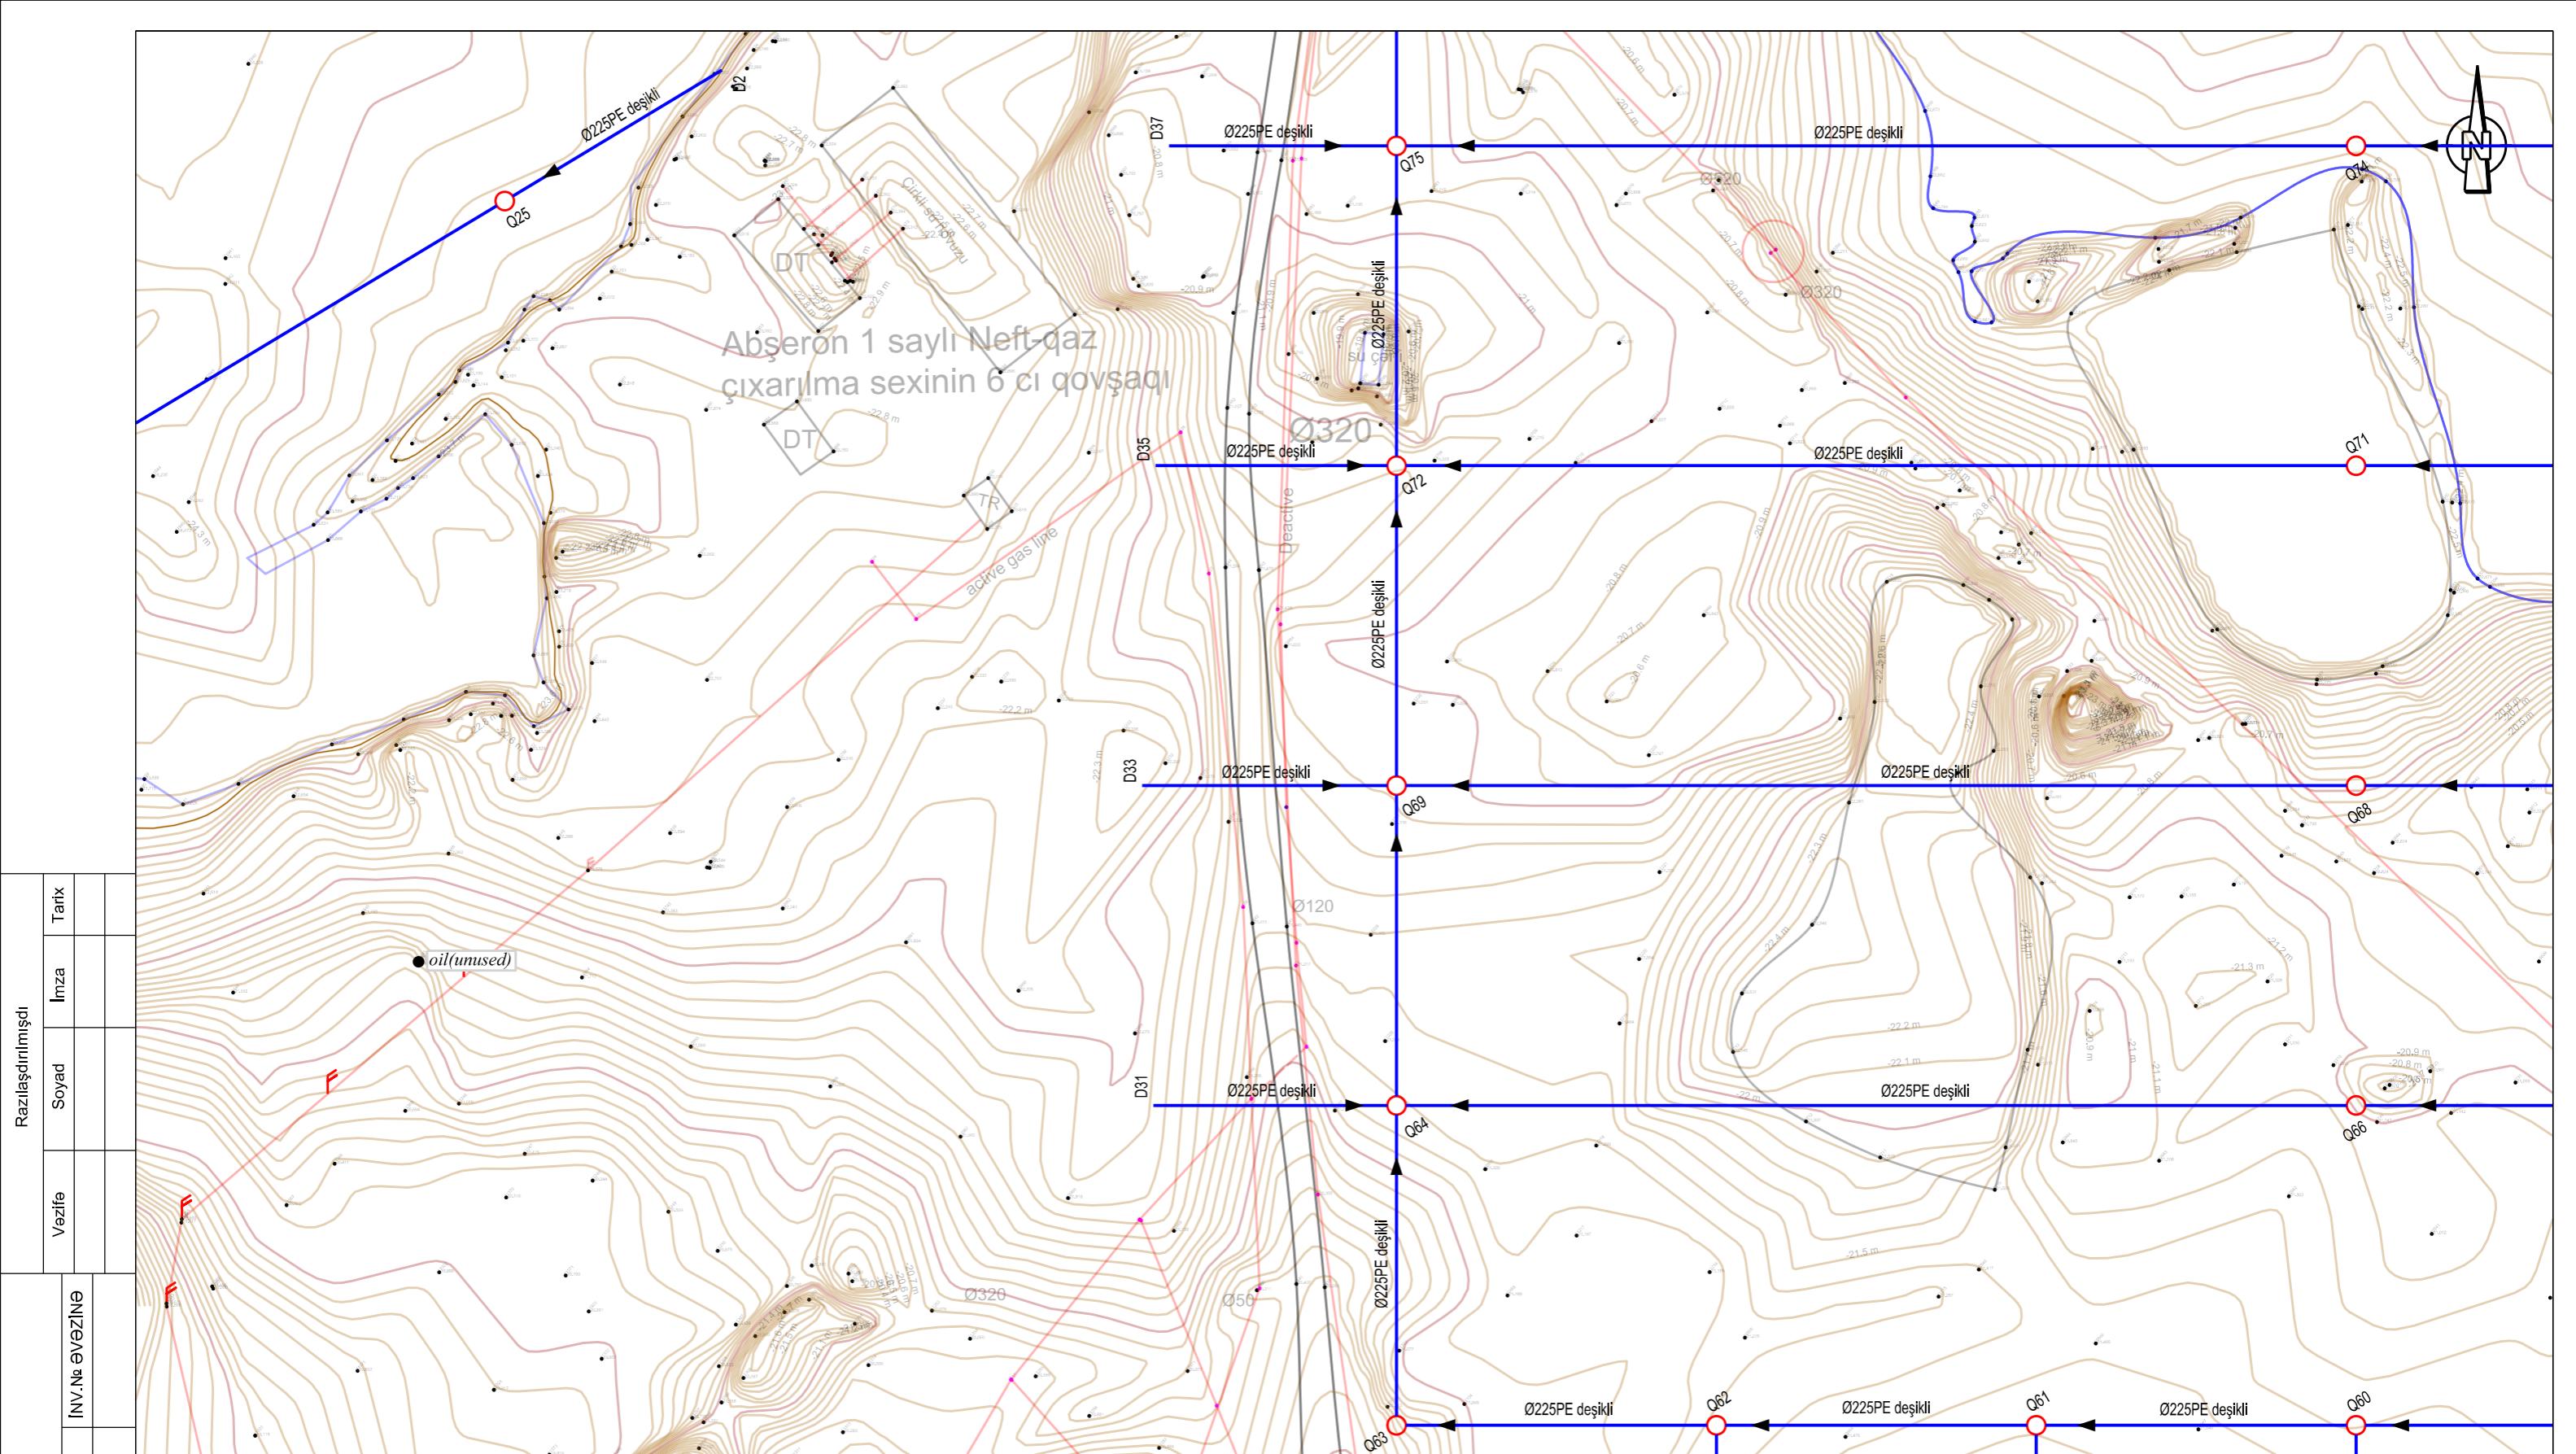

INVENTAR №	IMZA VƏ TARİX	INV.NƏ İVƏZİNƏ	Razlaşdırılmışdı
Vəzifə	Soyad	İmza	Tarix

Cizgilərin birləşmə sxemi

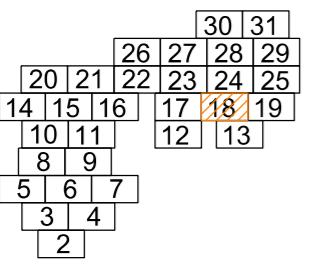

Şerti işarələr



Ø225 HDPE



Ø315 HDPE



Baxış quyusu

2021/AT-04-DS-9.2.1

Suraxanı rayonunun inzibati ərazisində Zığ gölünün ətrafında
yerləşən ərazilərdə yeni yaşlılıqların salınması və damcılı suvarma
sisteminin qurulması

Dəyiş.	Dəy.s	Vərəq	Sən.Nö	İmza	Tarix
LBM	T.Ağayev				
İşlədi	N.Məmmədov				
Yoxladı	A. Aliyev				
Normanəz.	Y. Sitnikova				

Drenaj sistemi

mərhələ vərəq vərəqlər

İL 18 84


Drenaj sistemi planı(davamı)

EIB HYDROTRANS ENGINEERING

ENGINEERING CENTER FOR DESIGN OF WATER AND TRANSPORT INFRASTRUCTURE


SU NAŞİYƏT İNFRASTRÜKTURUNUN LƏTİFLƏNDİRİLMƏSI İZƏT MƏHMONLUVU NƏTİCƏSİ

Format A3

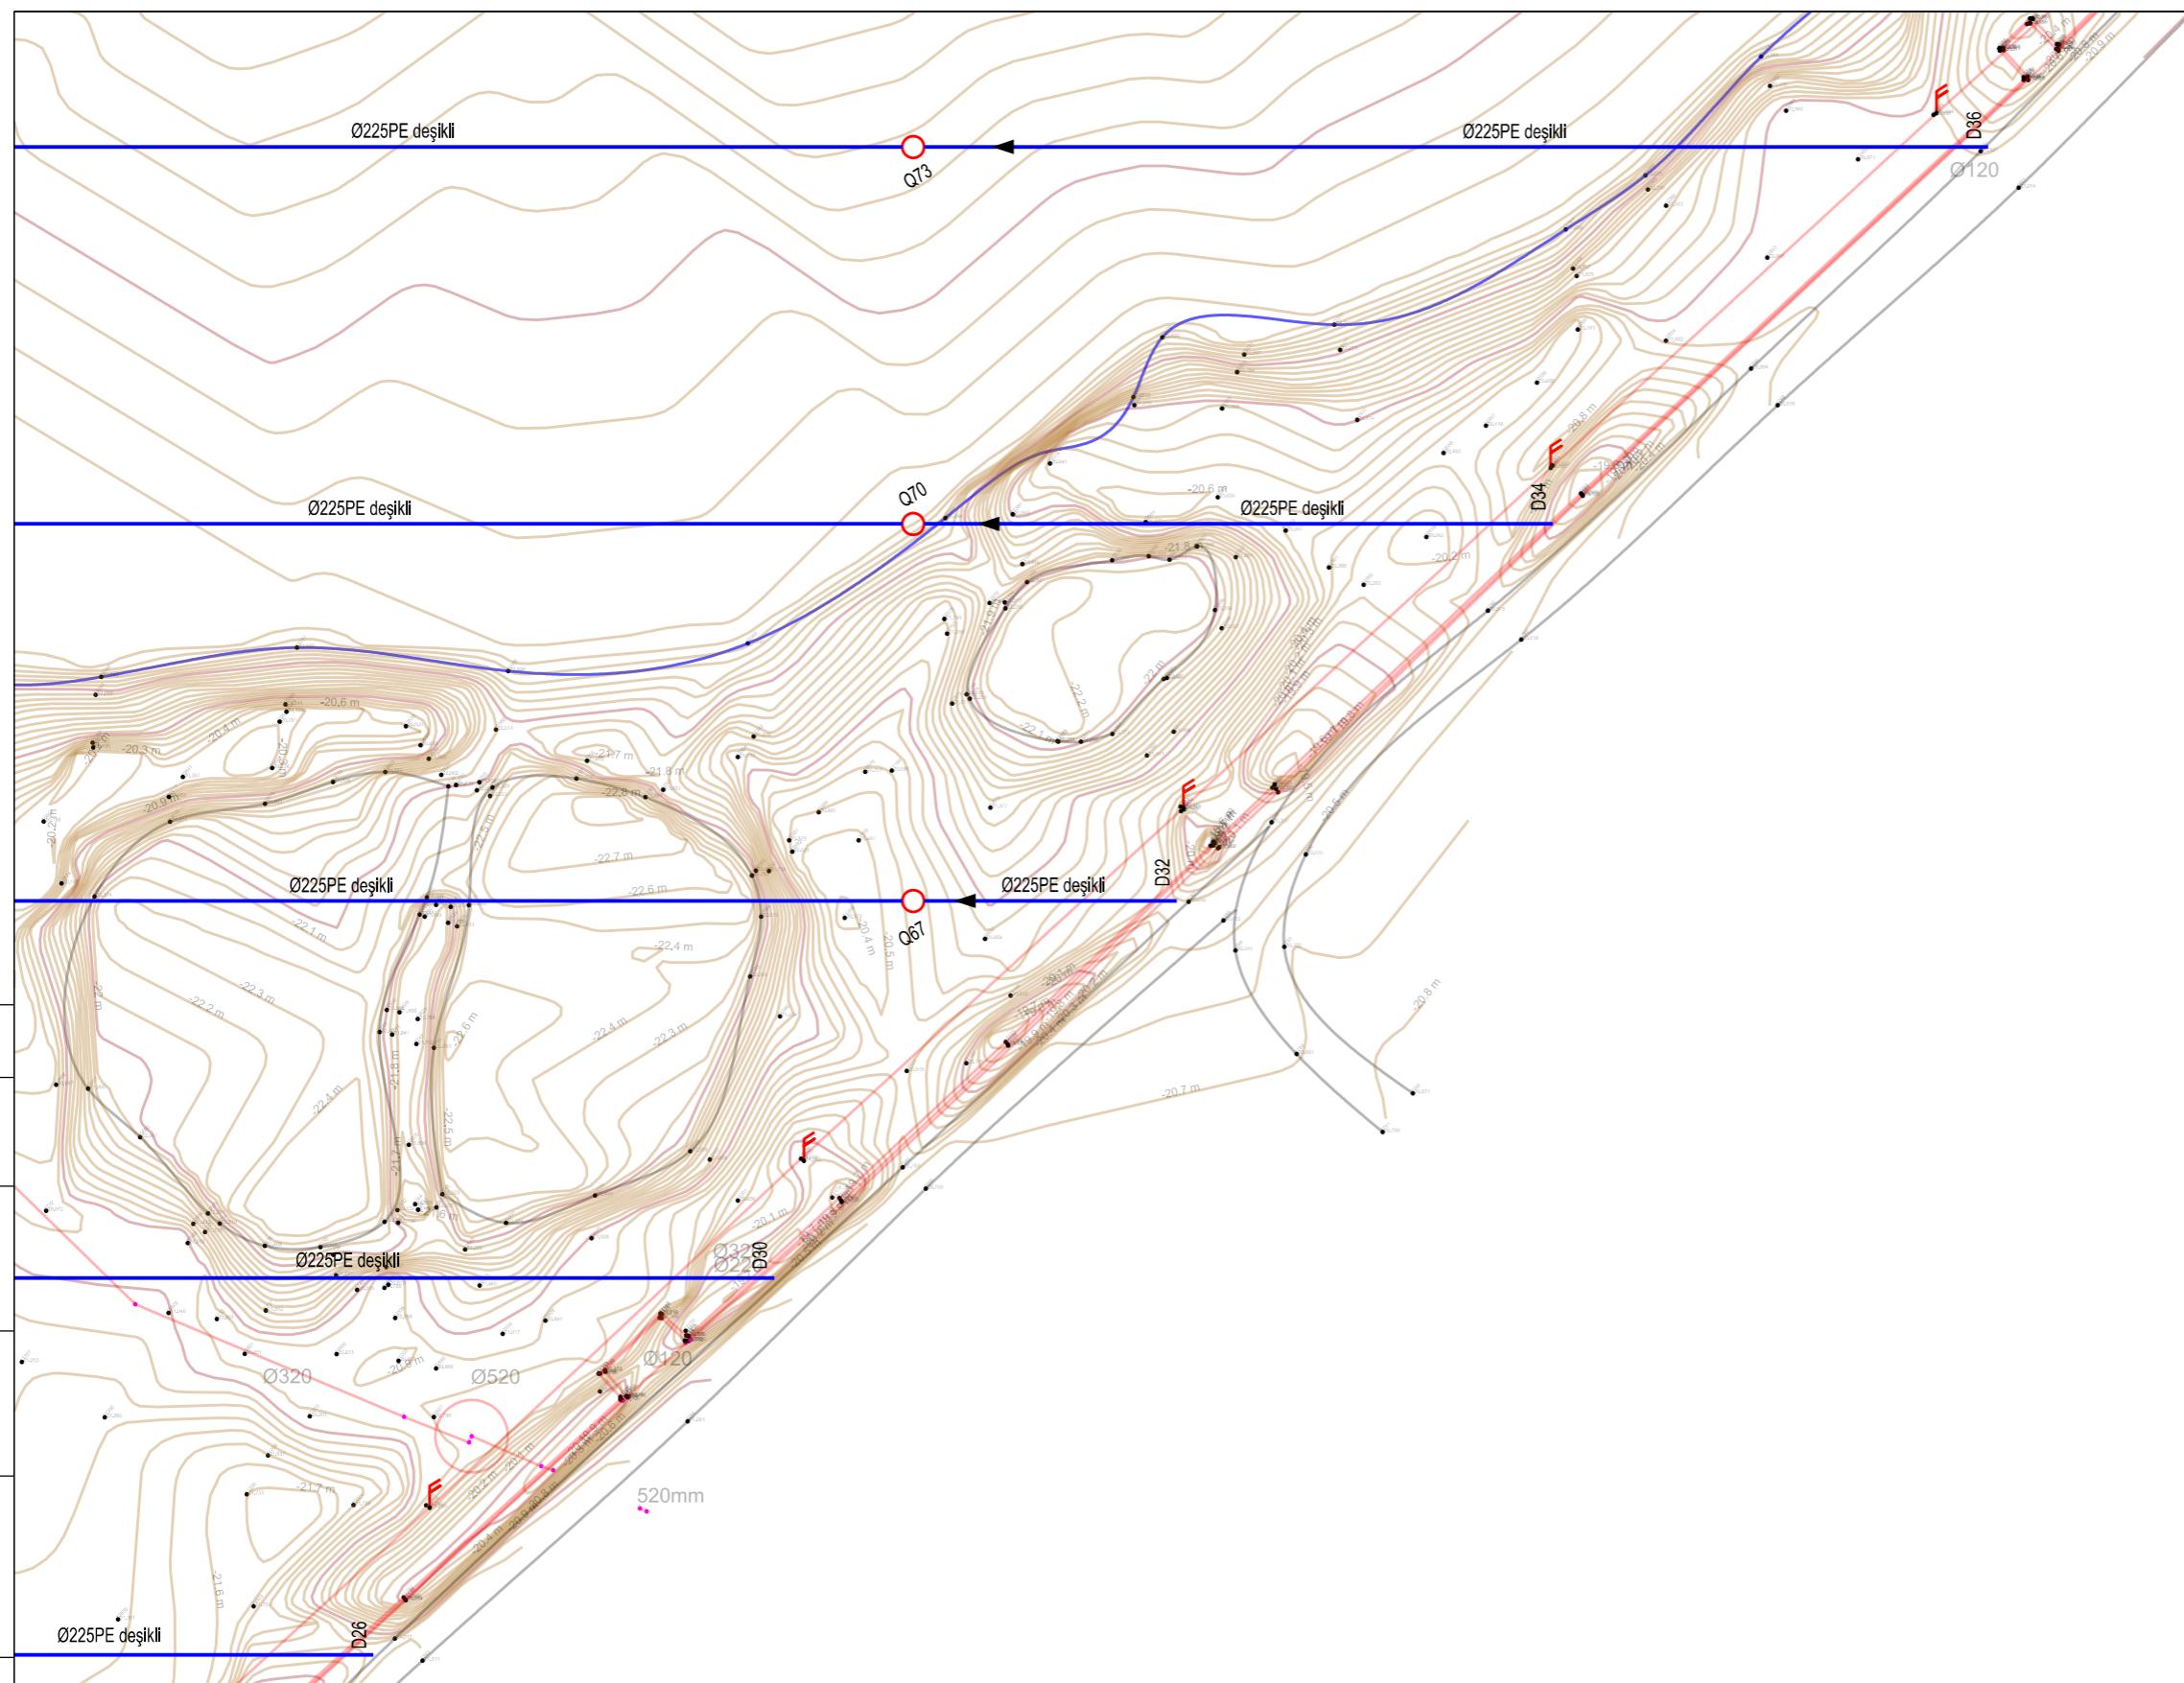

Razılışdırılmışdı			
INVENTAR №	İMZА VE TARİХ	İNV.№ ƏVƏZİNƏ	Vəzifə
			Soyad
			İmza
			Tarix

Cizgilərin birləşmə sxemi

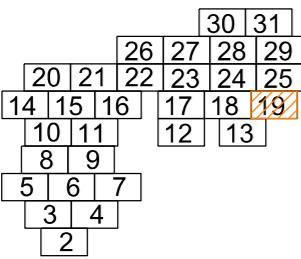

Şərti işarələ

Ø225 HDP

Ø315 HDP

Baxış quyu



2021/AT-04-DS-9.2.1


Tarix Suraxanı rayonunun inzibati ərazisində Zığ gölünün ətrafında yerləşən ərazilrdə yeni yaşlılıqların salınması və damcılı suvarma sisteminin qurulması

Dəyiş.	Dəy.s	Vərəq	Sən.Nö	İmza
LBM	T.Ağayev			
İşlədi	N.Məmmədov			
Yoxladı	A. Aliyev			
Normanəz.	Y. Sitnikova			

Drenaj sistemi


enaj sistemi planı(davamı)

 HYDROTRANS ENGINEERING
ENGINEERING CENTER FOR DESIGN OF WATER AND TRANSPORT INFRASTRUCTURE

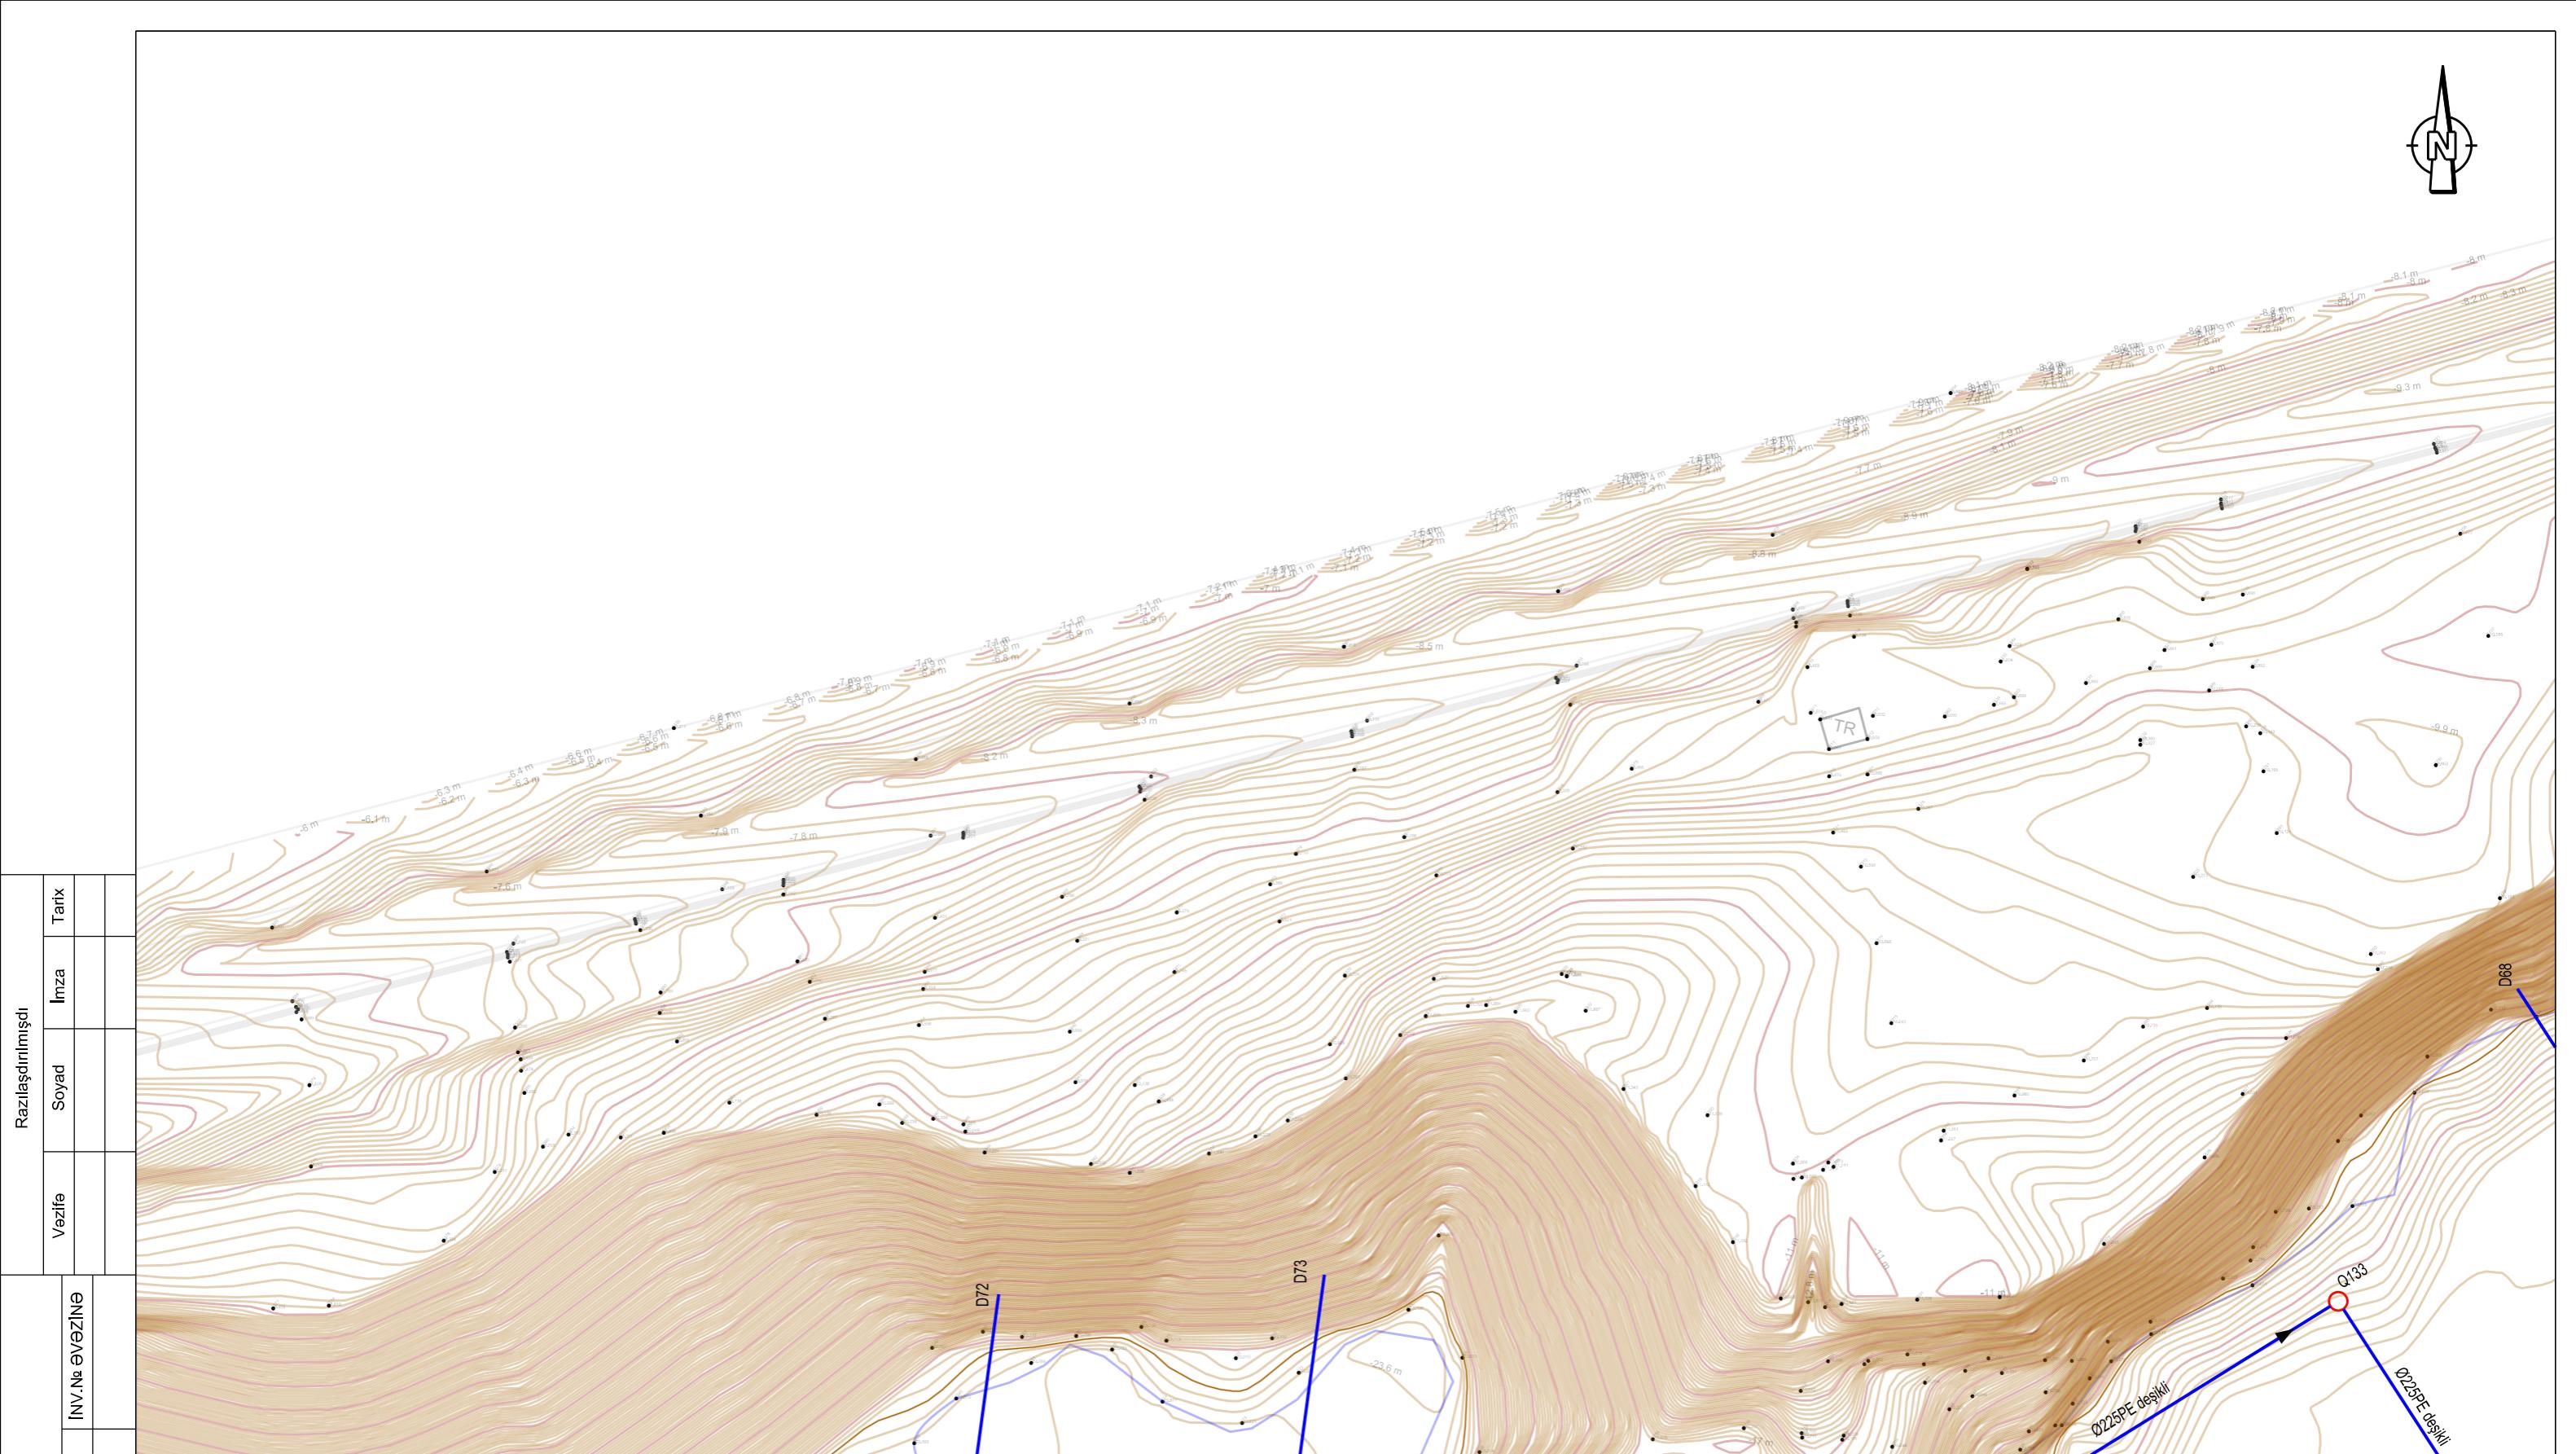

Razlaşdırılmışdı							
Razlaşdırılmışdı							
INVENTAR №		İMZA VƏ TARİX	INV.Nº ΘΕΩΖΗΝΘ	Vəzifə	Soyad	İmza	Tarix

Cizgilərin birləşmə sxemi

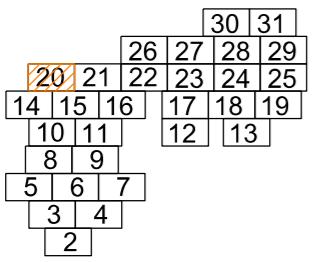

Şərti işarələr

Ø225 HDPE

Ø315 HDPE

Baxış quyusu



						2021/AT-04-DS-9.2.1		
						Suraxanı rayonunun inzibati ərazisində Zığ gölünün ətrafında yerləşən ərazilərdə yeni yaşıllıqların salınması və damcılı suvarma sisteminin qurulması		
Dəyiş.	Dəy.s	Vərəq	Sən.Nö	İmza	Tarix			
LBM	T.Ağayev					mərhələ	vərəq	vərəqlər
İşlədi	N.Məmmədov					İL	20	84
Yoxladı	A. Aliyev							
Normanəz.	Y. Sitnikova					Drenaj sistemi planı(davamı)		
						 HYDROTRANS ENGINEERING ENGINEERING CENTER FOR DESIGN OF WATER AND TRANSPORT INFRASTRUCTURE SEYİD RƏQİBŞEHİB İBREHİMŞƏHİB FİZİ MİNƏHƏNİB NƏŞRİ		


2021/AT-04-DS-9.2.1

Tarix Suraxanı rayonunun inzibati ərazisində Zığ gölünün ətrafında yerləşən ərazilərdə yeni yaşlılıqların salınması və damcılı suvarma sisteminin qurulması


Drenaj sistemi

HYDROTRANS ENGINEERING
ENGINEERING CENTER FOR DESIGN OF WATER AND TRANSPORT INFRASTRUCTURE
SU VE NOVUİYAT İNFRASTRÜKTÜRÜSUNU LAYHİĞİNDİRİLMESİ (ÖZGÜ MÜHENDİSLİK MERKEZİ)

Format A3

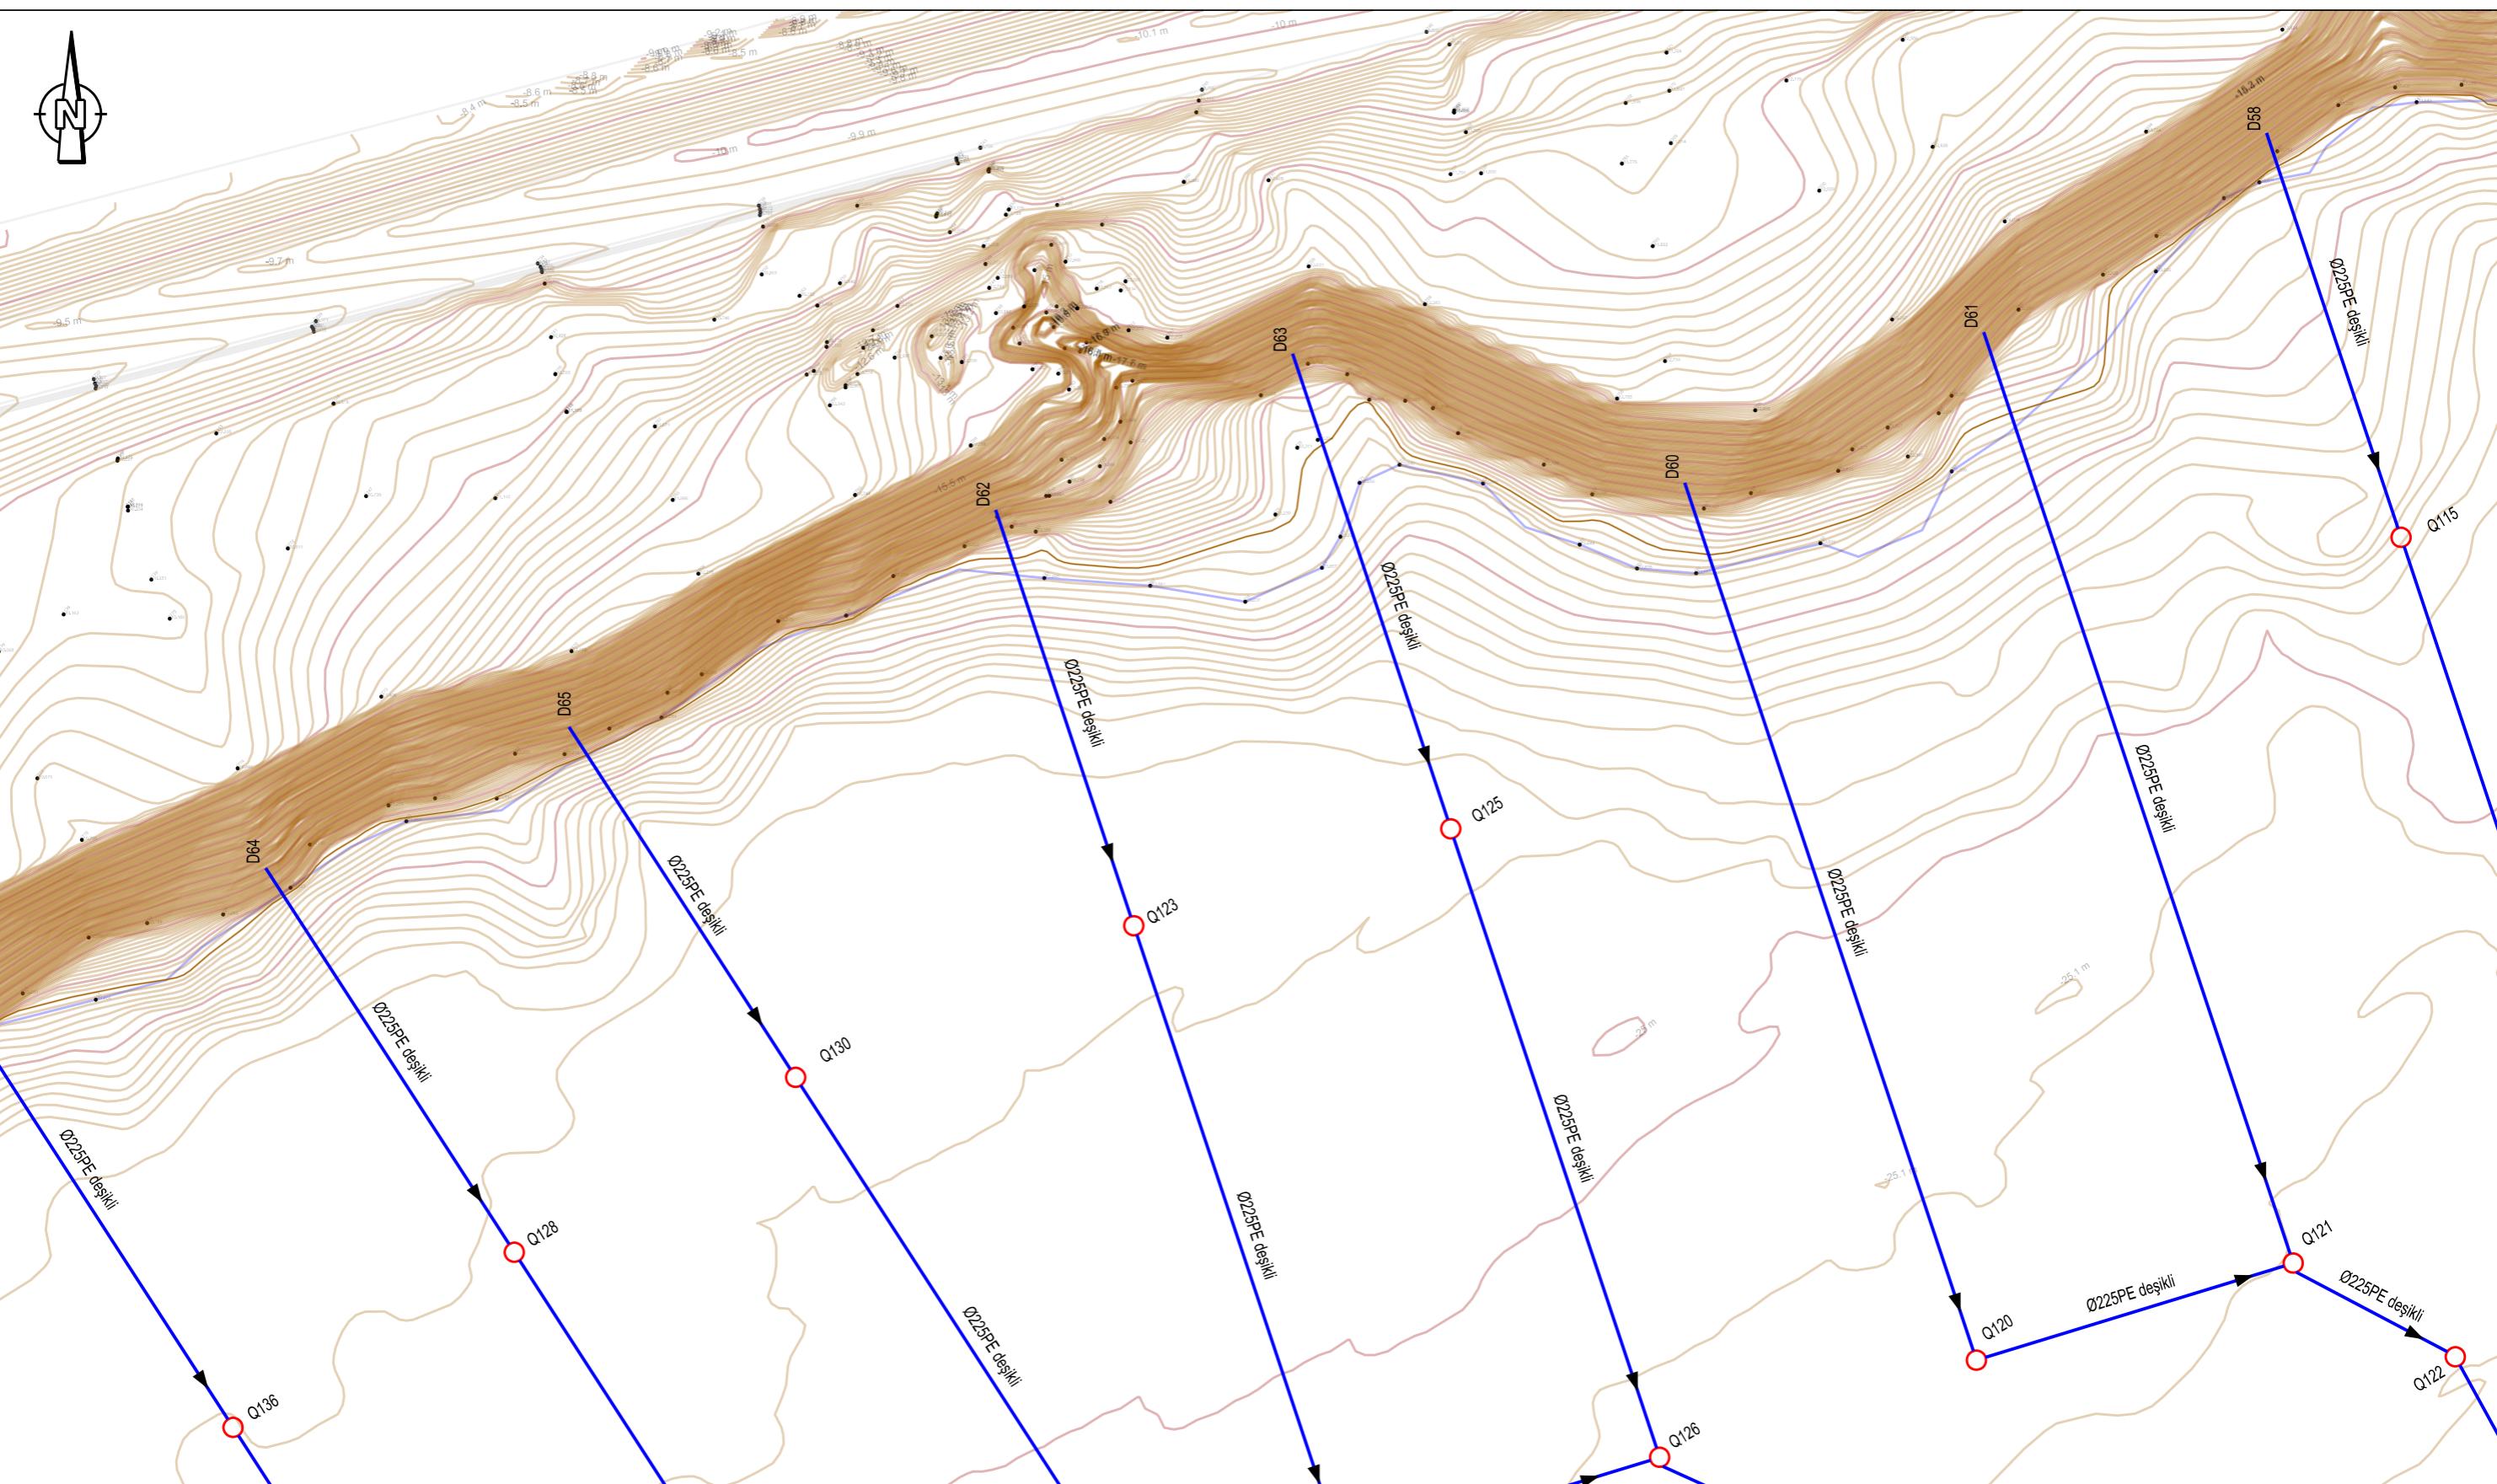

Cizgilərin birləşmə sxemi

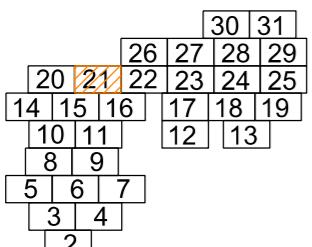

Şərti işarələr

Ø225 HDPE

Ø315 HDPE

Baxış quyusu

— 1 —

[View Details](#)

○

2021/AT-04-DS-9.2.1


Tarix Suraxanı rayonunun inzibati ərazisində Zığ gölünün ətrafında yerləşən ərazilərdə yeni yaşlılıqların salınması və damcılı suvarma sisteminin qurulması

Dəyiş.	Dəy.s	Vərəq	Sən.№	İmza
LBM	T.Ağayev			
İşlədi	N.Məmmədov			
Yoxladı	A. Alıyev			
Normanəz.	Y. Sitnikova			

Drenaj sistemi

renaj sistemi planı(davamı)

EIB HYDROTRANS ENGINEERING
ENGINEERING CENTER FOR DESIGN OF WATER AND TRANSPORT INFRASTRUCTURE
SU VE NÜKLİYAT İNFRASTRÜKTÜRLERİNİN LİAHOLİNDİRİLMESİ ÜZÜ MÜHENDİSLİK MERKEZİ

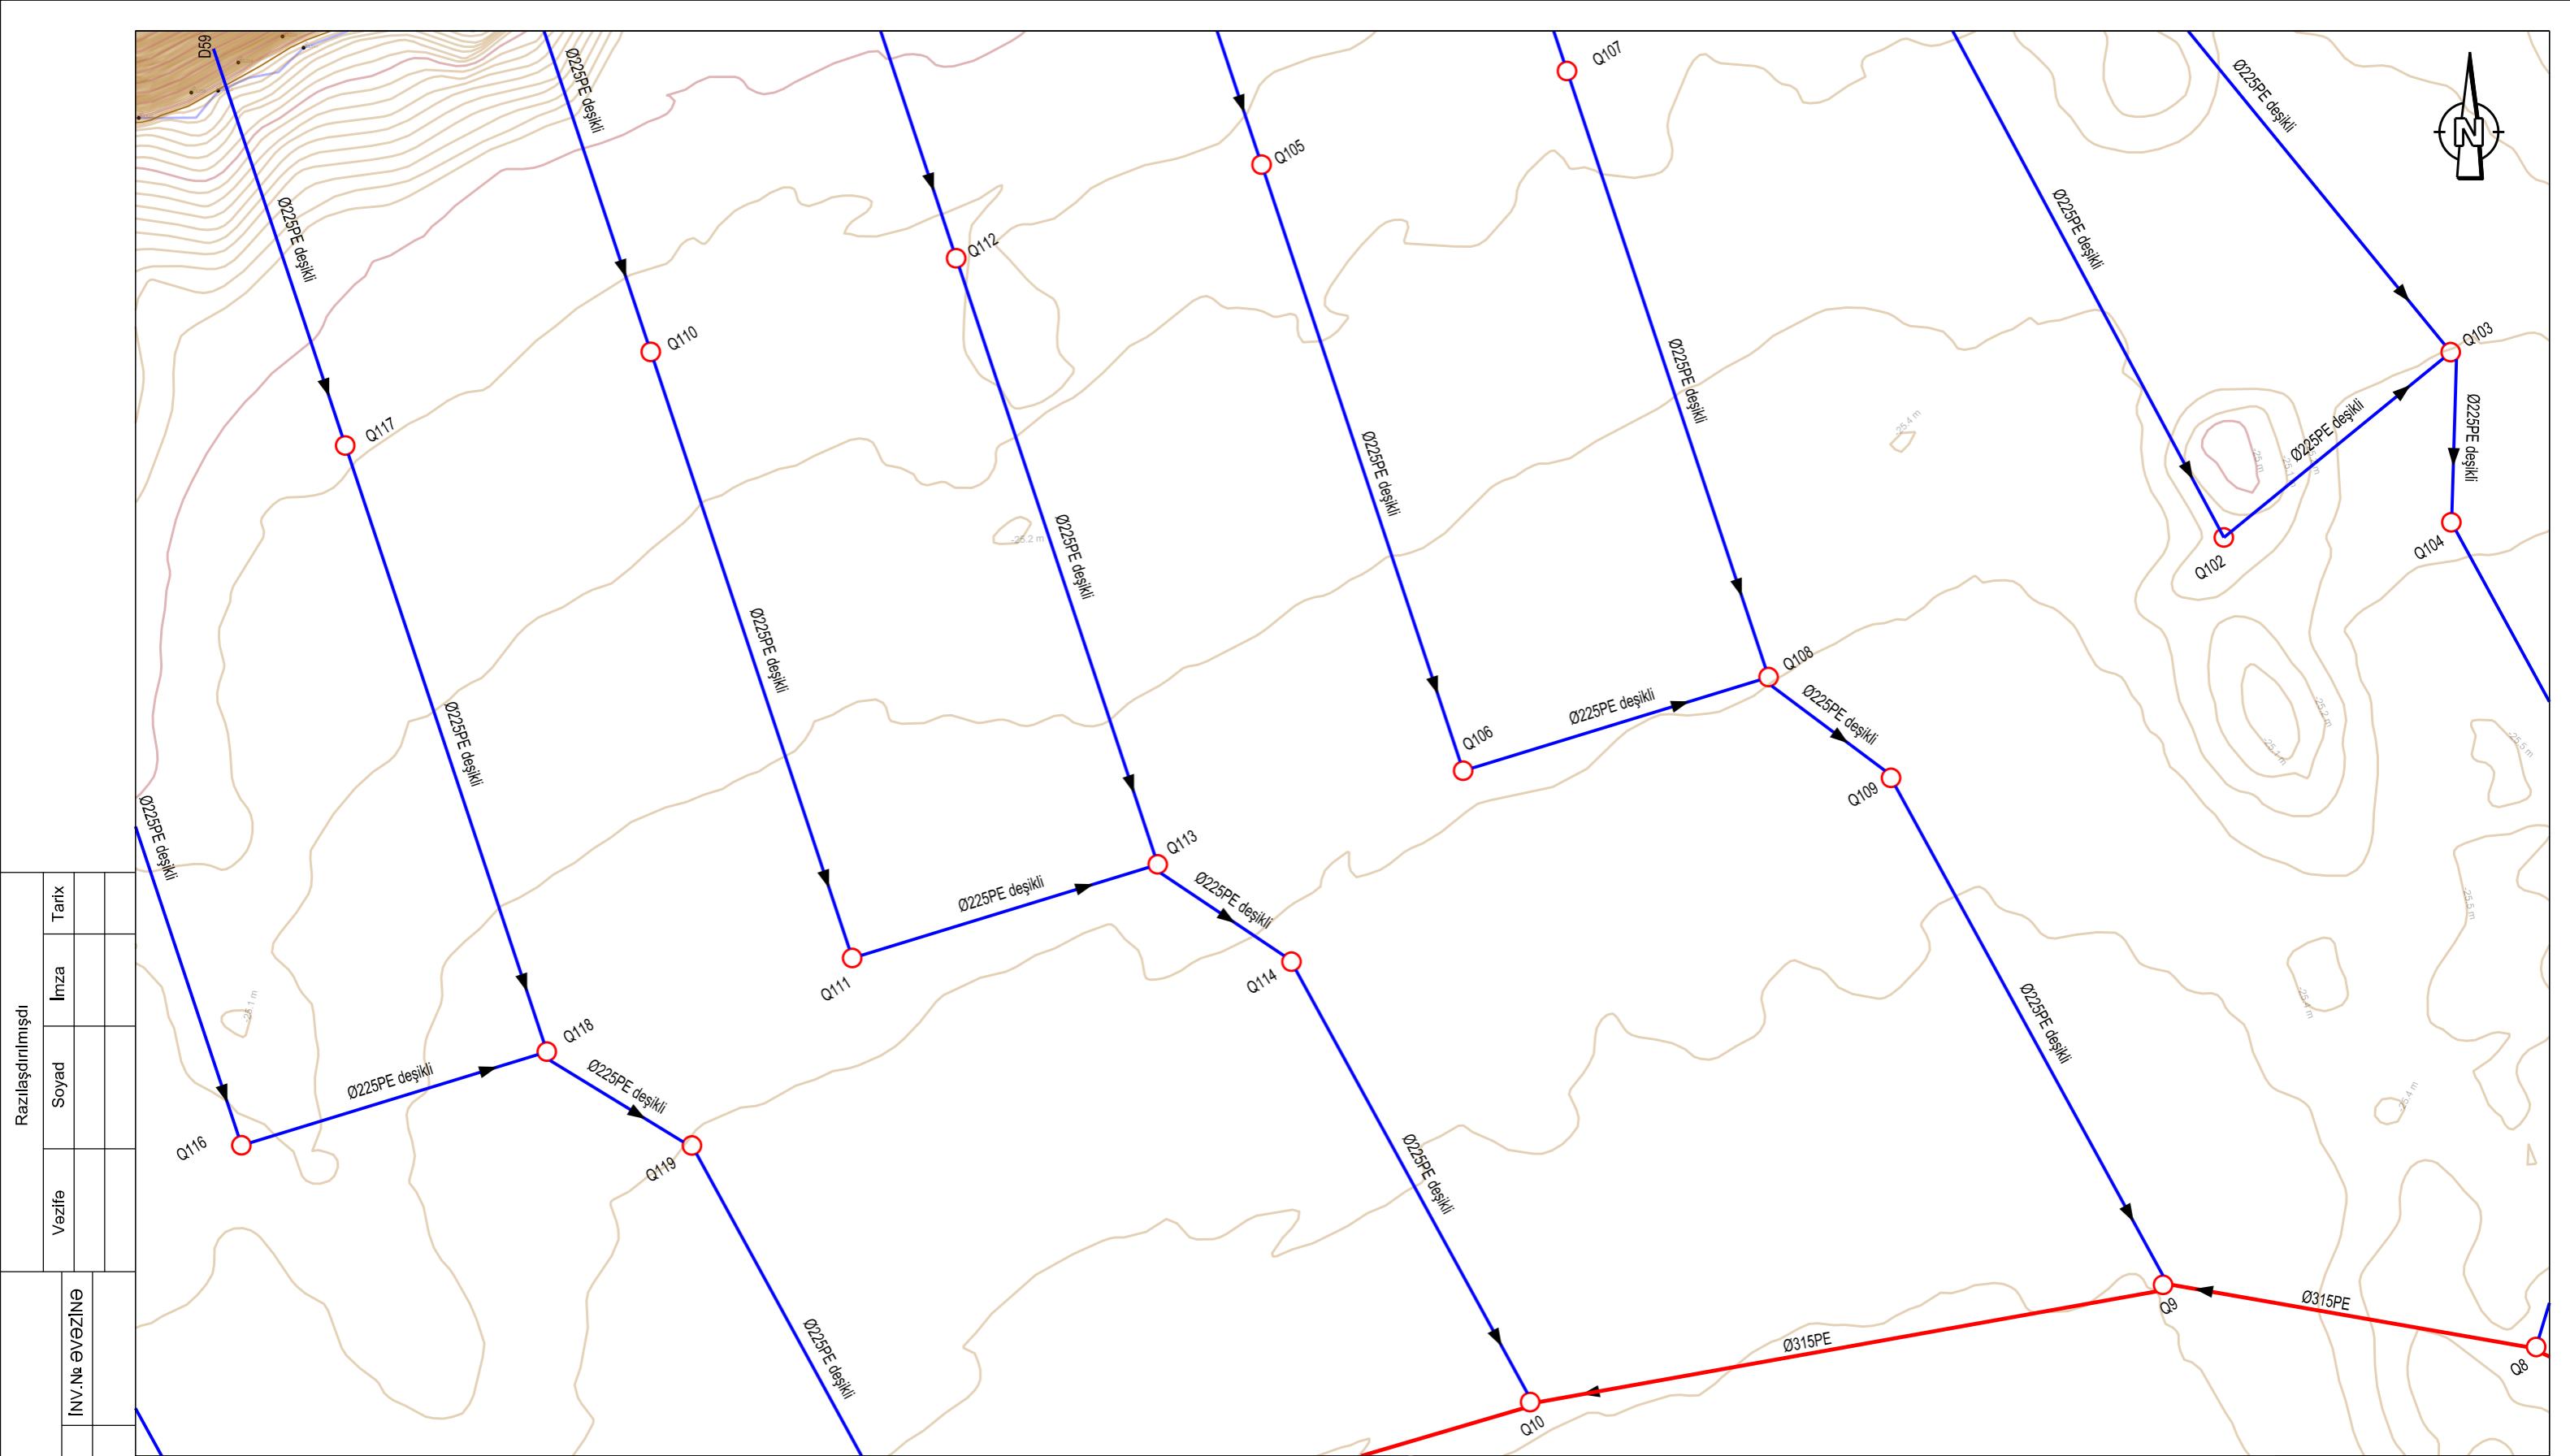


Razlaşdırılmışdı

Vəzifə	Soyad	İmza	Tarix

INV.NƏVƏZİNƏ

INVENTAR №	IMZA VƏ TARIX

Cizgilərin birləşmə sxemi

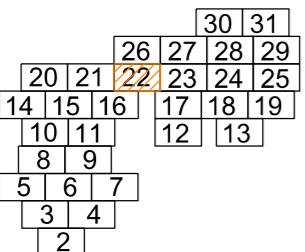

Şerti işarələr



Ø225 HDPE



Ø315 HDPE



Baxış quyusu

2021/AT-04-DS-9.2.1

Suraxanı rayonunun inzibati ərazisində Zığ gölünün ətrafında
yerləşən ərazilərdə yeni yaşlılıqların salınması və damcılı suvarma
sisteminin qurulması

Dəyiş.	Dəy.s	Vərəq	Sən.Nö	İmza	Tarix
LBM	T.Ağayev				
İşlədi	N.Məmmədov				
Yoxladı	A. Aliyev				
Normanəz.	Y. Sitnikova				

Drenaj sistemi

mərhələ vərəq vərəqlər


İL 22 84

Drenaj sistemi planı(davamı)

EIB HYDROTRANS ENGINEERING

ENGINNEERING CENTER FOR DESIGN OF WATER AND TRANSPORT INFRASTRUCTURE

SU NAQIYAH INFRASTRUCTURELƏRİN LƏTİFLƏNDİRİLMƏSI İZBƏ MƏMƏNÜLKÜ HƏMŞİRİ

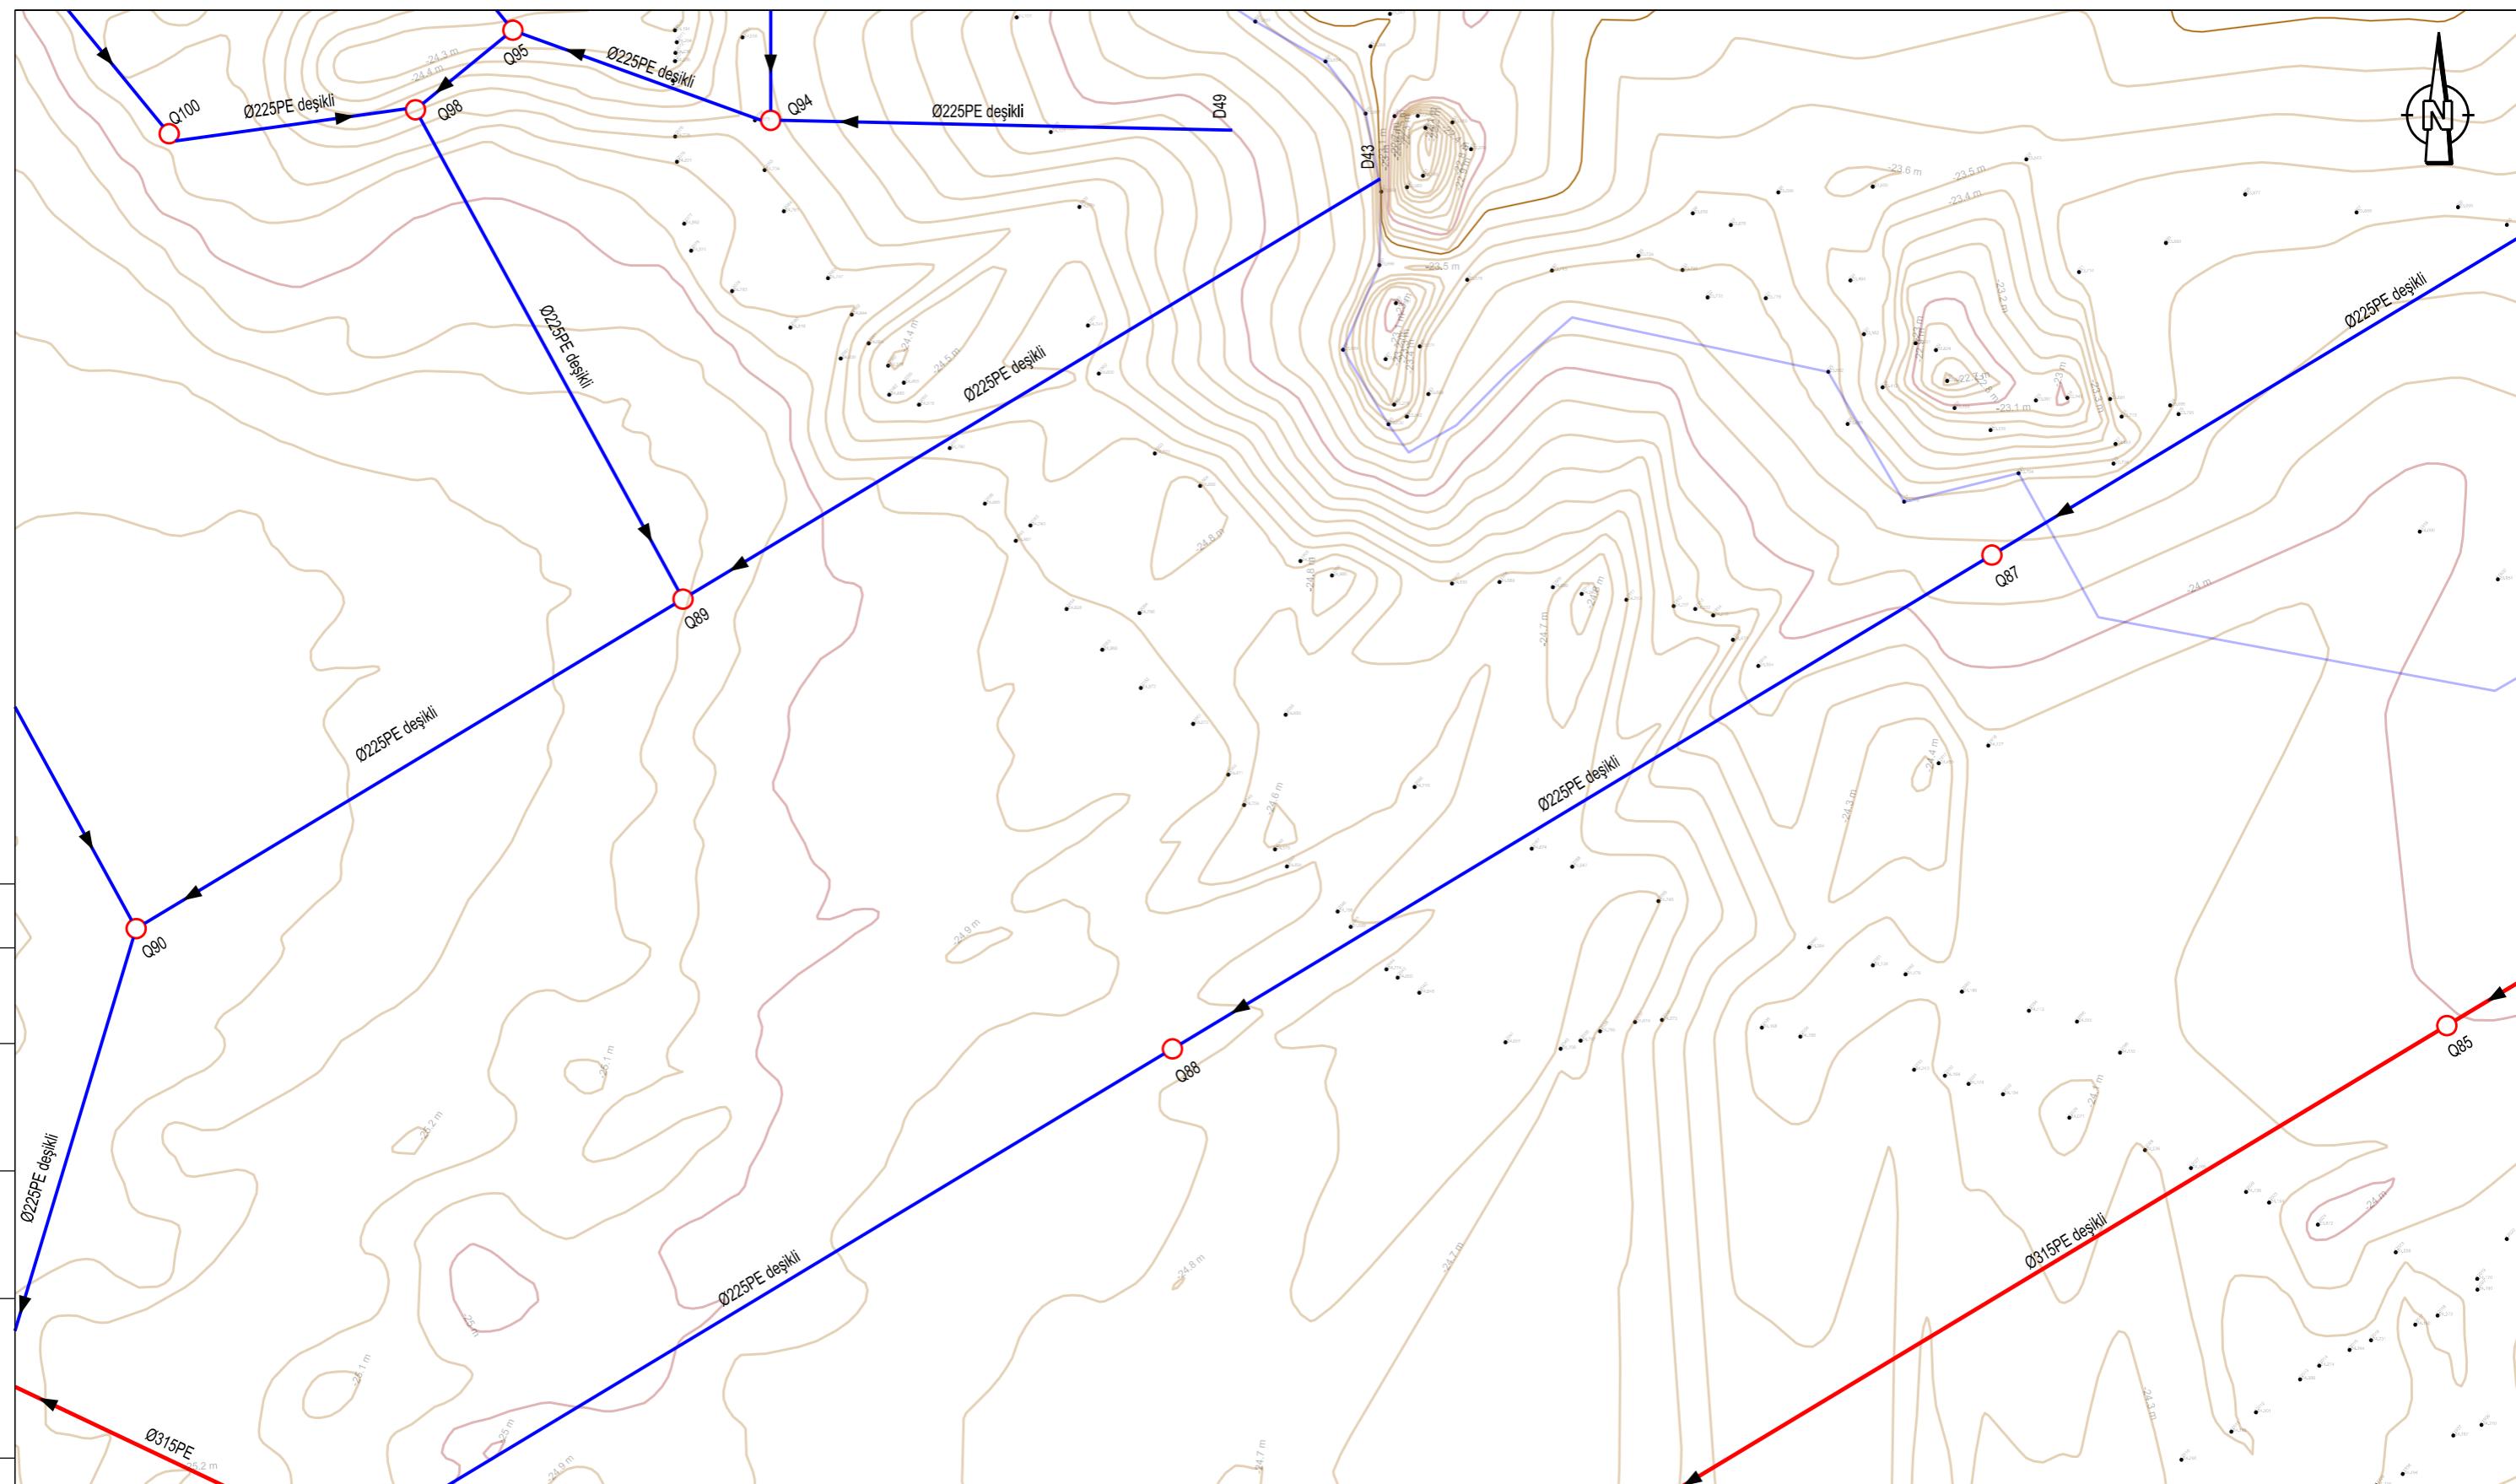

Cizgilərin birləşmə sxemi

Şərti işarələr

Ø225 HDPI

Ø315 HDPI

Baxış quyusu



2021/AT-04-DS-9.2.1


Tarix Suraxanı rayonunun inzibati ərazisində Zığ gölünün ətrafında yerləşən ərazilərdə yeni yaşlılıqların salınması və damcılı suvarma sisteminin qurulması

Dəyiş.	Dəy.s	Vərəq	Sən.№	İmza
LBM	T.Ağayev			
İşledi	N.Məmmədov			
Yoxladı	A. Aliev			
Normanəz.	Y. Sitnikova			

Drenaj sistemi

Drenaj sistemi planı(davamı)


EIB HYDROTRANS ENGINEERING
ENGINEERING CENTER FOR DESIGN OF WATER AND TRANSPORT INFRASTRUCTURE
SU VE NOKTULUŞ İNFRASTRUKTURULARIN LİYELİĞİNDEKİLİMİSİZ MÜHENDİSLİK

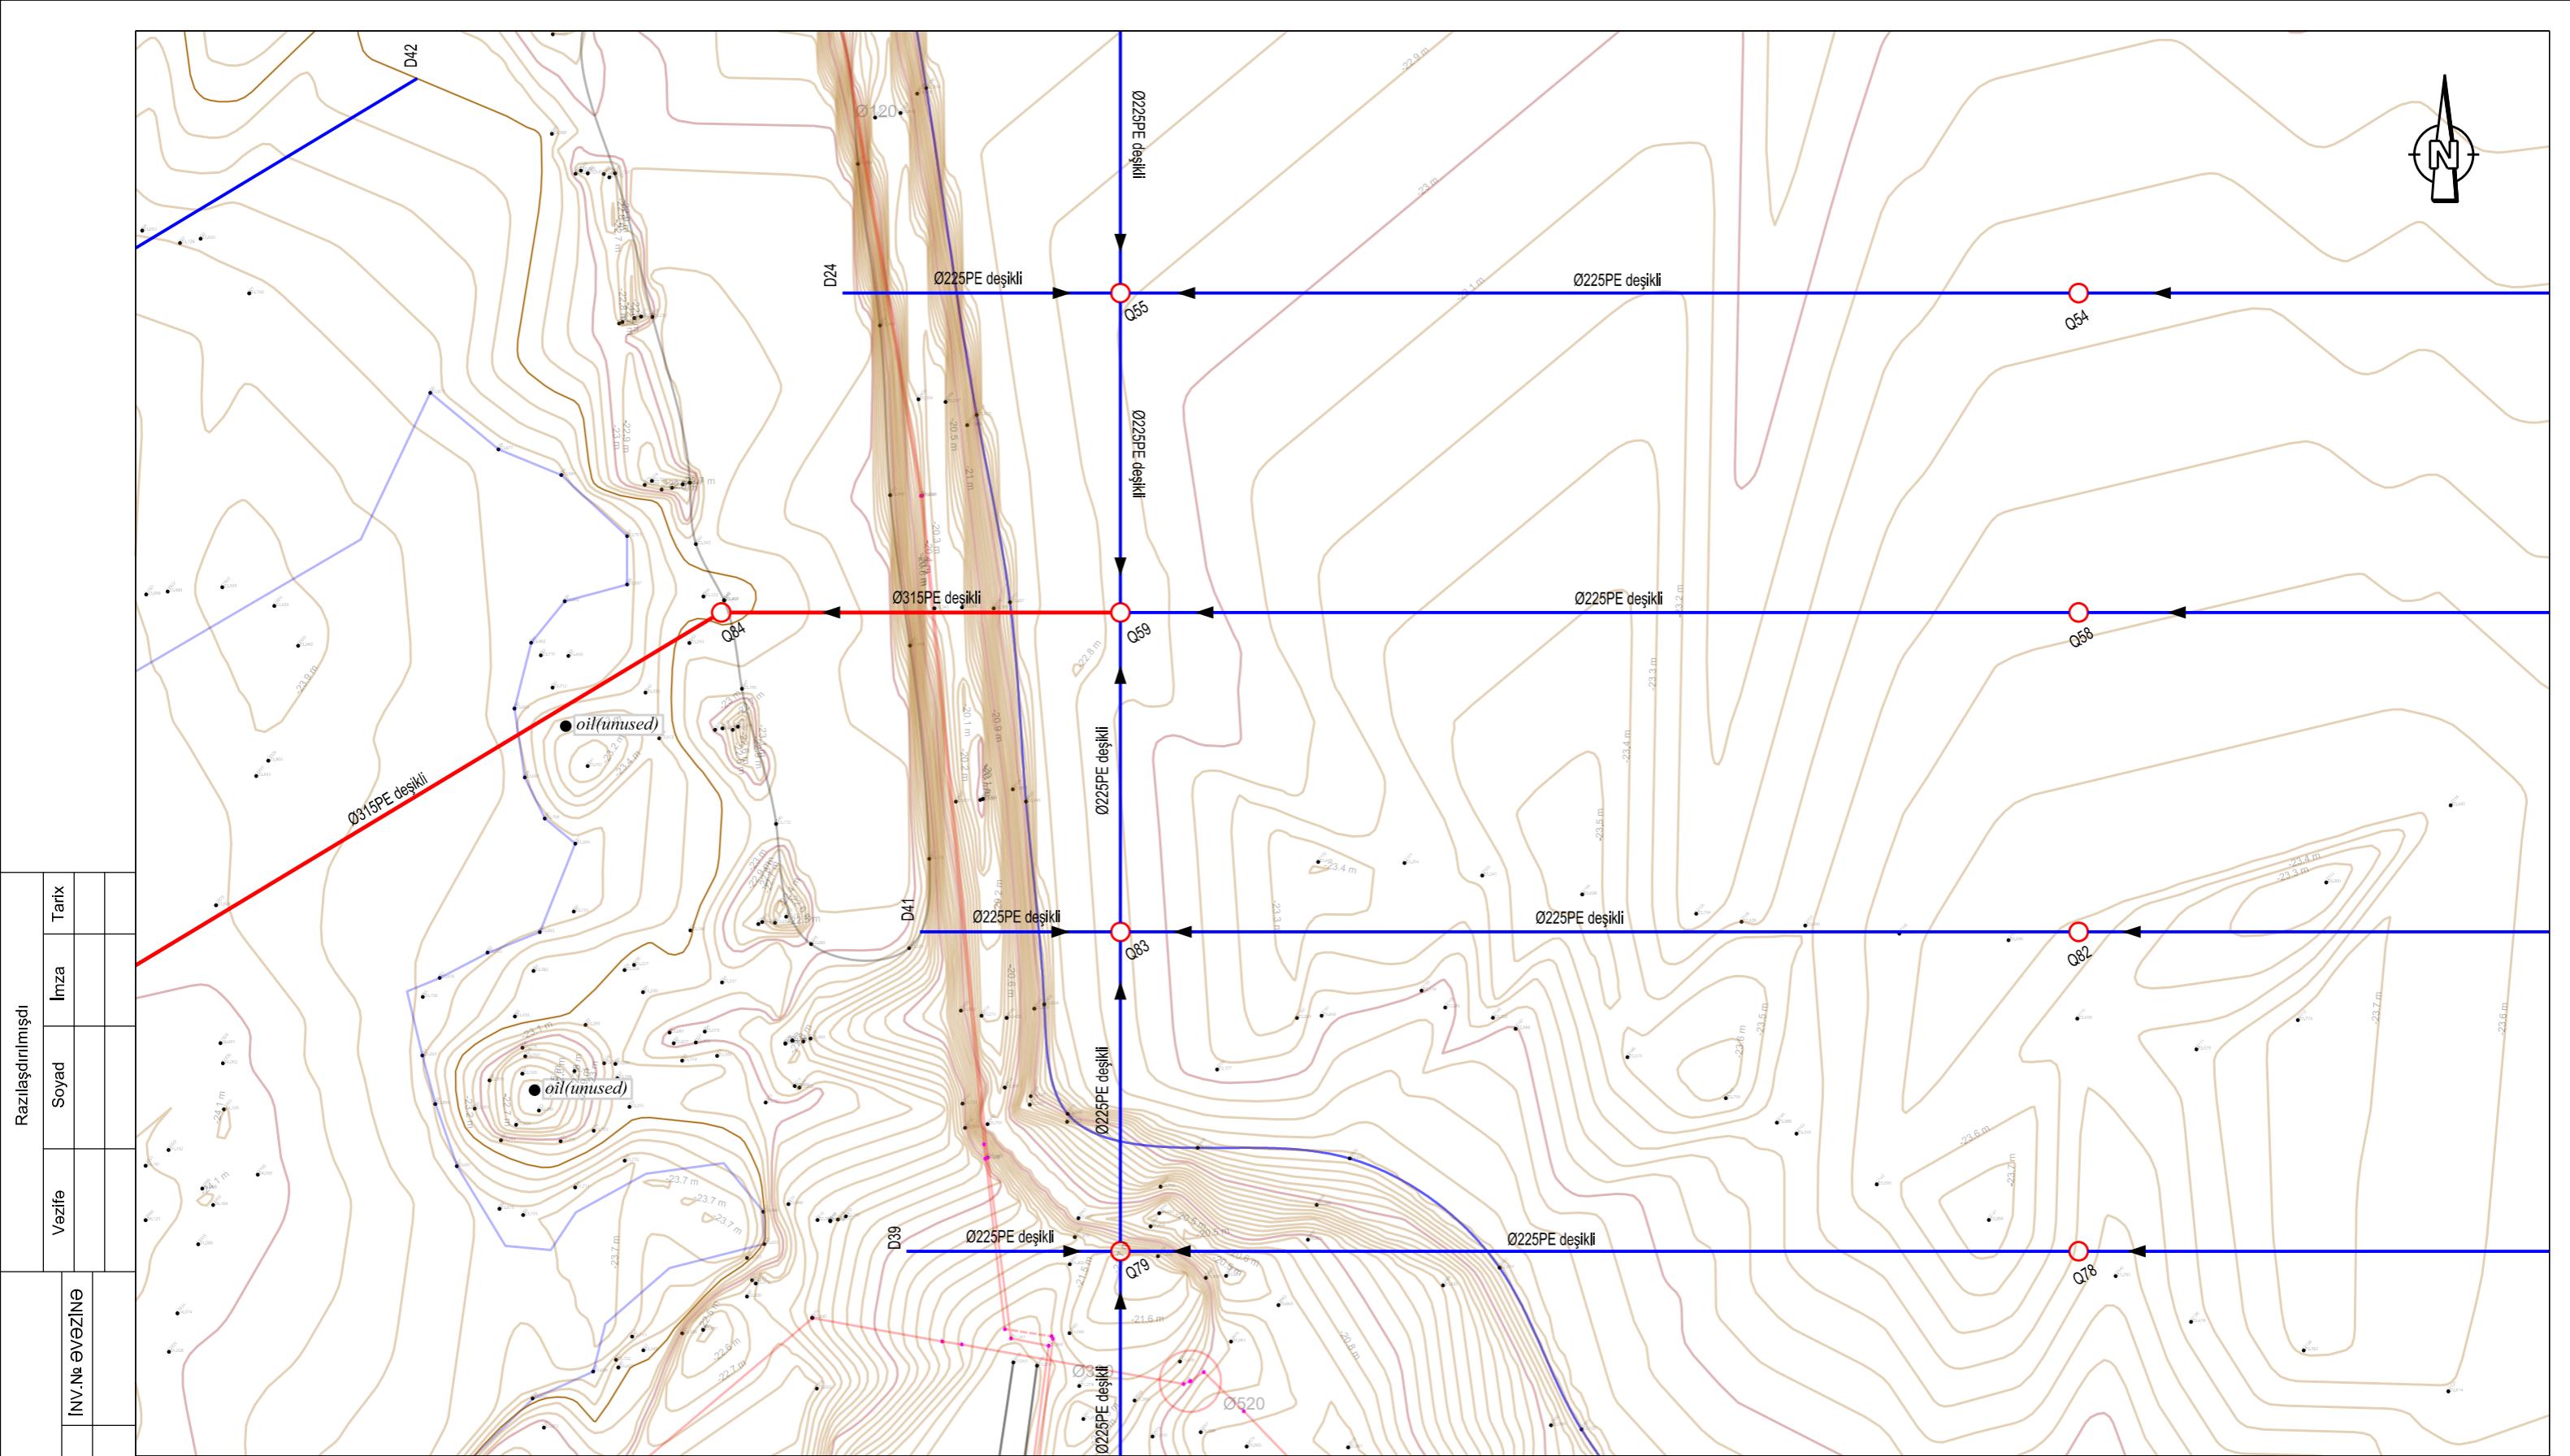


Razlışdırılmışlı					
Vəzifə	Soyad	İmza	Tarix		

INVENTAR №		IMZA VƏ TARIX	INV.NƏŞVƏZİNƏ

Cizgilərin birləşmə sxemi

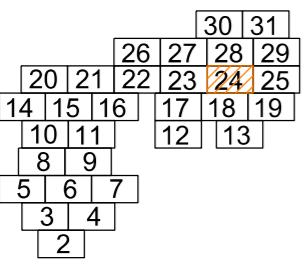

Şerti işarələr

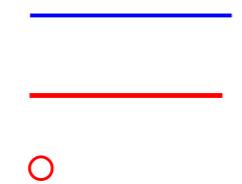

Ø225 HDPE

Ø315 HDPE

Baxış quyusu


2021/AT-04-DS-9.2.1

Suraxanı rayonunun inzibati ərazisində Zığ gölünün ətrafında
yerləşən ərazilərdə yeni yaşlılıqların salınması və damcılı suvarma
sisteminin qurulması


Dəyiş.	Dəy.s	Vərəq	Sən.Nö	İmza	Tarix
LBM	T.Ağayev				
İşlədi	N.Məmmədov				
Yoxladı	A. Aliyev				
Normanəz.	Y. Sitnikova				

Drenaj sistemi

Drenaj sistemi planı(davamı)

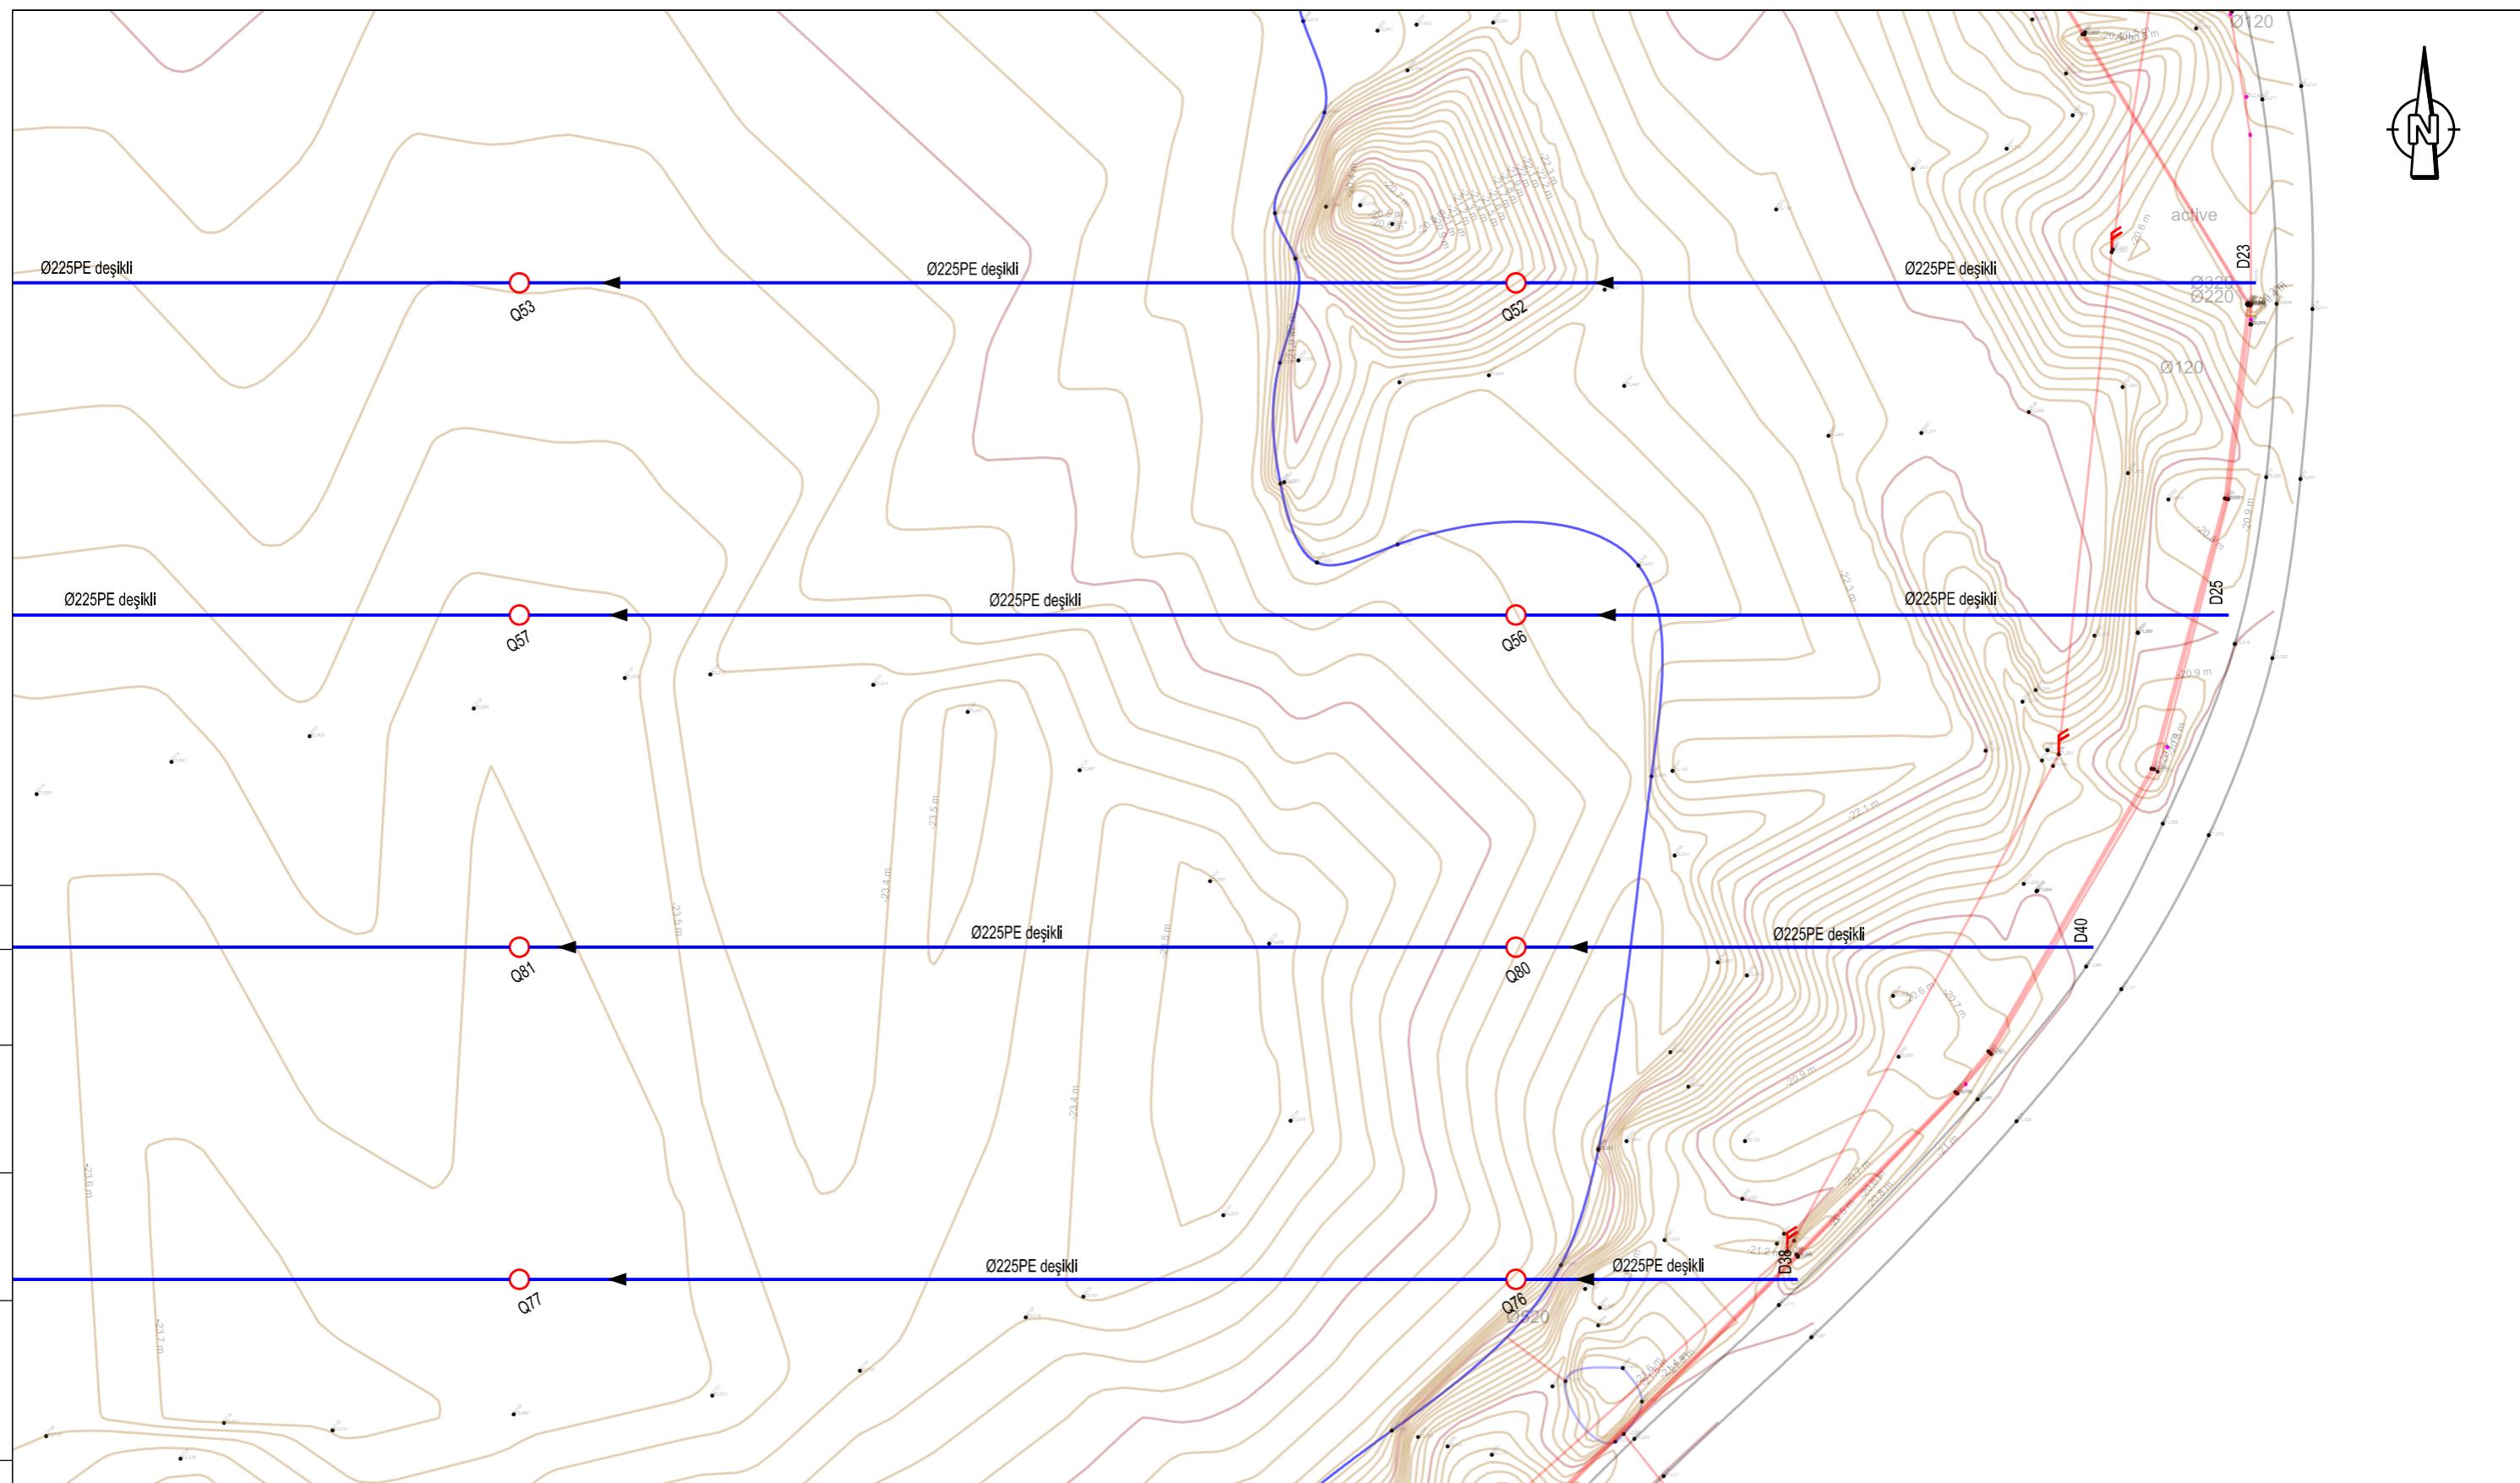

Cizgilərin birləşmə sxemi

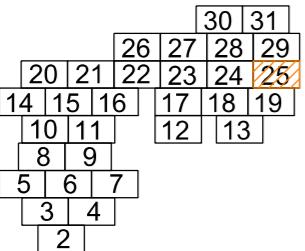


Şərti işarələ

Ø225 HDP

Ø315 HDP

Baxış quyu

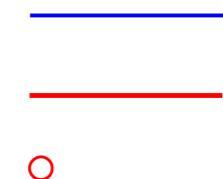


2021/AT-04-DS-9.2.1


Dəyiş.	Dəy.s	Vərəq	Sən.Nö	İmza	T
LBM		T.Ağayev			
İşlədi		N.Məmmədov			
Yoxladı		A. Aliyev			
Normanəz.		Y. Sitnikova			

2021/AT-04-DS-9.2.1

EIB HYDROTRANS ENGINEERING
ENGINEERING CENTER FOR DESIGN OF WATER AND TRANSPORT INFRASTRUCTURE
SU YO NOLQYATI INFRASTRUCTURALARIN LAYBEGLIDILISHIMIZ (ÜZGÜ MÖHÜRSÜLKÜ MÖHÜRÜ)

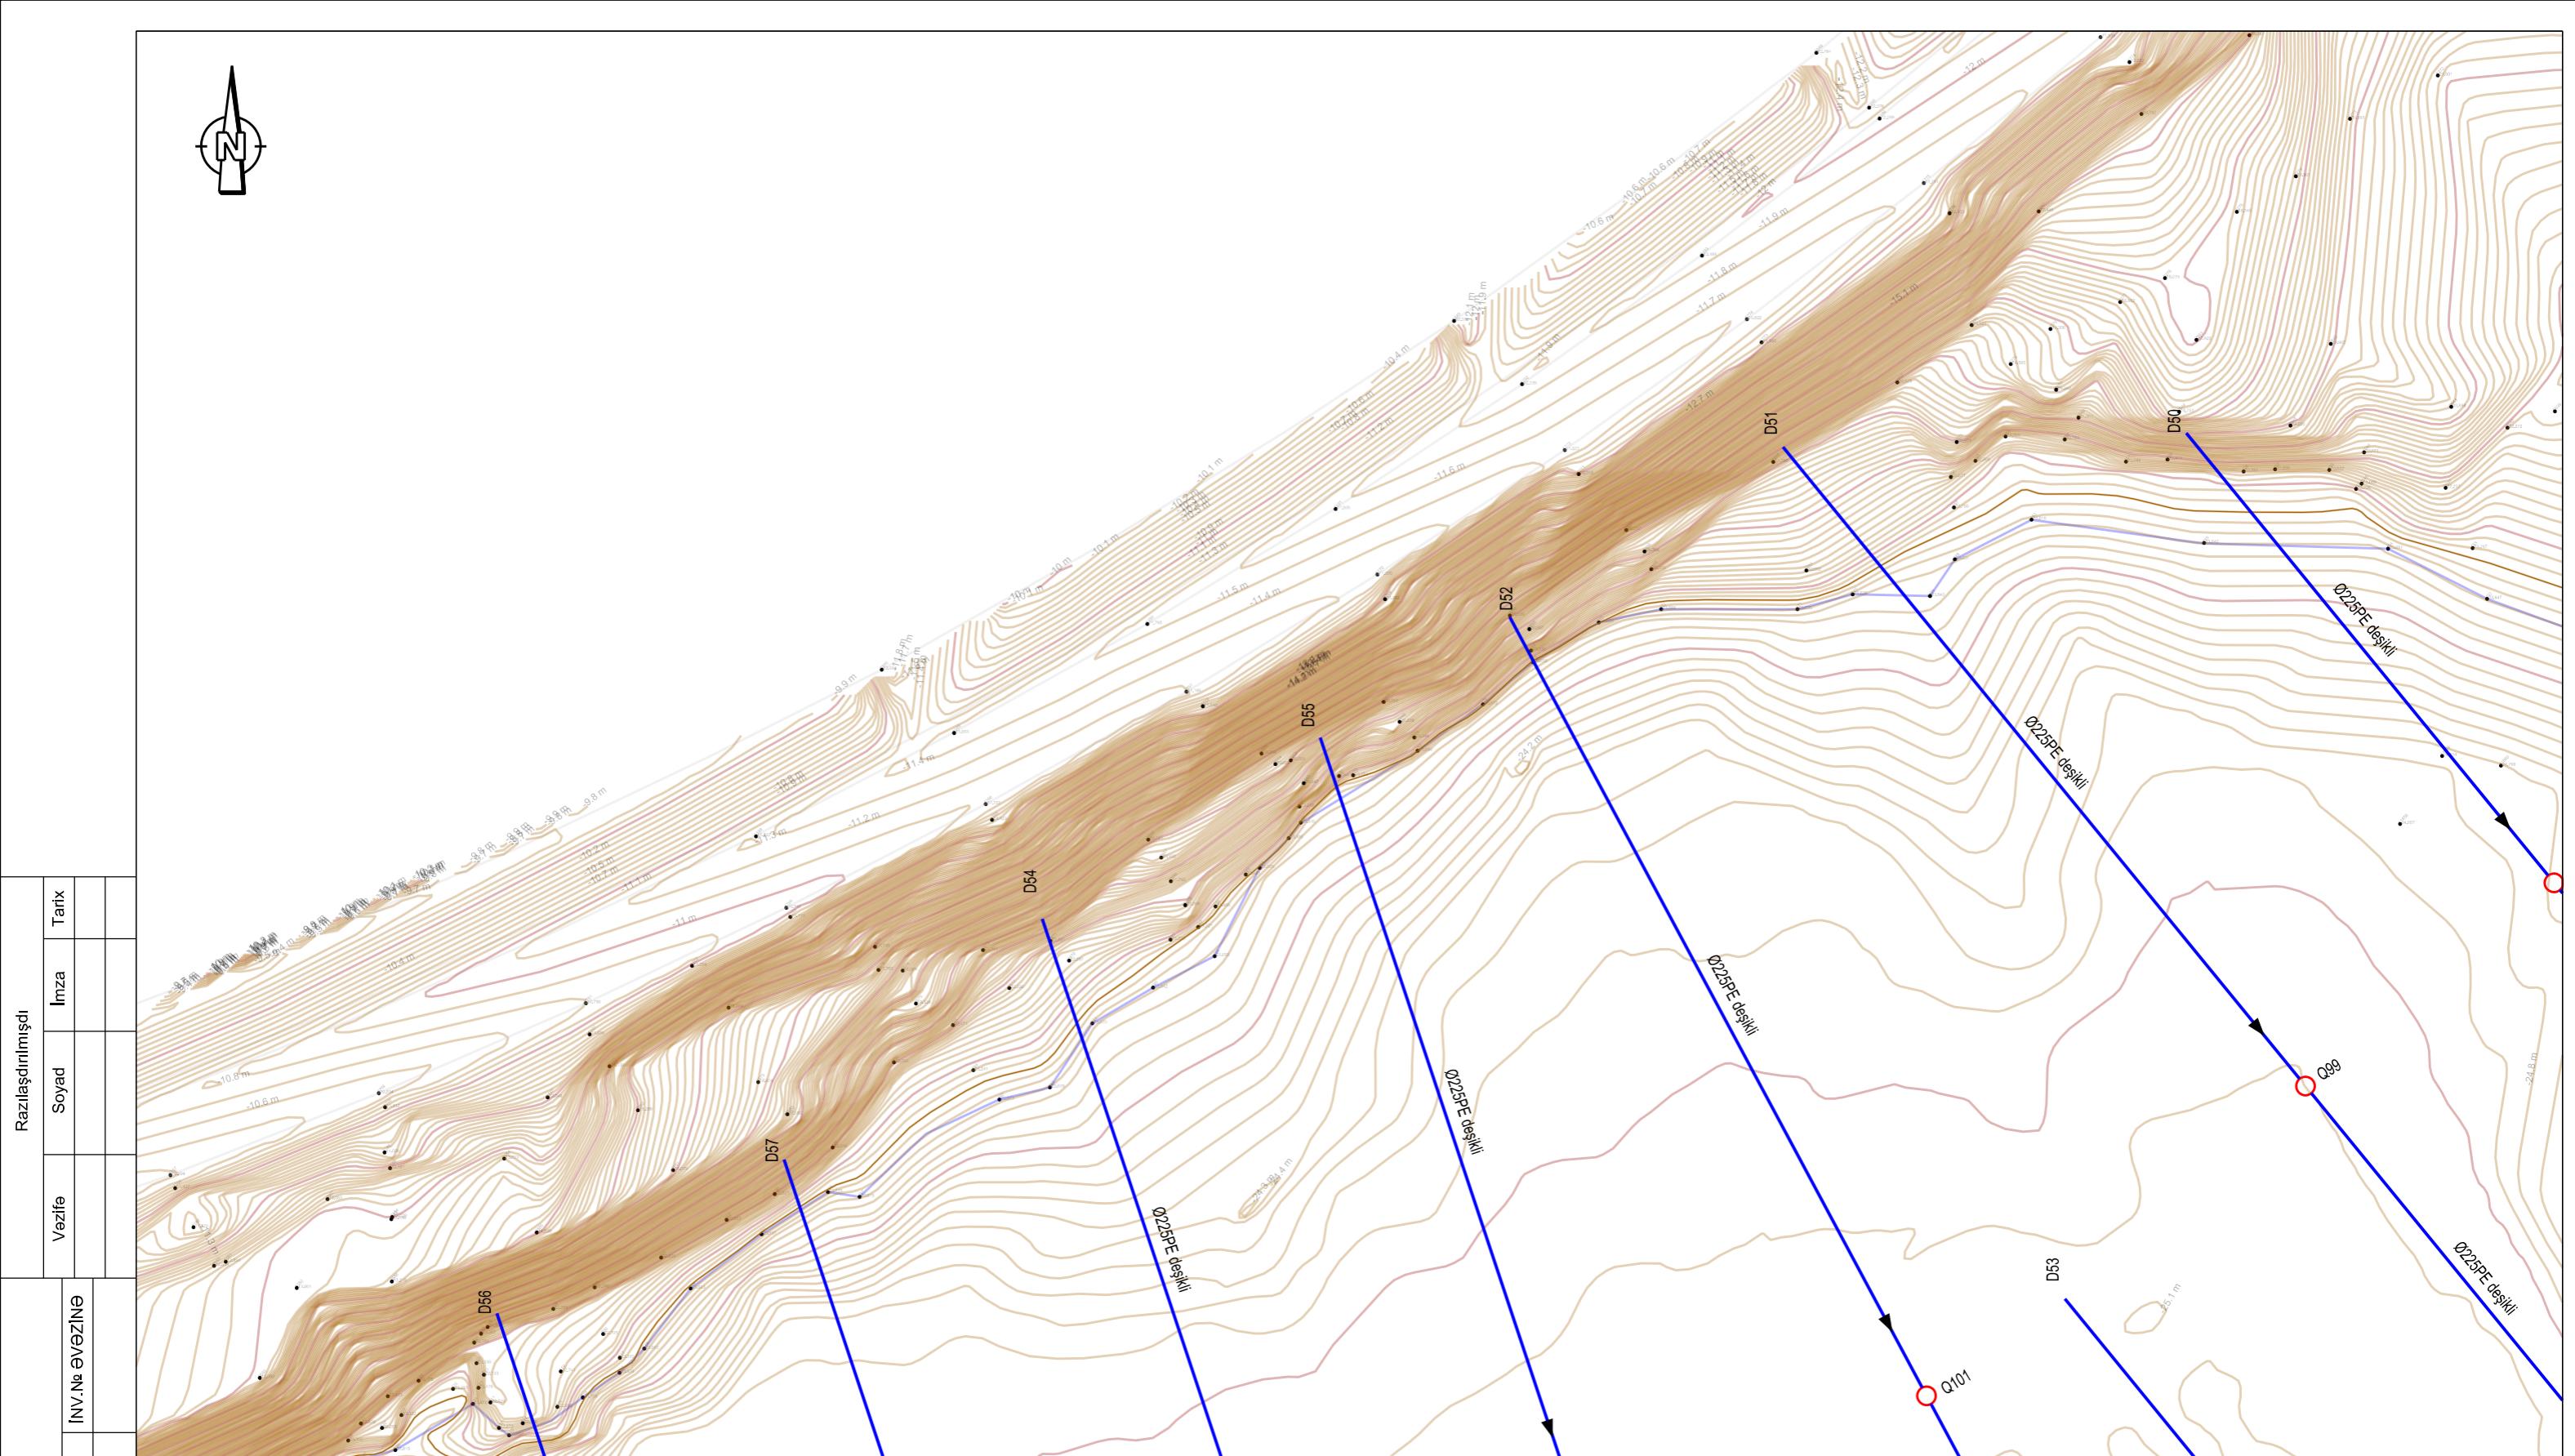

Cizgilərin birləşmə sxemi

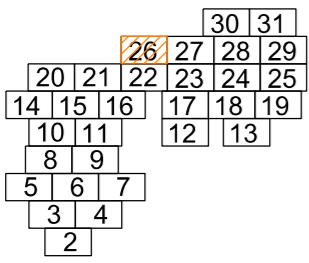

Şərti işarələr

Ø225 HDPE

Ø315 HDPE

Baxış quyusu

○

2021/AT-04-DS-9.2.1


Tarix Suraxanı rayonunun inzibati ərazisində Zığ gölünün ətrafında yerləşən ərazilərdə yeni yaşlılıqların salınması və damcılı suvarma sisteminin qurulması

Dəyiş.	Dəy.s	Vərəq	Sən.Nö	İmza
LBM	T.Ağayev			<u>Ağayev</u>
İşlədi	N.Məmmədov			<u>Məmmədov</u>
Yoxladı	A. Aliyev			<u>Aliyev</u>
Normanəz.	Y. Sitnikova			<u>Sitnikova</u>

Drenaj sistemi

HYDROTRANS ENGINEERING
ENGINEERING CENTER FOR DESIGN OF WATER AND TRANSPORT INFRASTRUCTURE
SU VE NÖVÜLYAT INFRASTRUKTURALARIN LATHIGOLGUDKILMESİ (2020 MÜHENDİSLİK MÜRSİDİ)

Format A3

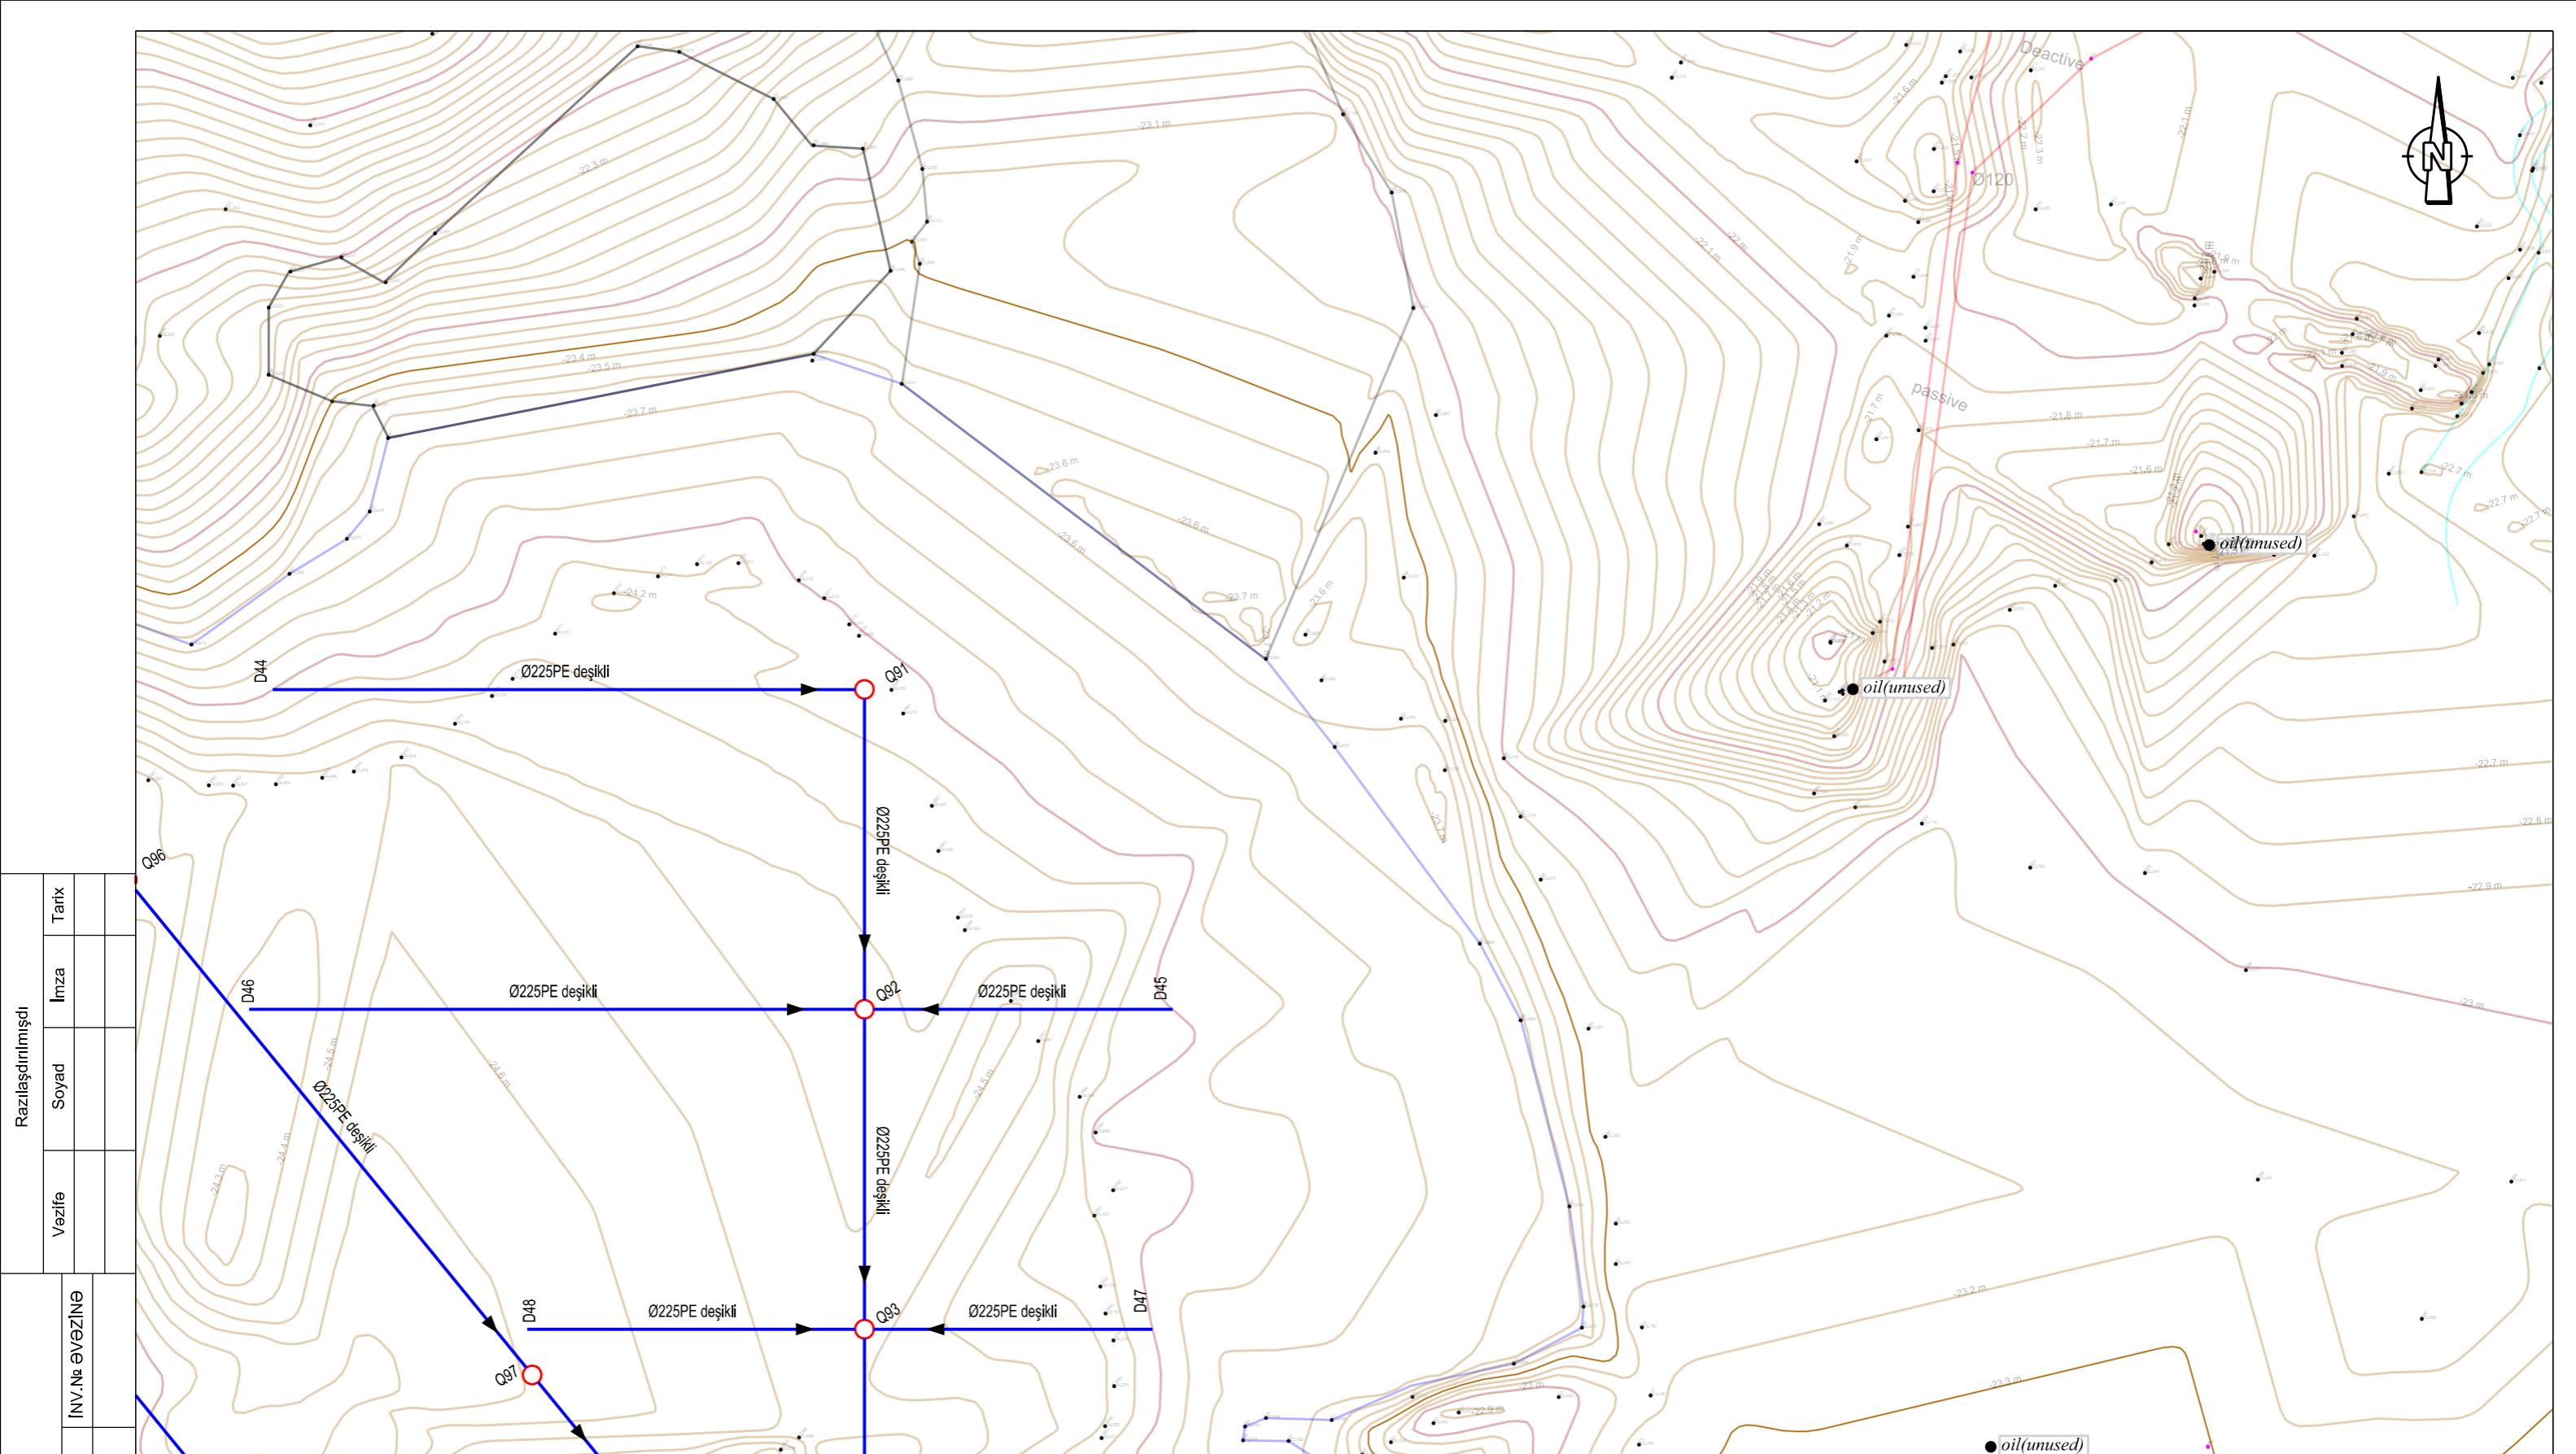


Razlaşdırılmışdı

Vəzifə	Soyad	İmza	Tarix

INV.NƏVƏZİNƏ

INVENTAR №	IMZA VƏ TARIX

Cizgilərin birləşmə sxemi

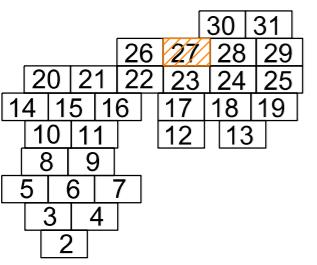

Şerti işarələr



Ø225 HDPE



Ø315 HDPE



Baxış quyusu

2021/AT-04-DS-9.2.1

Suraxanı rayonunun inzibati ərazisində Zığ gölünün ətrafında
yerləşən ərazilərdə yeni yaşlılıqların salınması və damcılı suvarma
sisteminin qurulması


Dəyiş.	Dəy.s	Vərəq	Sən.Nö	İmza	Tarix
LBM	T.Ağayev				
İşlədi	N.Məmmədov				
Yoxladı	A. Aliyev				
Normanəz.	Y. Sitnikova				

Drenaj sistemi

mərhələ	vərəq	vərəqlər
İL	27	84

Drenaj sistemi planı(davamı)

EIB	HYDROTRANS ENGINEERING
	SU NAQDÝYAT INFRASTRÜKTURUNA LAŞIQLANDIRILMƏSI İZƏT MƏRNİYƏT NƏTİCƏSİ

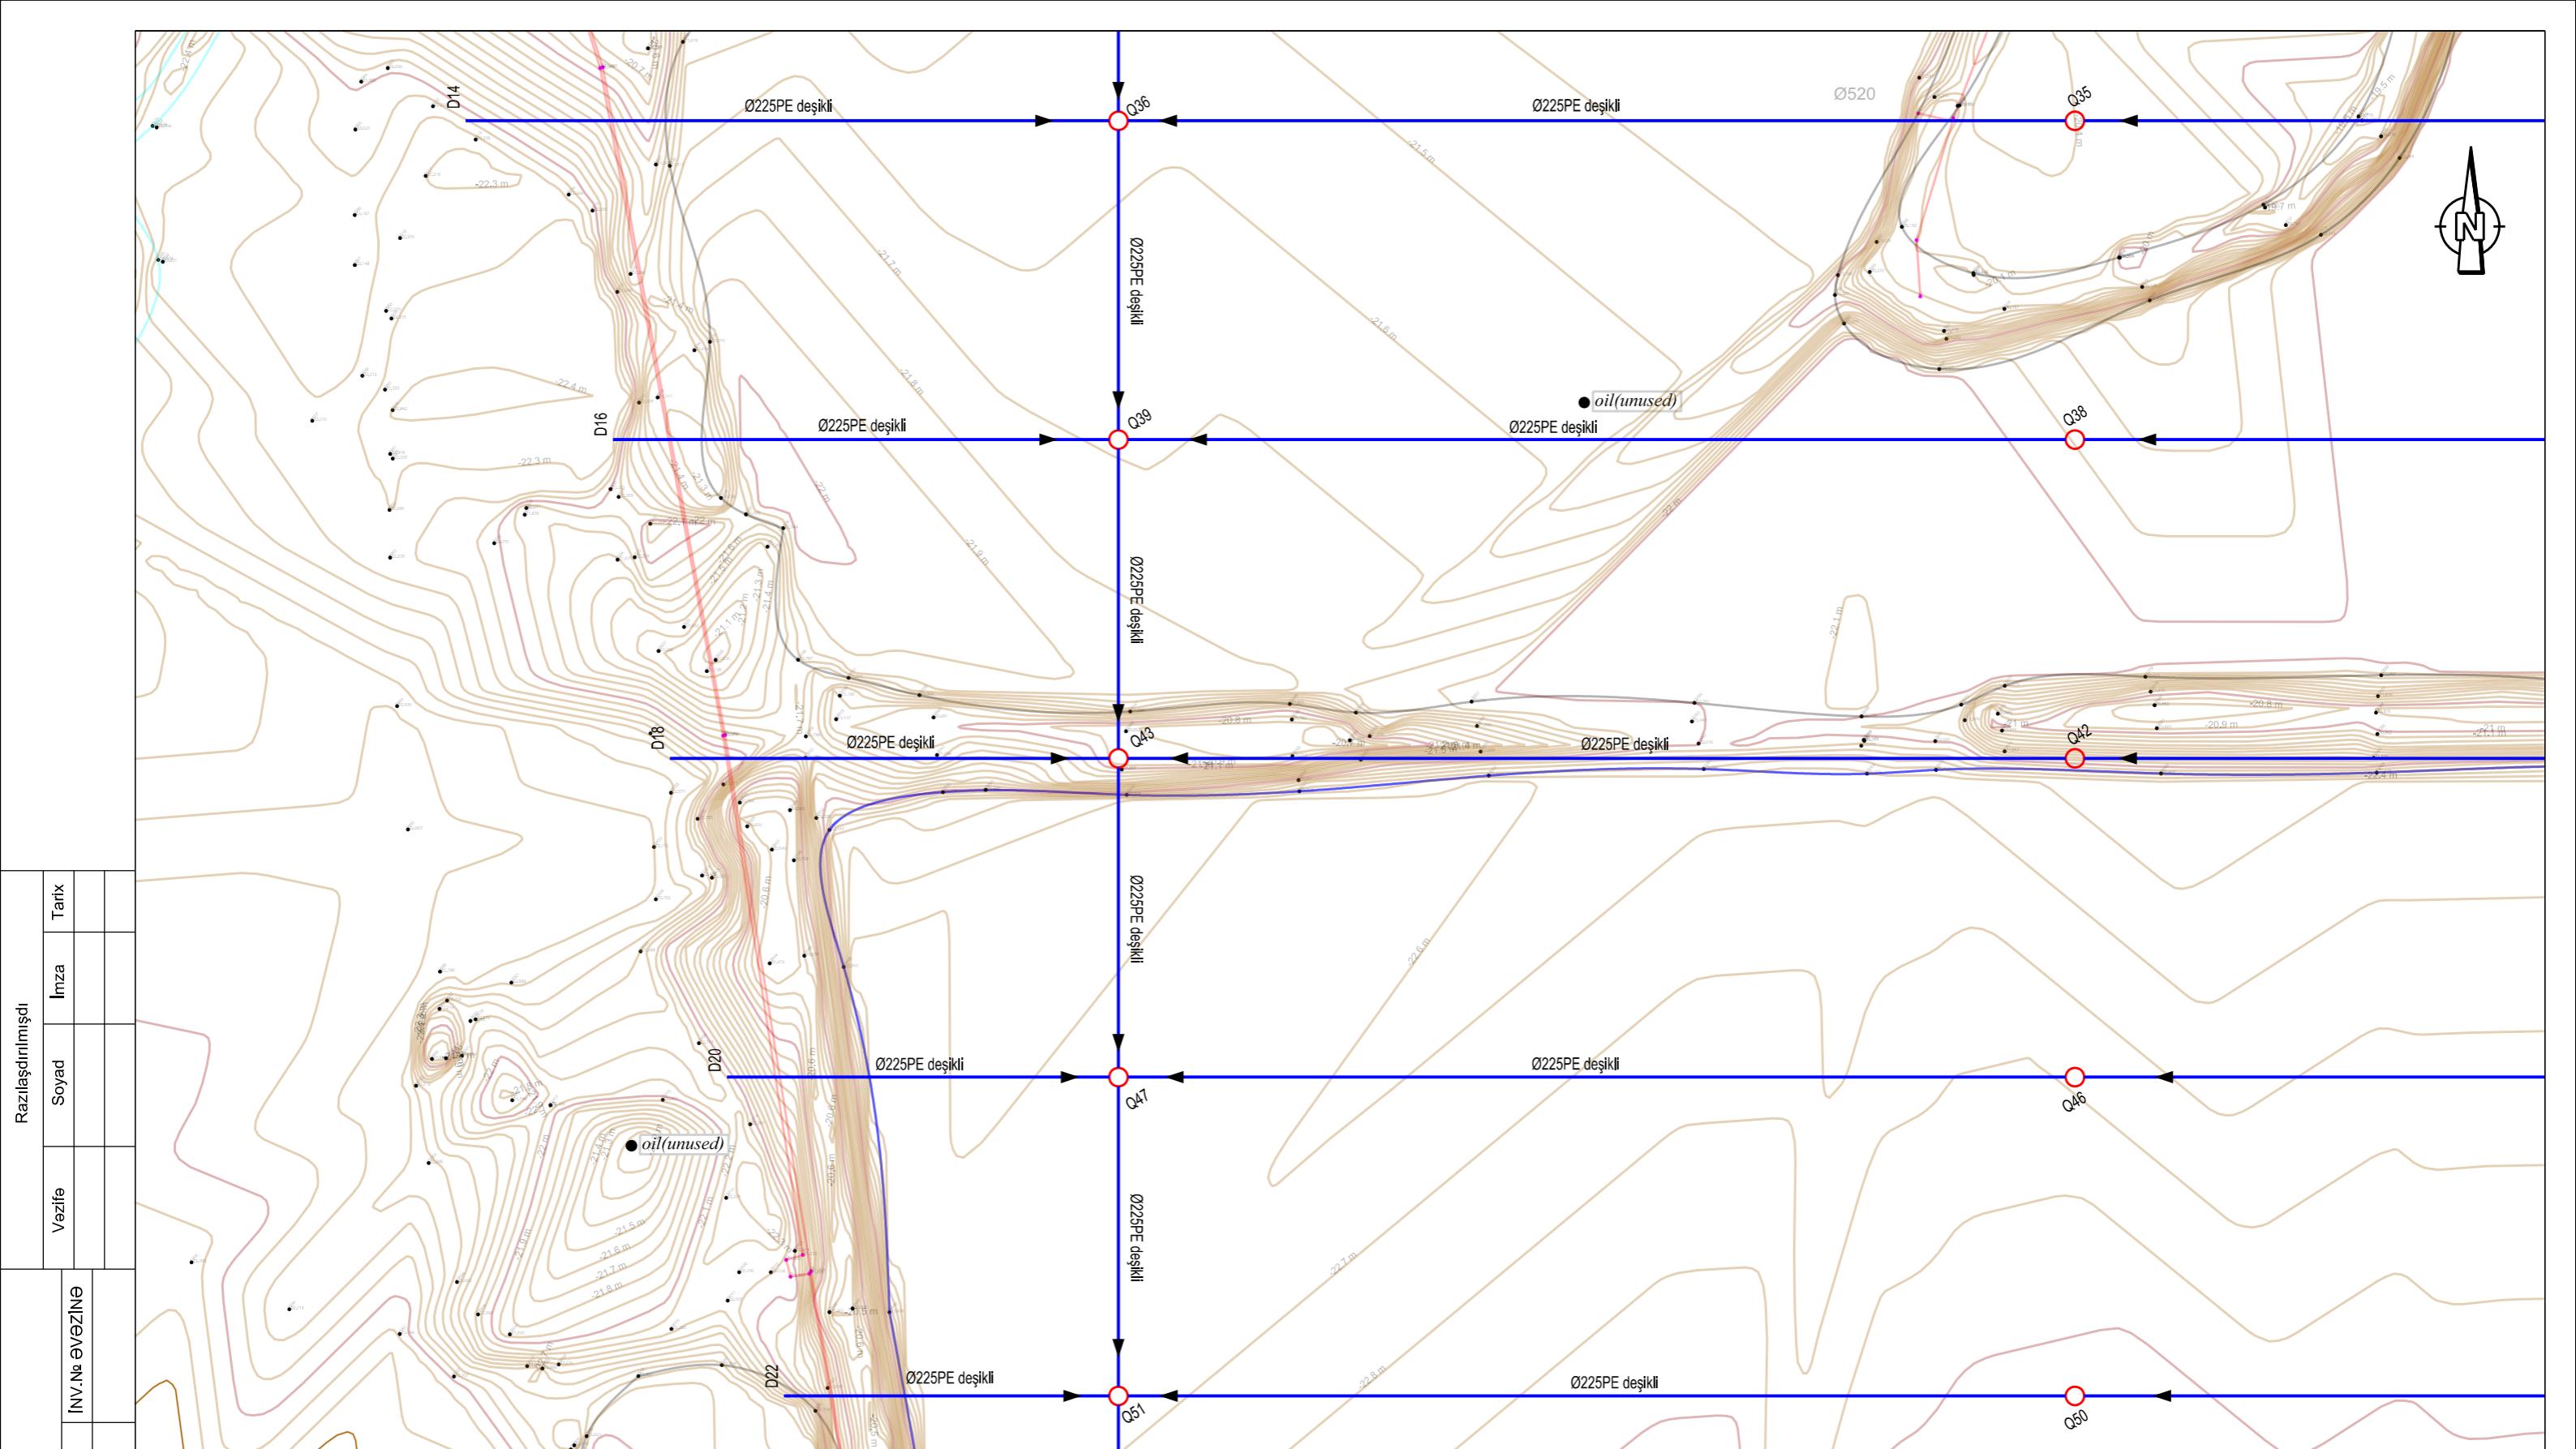


Razlaşdırılmış

Vəzifə	Soyad	İmza	Tarix


INV.NƏVƏZİNƏ

INVENTAR №	IMZA VƏ TARIX

Cizgilərin birləşmə sxemi

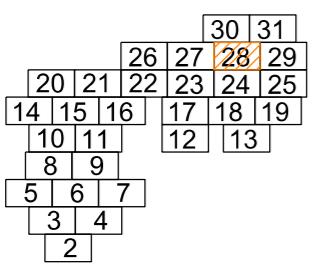

Şerti işarələr

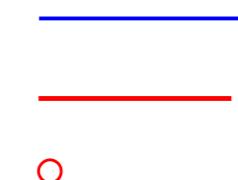

Ø225 HDPE

Ø315 HDPE

Baxış quyusu


2021/AT-04-DS-9.2.1

Suraxanı rayonunun inzibati ərazisində Zığ gölünün ətrafında
yerləşən ərazilərdə yeni yaşlılıqların salınması və damcılı suvarma
sisteminin qurulması

Dəyiş.	Dəy.s	Vərəq	Sən.Nö	İmza	Tarix
LBM	T.Ağayev				
İşlədi	N.Məmmədov				
Yoxladı	A. Aliyev				
Normanəz.	Y. Sitnikova				


Drenaj sistemi planı(davamı)

EIB HYDROTRANS ENGINEERING
ENGINEERING CENTER FOR DESIGN OF WATER AND TRANSPORT INFRASTRUCTURE
SU NƏqliyyat İnfrastrukturlarının Layihələndirilməsi Üzrə Mərkəzlilik Mərkəzi

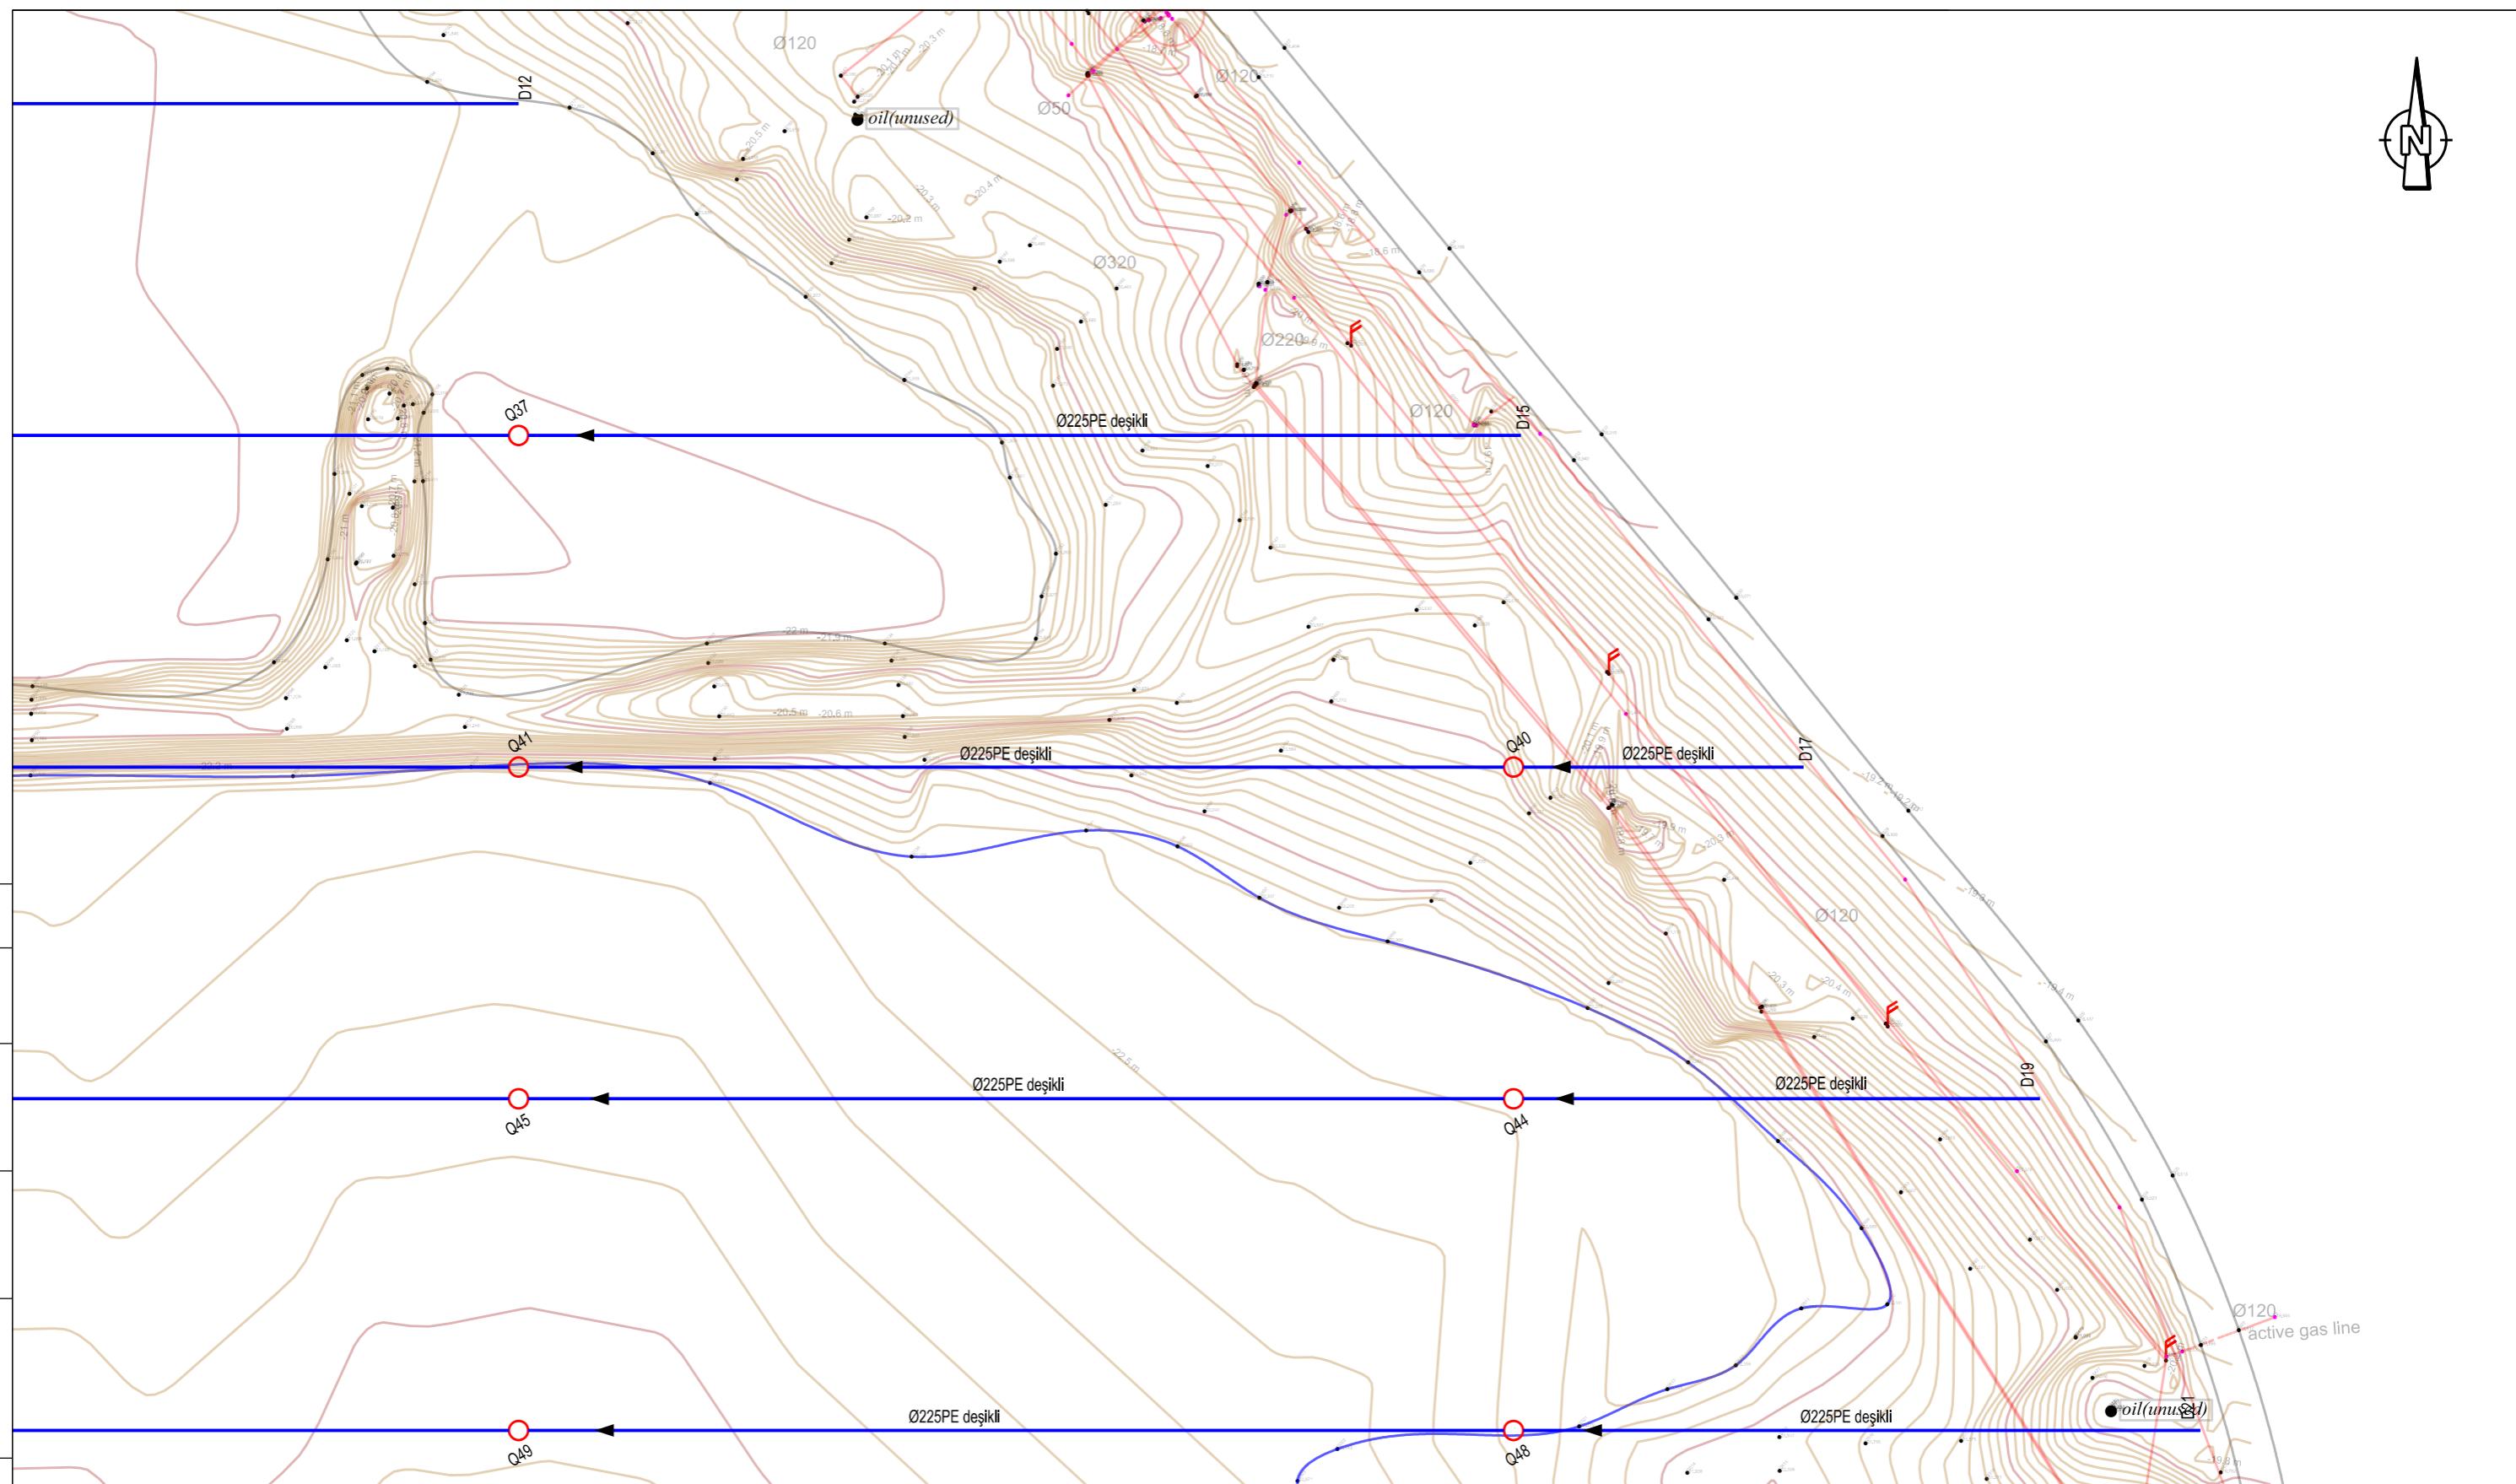

INVENTAR №		İMZА VƏ TARİХ	INV.Nº ΘVΘΖΙΝΘ	Razlaşdırılmışdı		
Vəzifə	Soyad	İmza	Tarix			

Cizgilərin birləşmə sxemi

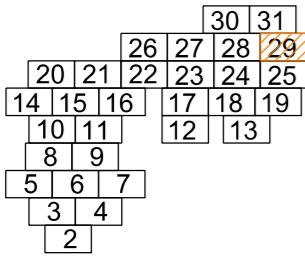

Şərti işarələ

Ø225 HD

Ø315 HD

Baxış quy

ANSWER

○

2021/AT-04-DS-9.2.1


Suraxanı rayonunun inzibati ərazisində Ziğ gölünün ətrafında yerləşən ərazilərdə yeni yaşlılıqların salınması və damcılı suvarma sisteminin qurulması

Dəyiş.	Dəy.s	Vərəq	Sən.Nö	İmza
LBM	T.Ağayev			
İşlədi	N.Məmmədov			
Yoxladı	A. Aliyev			
Normanəz.	Y. Sitnikova			

Drenaj sistēma

renaj sistemi planı(davamı)

EIB HYDROTRANS ENGINEERING
ENGINEERING CENTER FOR DESIGN OF WATER AND TRANSPORT INFRASTRUCTURE
SU VE NÜZYAT İNFRASTRUCTURELARIN LAHİZHƏMİLÇİ QƏZİ MƏHİNƏLİK MƏRKƏZİ

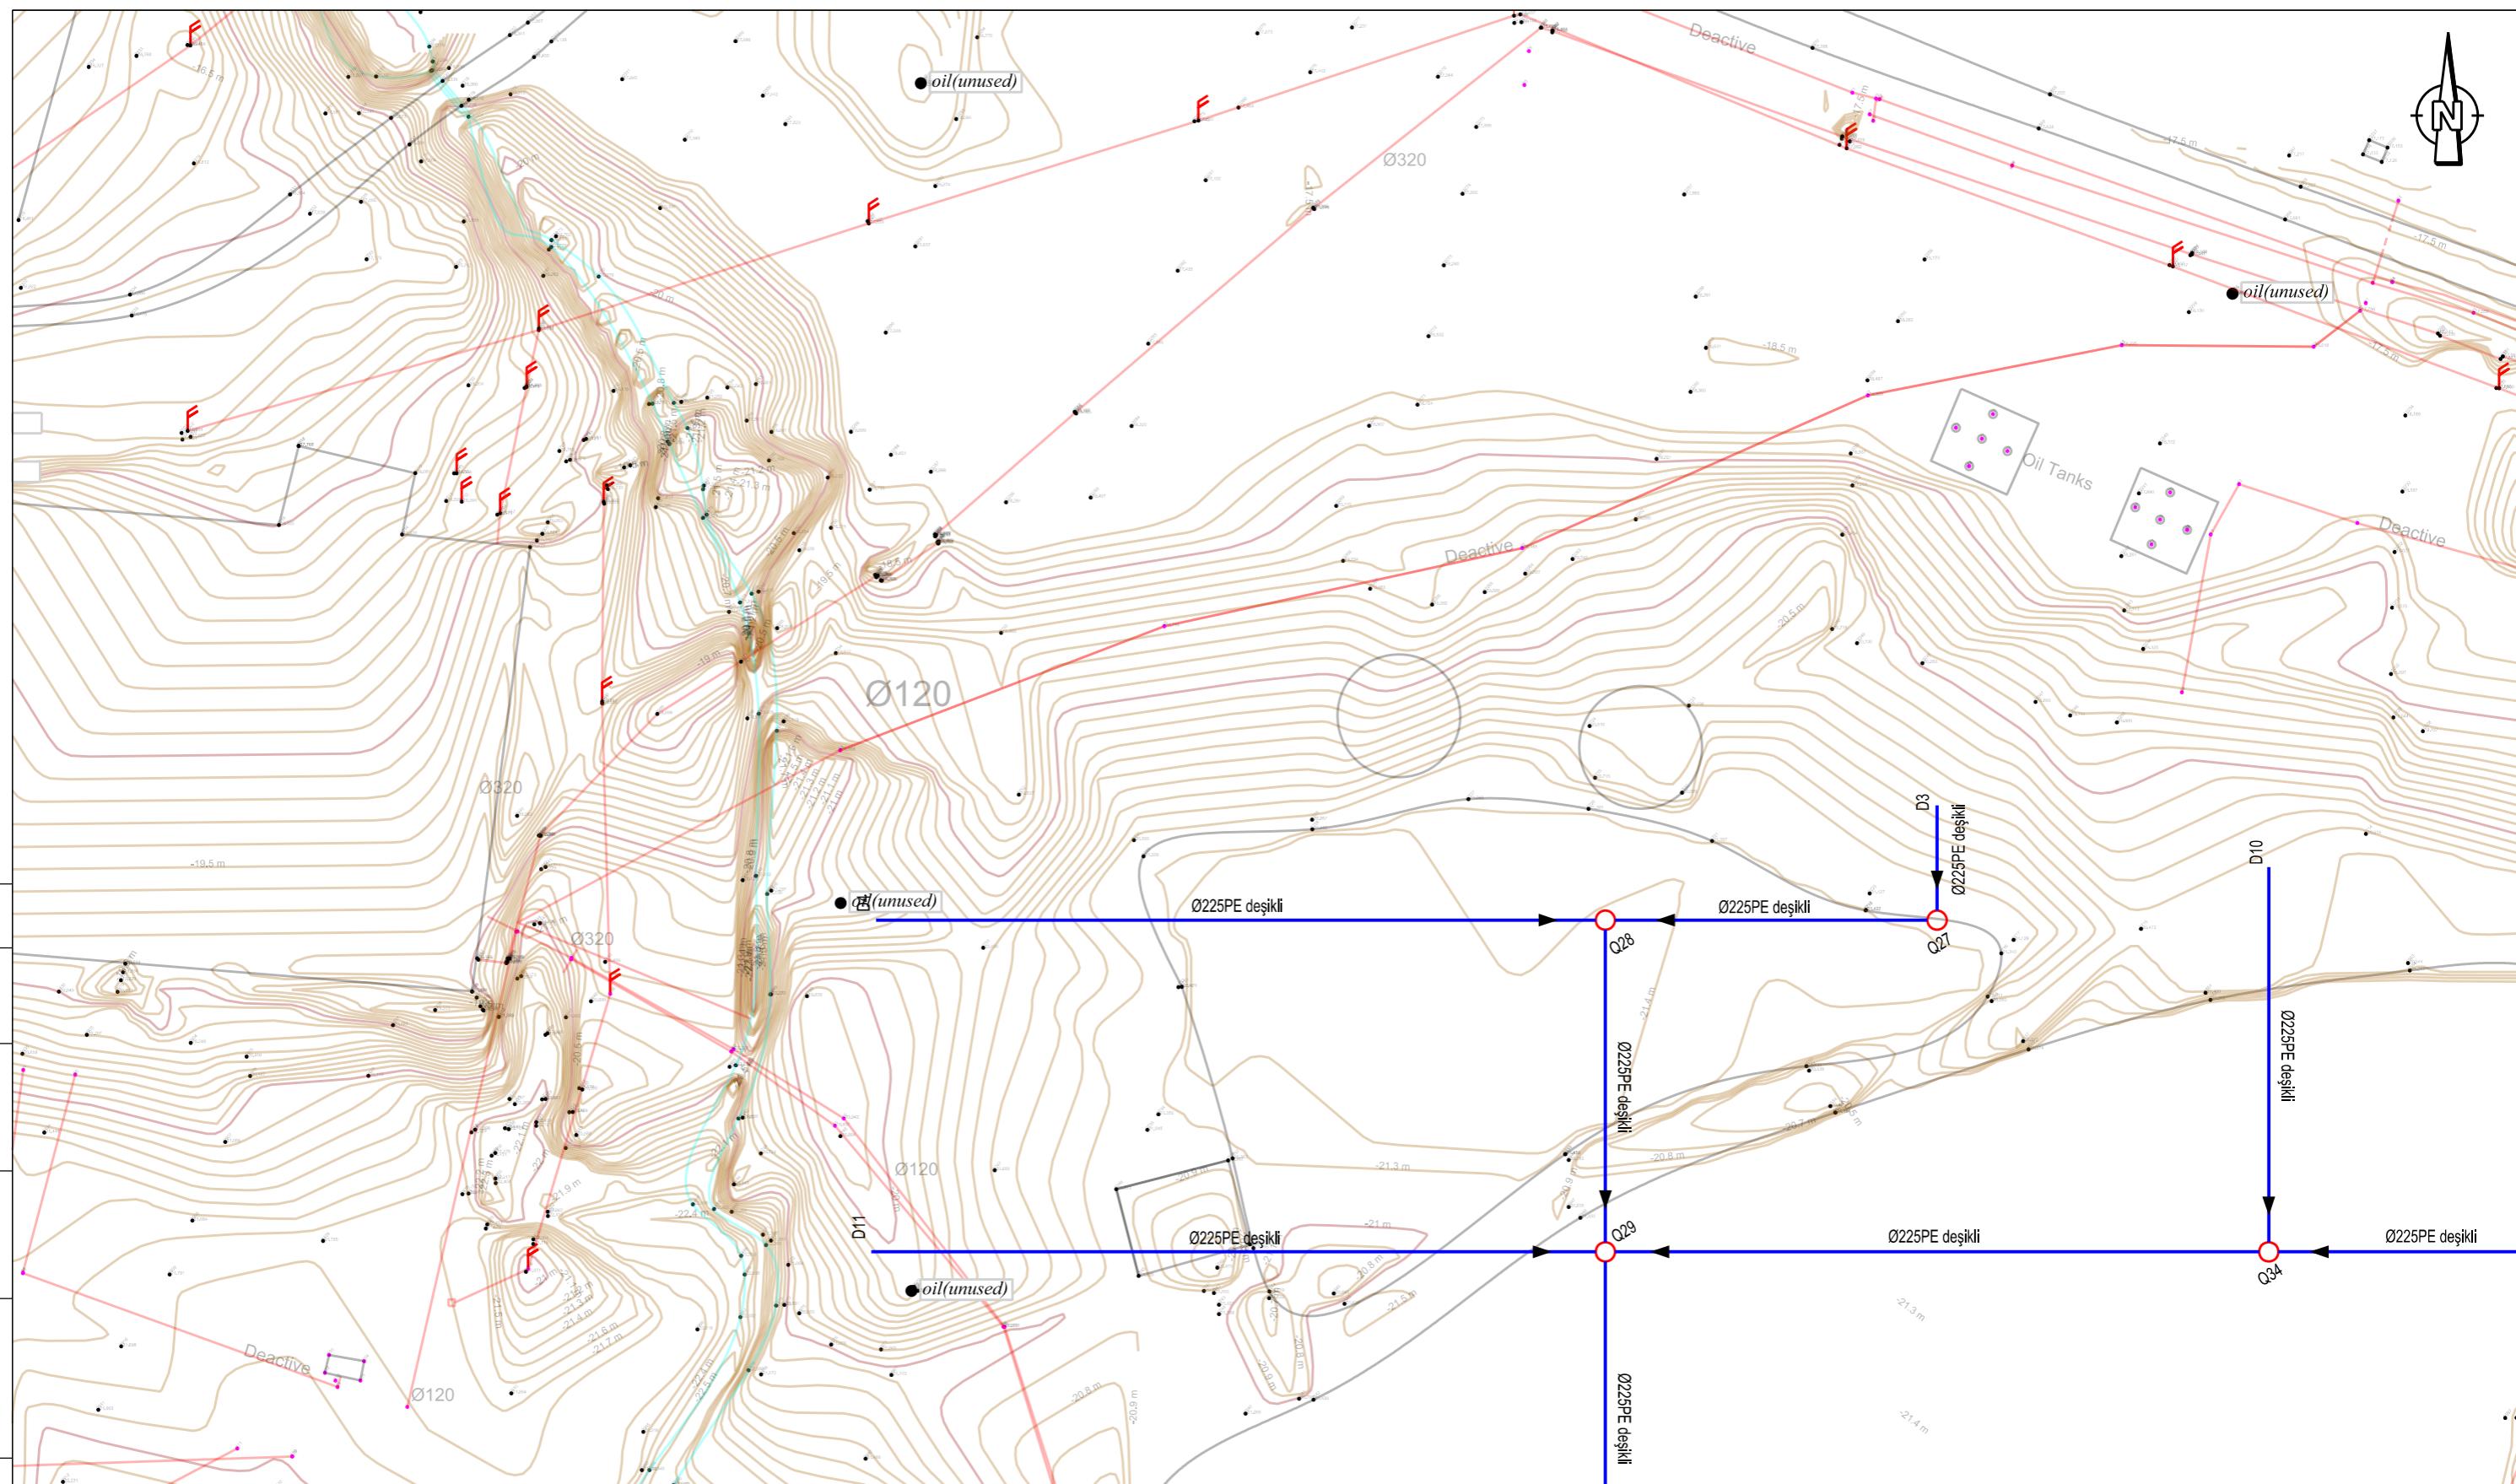

Cizgilərin birləşmə sxemi

			30	31
26	27	28	29	
20	21	22	23	25
14	15	16	17	18
10	11		12	13
8	9			
5	6	7		
3	4			
2				

Şərti işarələr

Ø225 HDPI

Ø315 HDPI

Baxış quyusu

2021/AT-04-DS-9.2.1


Tarix Suraxanı rayonunun inzibati ərazisində Ziğ gölünün ətrafında yerləşən ərazilərdə yeni yaşlılıqların salınması və damcılı suvarma sisteminin qurulması

Dəyiş.	Dəy.s	Vərəq	Sən.Nö	İmza
LBM	T.Ağayev			
İşlədi	N.Məmmədov			
Yoxladı	A. Aliyev			
Normanəz.	Y. Sitnikova			


Drenai sistēma

Table 1: Summary of experimental results

 HYDROTRANS ENGINEERING
ENGINEERING CENTER FOR DESIGN OF WATER AND TRANSPORT INFRASTRUCTURE

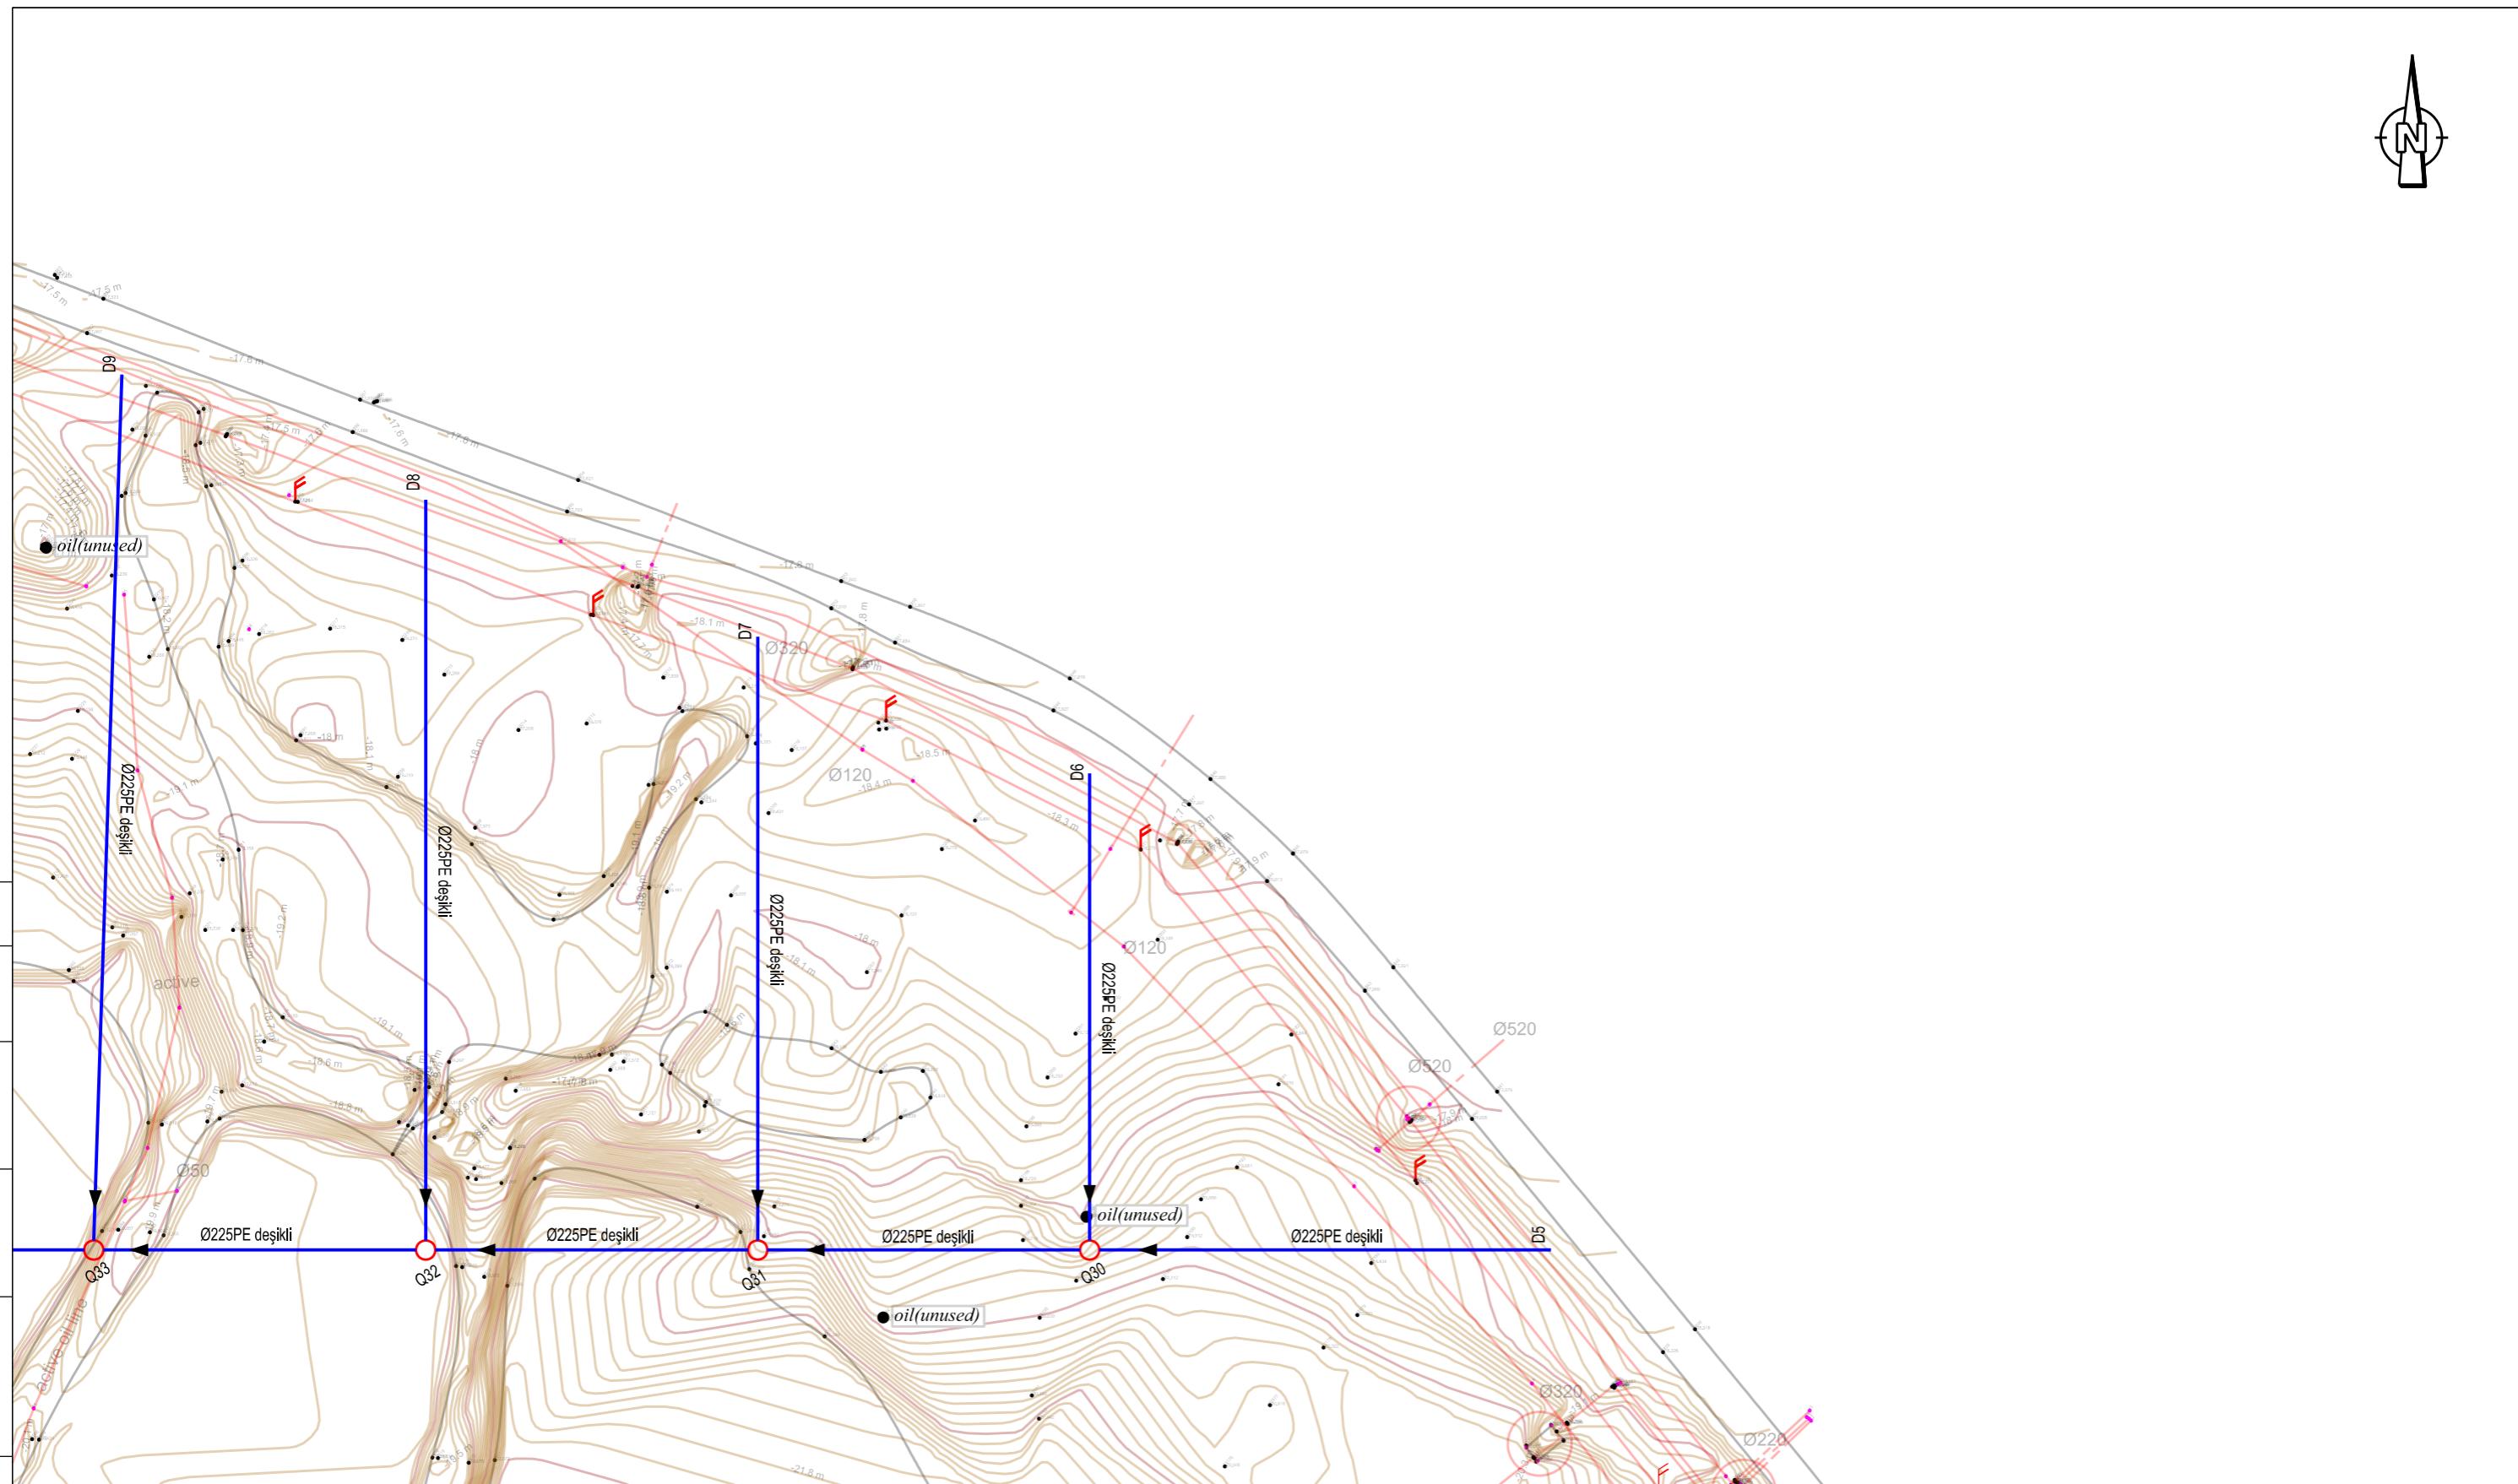

Cizgilərin birləşmə sxemi

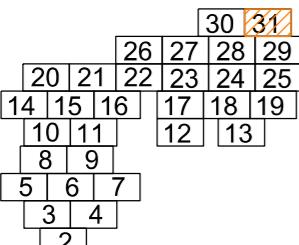

Şərti işarələr

Ø225 HDF

Ø315 HDF

Baxış quyu

2021/AT-04-DS-9.2.1

Suraxanı rayonunun inzibati ərazisində Zığ gölünün ətrafında yerləşən ərazilərdə yeni yaşlılıqların salınması və damcılı suvarma sisteminin qurulması

S/s	Materialın adı və texniki xarakteristikası	İstinad edilən sənədin adı	Ölçü vahidi	Miqdarı	Vahidin kütləsi, kq	Cəminin kütləsi, kq	Qeyd
1	Politelin boru Ø315	ГОСТ Р 52134-2003	m	1283.00			
2	Politelin boru Ø315 deşikli	ГОСТ Р 52134-2003	m	478.00			
3	Politelin boru Ø225	ГОСТ Р 52134-2003	m	522.00			
4	Politelin boru Ø225 deşikli	ГОСТ Р 52134-2003	m	23379.00			
5	Baxış quyuları	-	ədəd	192			Əlavə olaraq DK məlumatları verilecek

Razlaşdırılmışdı	Vəzifə	Soyad	İmza	Tarix

							2021/AT-04-DS-9.2.1-S
							Suraxanı rayonunun inzibati ərazisində Zığ gölünün ətrafında yerləşən ərazilərdə yeni yaşlılıqların salınması və damcılı suvarma sisteminin qurulması
Dəyiş.	Dəy.s	Vərəq	Sən.Nö	İmza	Tarix		
LBM	T.Ağayev						
İşlədi	N.Məmmədov						
Yoxladı	A. Aliyev						
Normanəz .	Y. Sitnikova						

Drenaj sistemi	mərhələ	vərəq	vərəqlər
	İL	1	1
Avadanlığın material və məmulatların spesifikasiyası	EIB	HYDROTRANS ENGINEERING	