

# Azərbaycan Respublikası



**“Hydrotrans Engineering Mühəndislik Mərkəzi” MMC**

**Lənkəran rayonu, Siyavar kənd ərazisində tikiləcək  
“Qamışlı” MMC-yə məxsus Nohur balıq yetişdirmə təsərrüfatı**

**Albom 1. Balıq yetişdirmə yerləri**

**İŞÇİ CİZGİLƏR**

**BAKİ 2022**

**Lənkəran rayonu, Siyavar kənd ərazisində tikiləcək  
“Qamışlı” MMC-yə məxsus Nohur balıq yetişdirmə təsərrüfatı**

**Albom 1. Balıq yetişdirmə yerləri**

**iŞÇİ CİZGİLƏR**

**Direktor:** Əliyev N.

**LBM:** Aliyev A.

## Cizgiların cədvəli

Nº	ADI	QEYDLƏR
1	İşçi çizgilərin siyahısı	
2	Sahə planı	
3	Yerləşmə görünüşü	
4	Ofis binasının planı	
5	Ofisin ikinci mərtəbəsinin planı	
6	Köməkçi binanın planı	
7	Ön fasad	
8	Arxa fasad	
9	Yan fasad - 1	
10	Yan fasad - 2	
11	En kəsik	

		Razlaşdırılmışdır		
INVENTAR №	MZA VƏ TARİX	İNV.Nº ƏVƏZİNƏ	Vəzifə	Soyad
				İmza
				Tarix

Lənkəran rayonu, Siyavar kənd ərazisində tikiləcək "Qamışlı" MMC-yə məxsus Nohur balıq yetişdirmə təsərrüfatı

Meydançanın kunc nöqtələri

- A. X=314896.4552; Y=4278389.2143
- B. X=314993.0978; Y=4278389.2143
- C. X=314993.0978; Y=4278186.7501
- D. X=314896.4552; Y=4278186.7501

Eksplikasiya

- 1. Ofis binası
- 2. Köməkçi bina
- 3. Su anbarı
- 4. Nasos stansiyası
- 5. Suqəbuledici qurğu

Şərti işaretlər


— Su xətti



Qeyd:  
1. Bütün koordinatlar WGS84 UTM 39 sistemində verilmişdir.  
2. Ayrılaçlı torpaq sahəsi 1.957 ha-dır.  
(96.7x202.4)


Dəyiş.	Dəy.s.	Vərəq	Sən.№	İmza	Tarix	Balıq yetişdirmə yerləri	mərhələ	vərəq	vərəqlər
LBM	A. Aliyev						B. L.	2	
İşlədi	N. Məmmədov								
Yoxladı	T. İsmayılov					Sahə planı	EIB	HYDROTRANS ENGINEERING	ENGİNEERING CENTER FOR DESIGN OF WATER AND TRANSPORT INFRASTRUCTURE SU NAQİYYƏT İNFRASTRÜKTURLARIN LİSEKLƏNDİRİLMƏSI İŞLƏR MƏRKƏZİ
Normanəz.	Y. Sitnikova								

INVENTAR №	IMZA VƏ TARİX	INV.NƏ İVƏZİNƏ

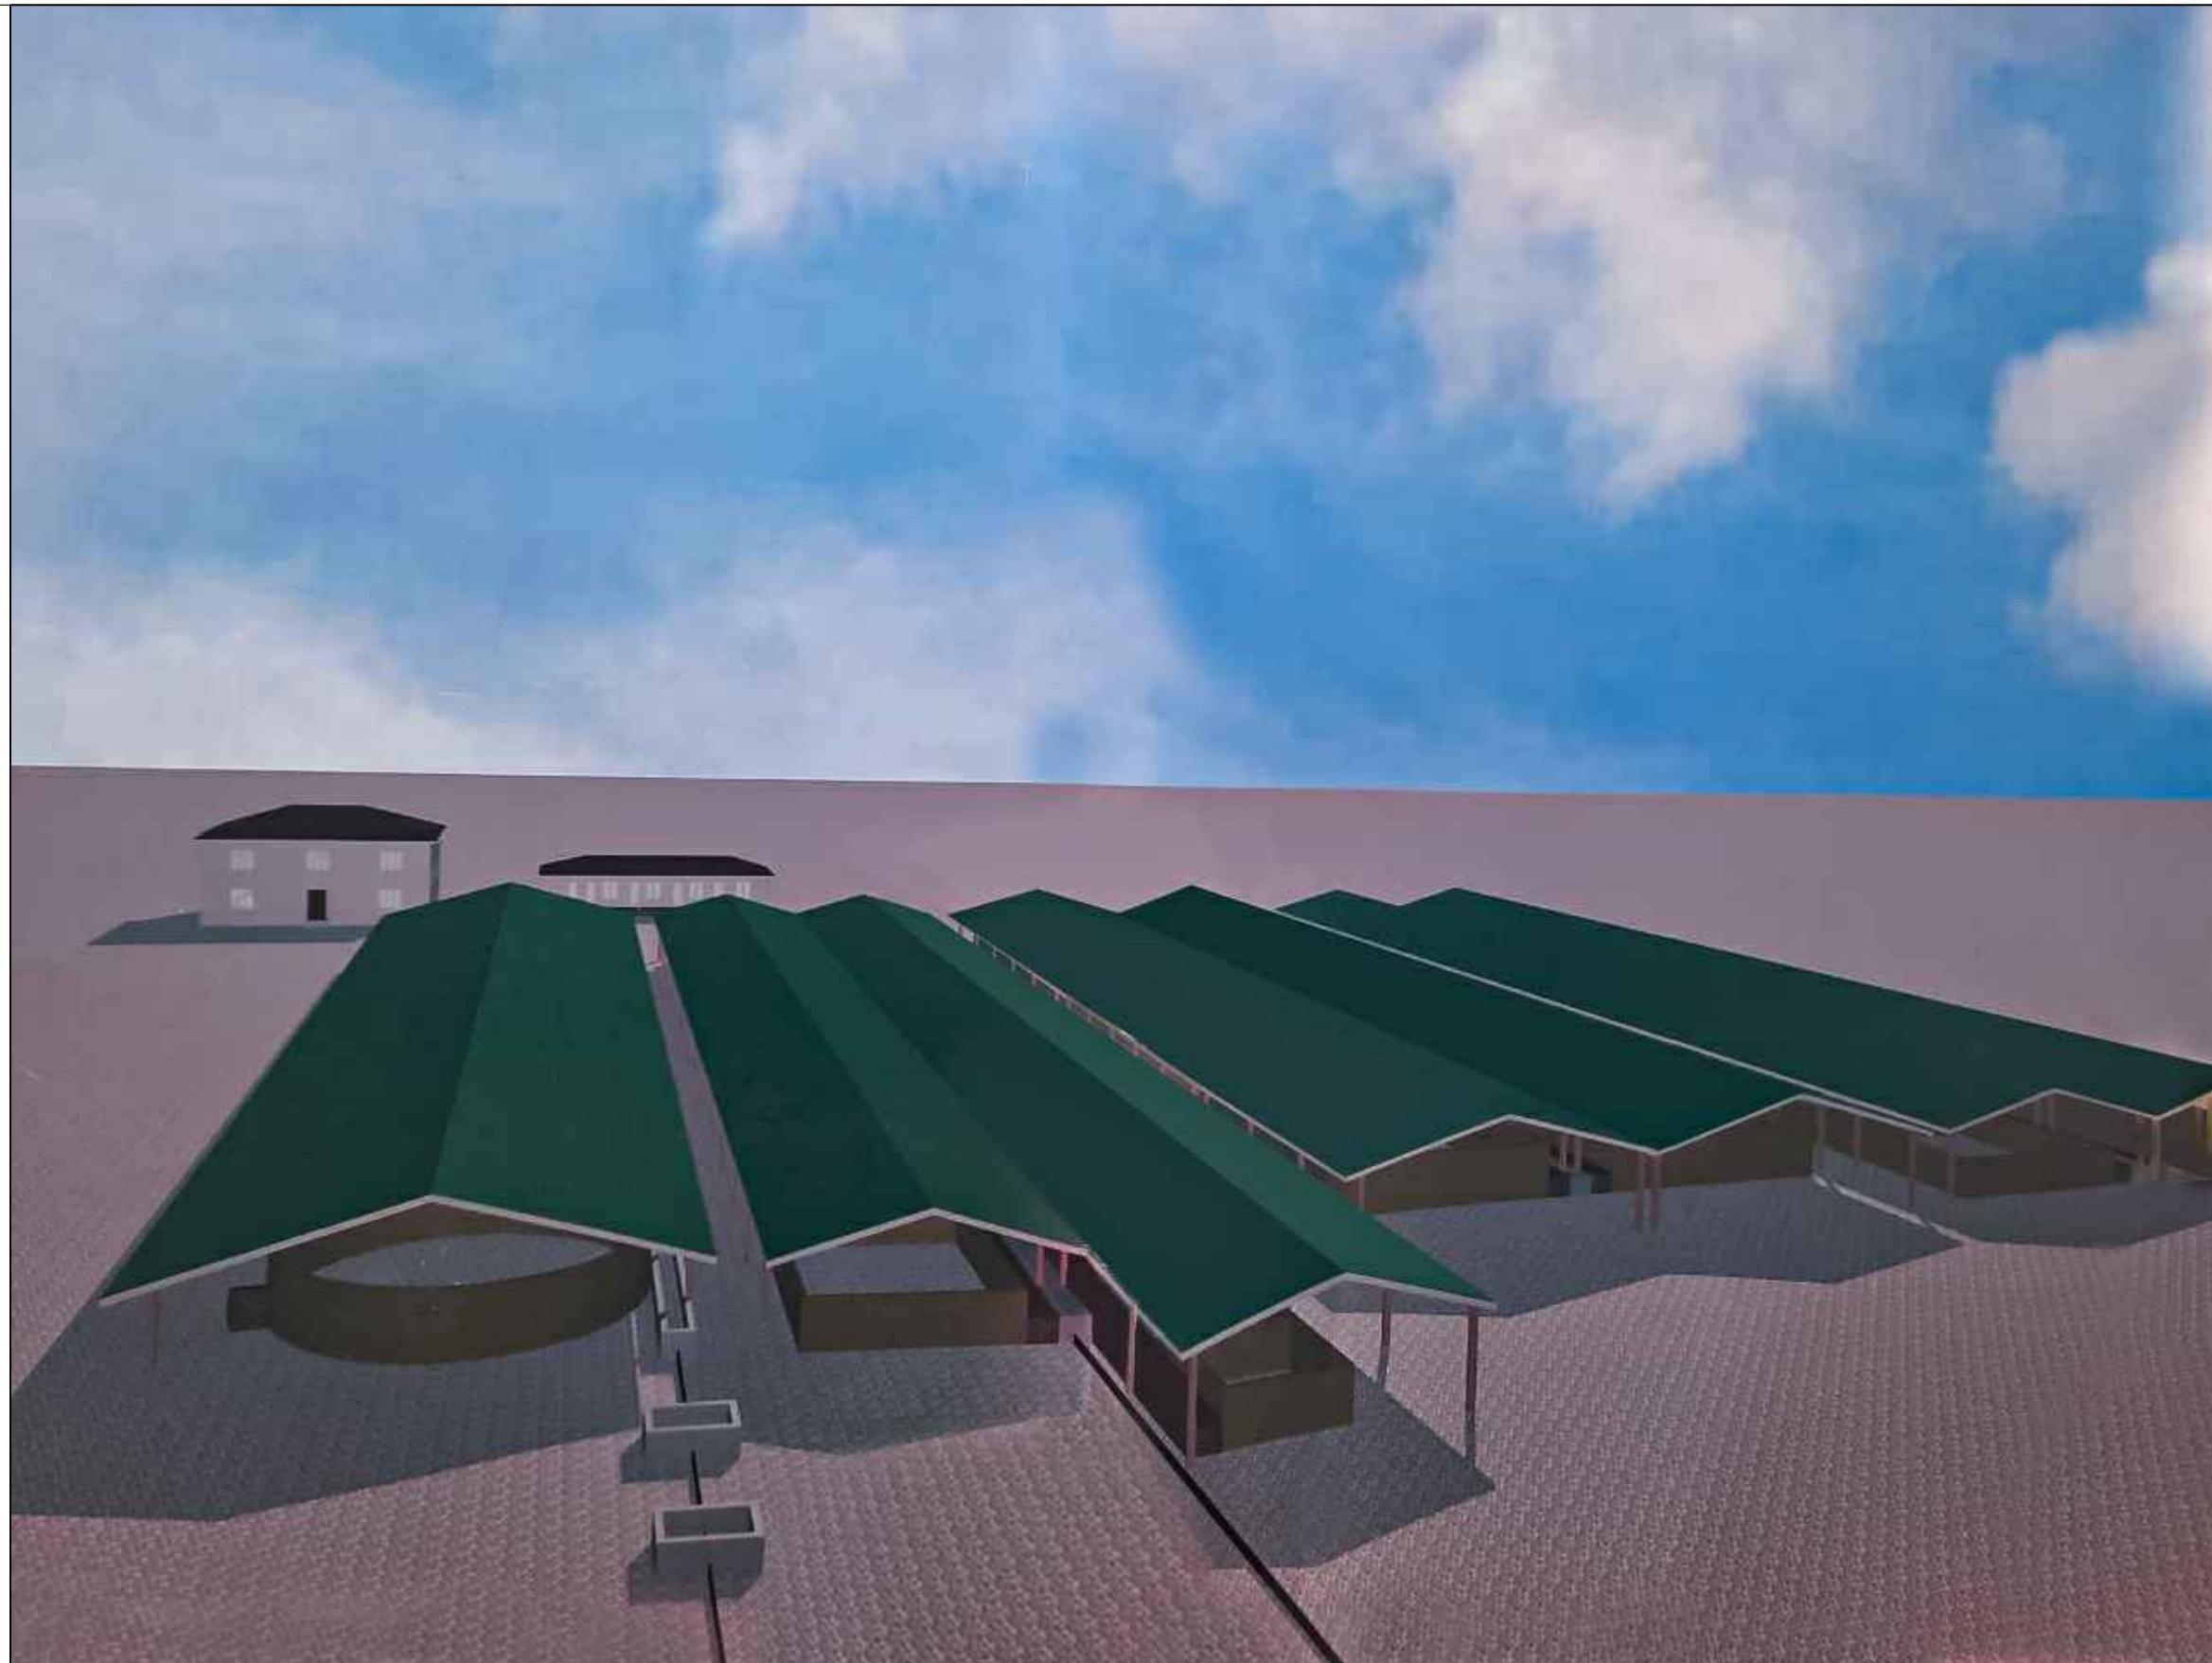

Razlaşdırılmışdır				
Vəzifə	Soyad	İmza	Tarix	

Dəyiş	Dəy.say.	Vərəq	Sən.Nö	İmza	Tarix	Lənkəran rayonu, Siyavar kənd ərazisində tikiləcək "Qamışlı" MMC-yə məxsus Nohur balıq yetişdirmə təsərrüfatı	Mərhələ	Vərəq	Vərəqlər
						Balıq yetişdirmə yerləri	I.L	3	
LBM	A. Aliyev								
İşlədi	N. Məmmədov								
Yoxladı	T. İsmayılov								
Normanəz.	Y. Sitnikova								
						Yerləşmə görünüşü		HYDROTRANS ENGINEERING	

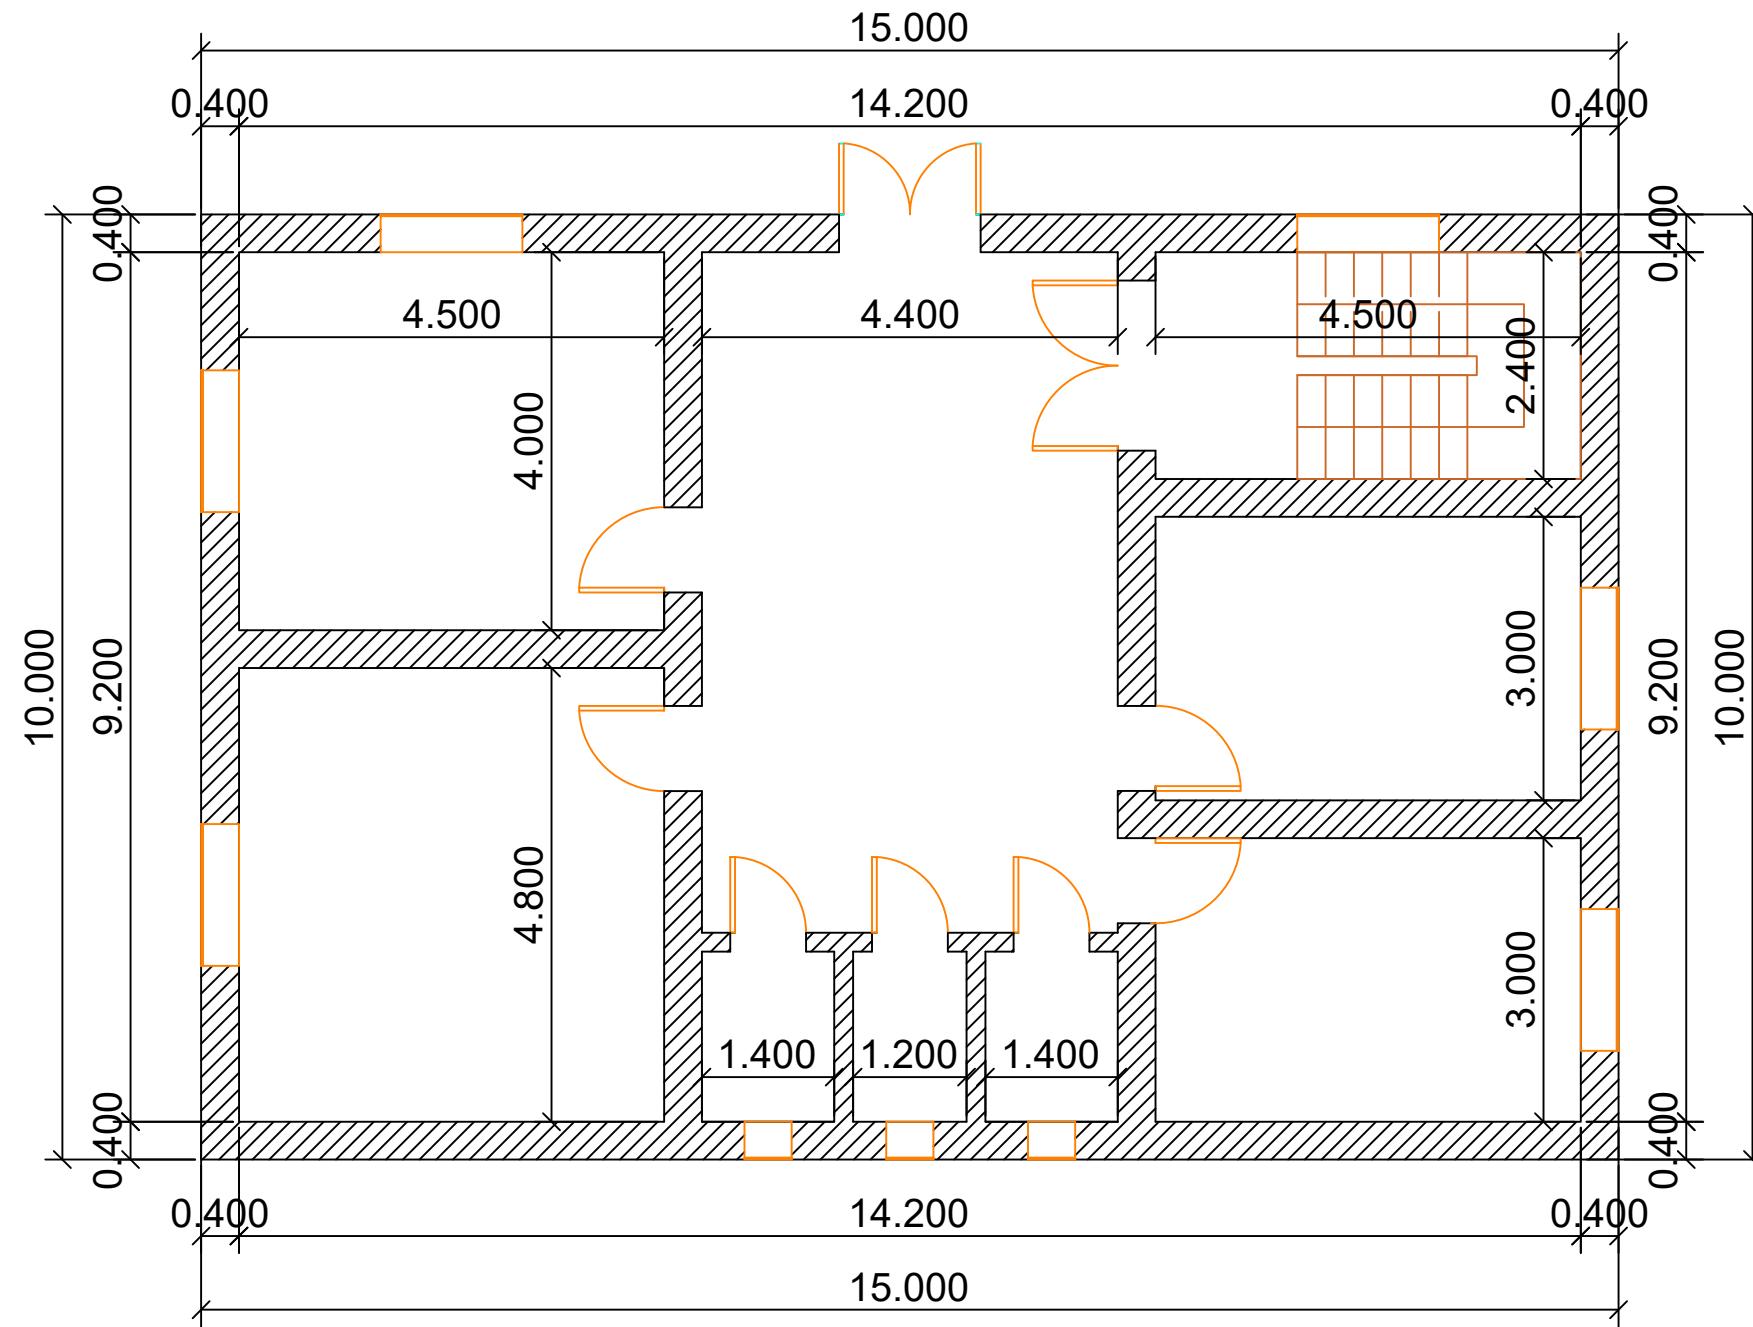


Dəyiş	Dey.say.	Vərəq	Sən.No	İmza	Tarix	Lənkəran rayonu, Siyavar kənd ərazisində tikiləcək "Qamışlı" MMC-yə məxsus Nohur balıq yetişdirmə təsərrüfatı		
LBM	A. Aliyev				Balıq yetişdirmə yerləri	Mərhələ	Vərəq	Vərəqlər
İşlədi	N. Məmmədov					i.L	4	
Yoxladı	T. İsmayılov				Ofis binasının planı			
Normanəz.	Y. Sitnikova				Miqyas 1:80			

## Lənkəran rayonu, Siyavar kənd ərazisində tikiləcək "Qamışlı" MMC-yə məxsus Nohur balıq yetişdirmə təsərrüfatı

Başarı yetişdirmə verləri


Ofis binasının planı  
Miqyas 1:80

INVENTAR №		IMZA VƏ TARİX	INV.NƏ İVƏZİNƏ
Vəzifə	Soyad	İmza	Tarix

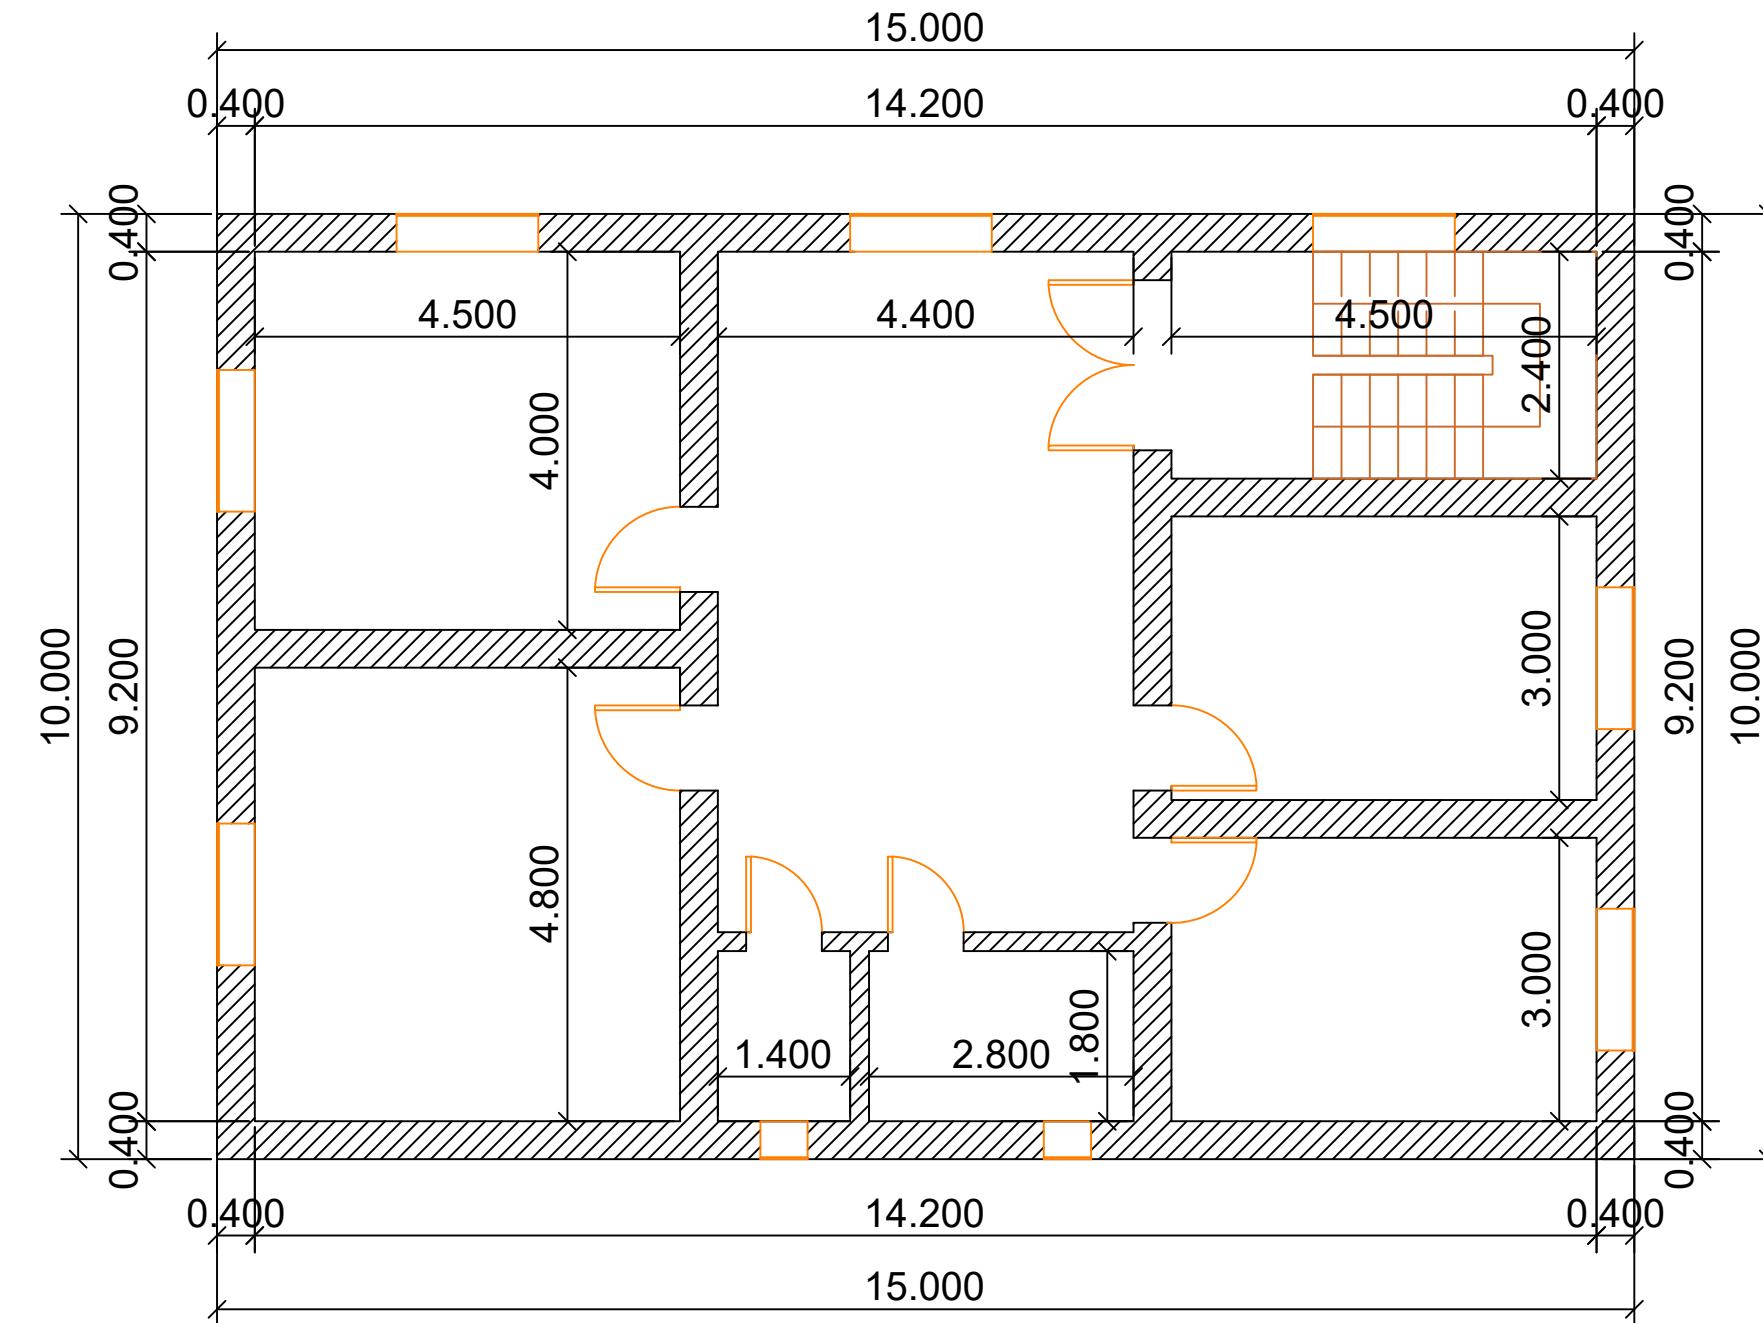


Dəyiş	Dəy.say.	Vərəq	Sən.Nö	İmza	Tarix	Lənkəran rayonu, Siyavar kənd ərazisində tikiləcək "Qamışlı" MMC-yə məxsus Nohur balıq yetişdirmə təsərrüfatı	Mərhələ	Vərəq	Vərəqlər
LBM	A. Aliyev					Balıq yetişdirmə yerləri	İ.L	5	
İşlədi	N. Məmmədov								
Yoxladı	T. İsmayılov					Ofisin ikinci mərtəbəsinin planı Miqyas 1:80			
Normanəz.	Y. Sitnikova								

INVENTAR №		IMZA VƏ TARİX	INV.NƏ İVƏZİNƏ
Vəzifə	Soyad	İmza	Tarix

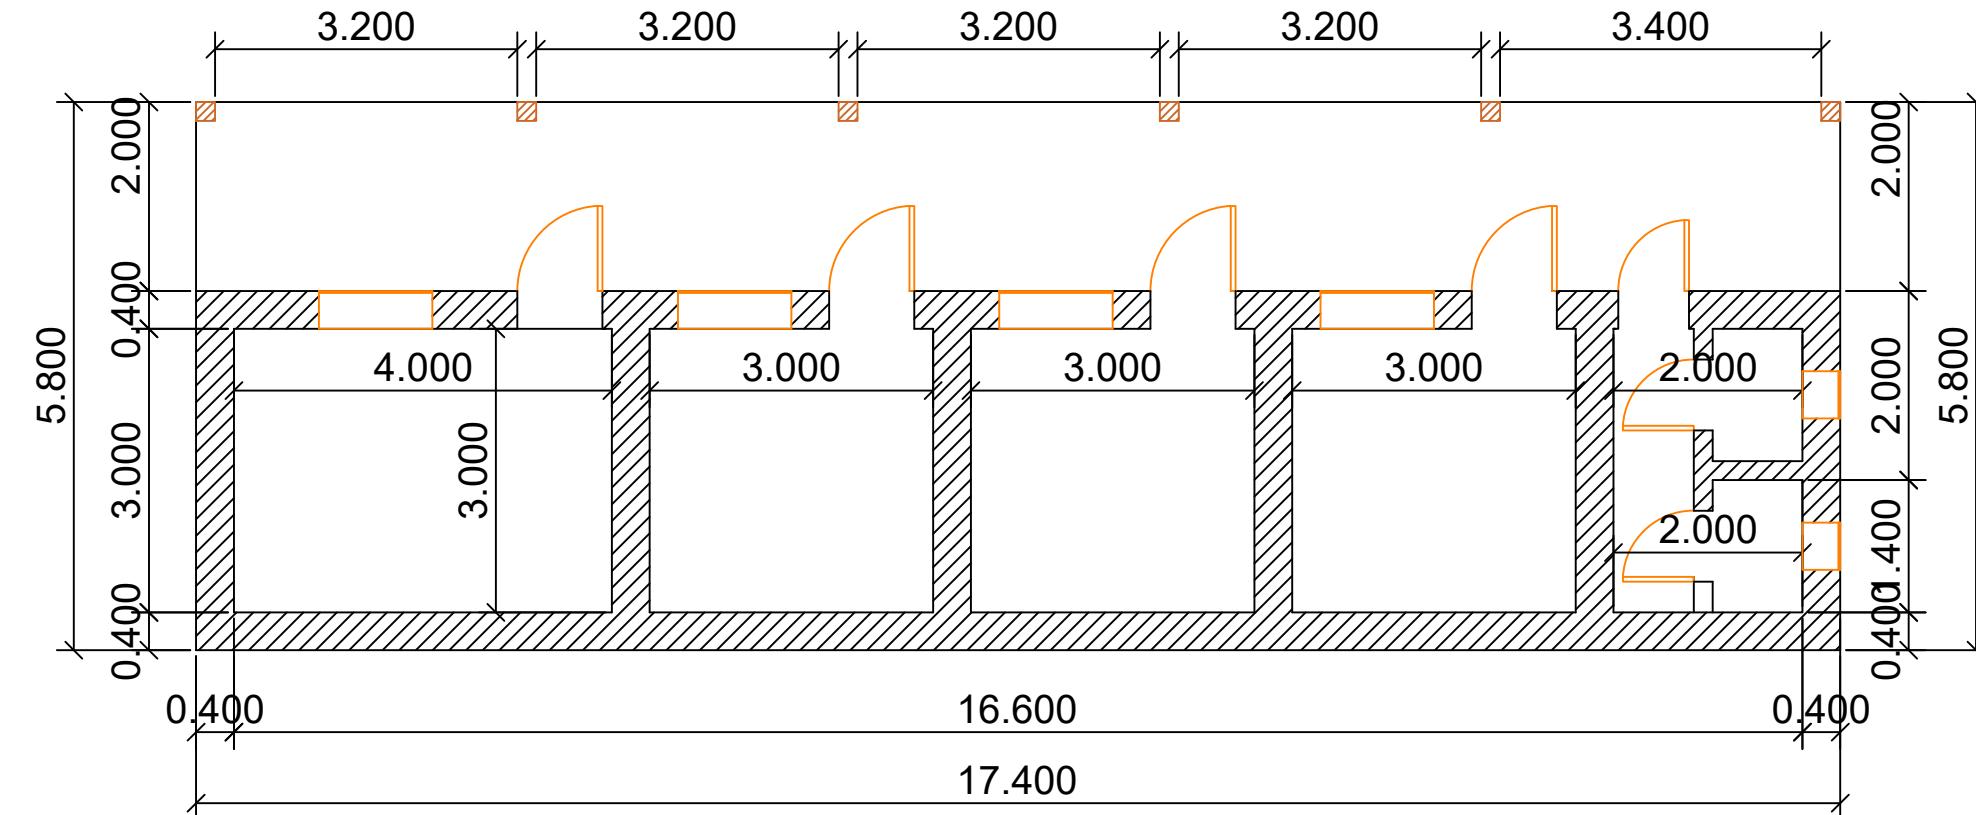

Dəyiş	Dəy.say	Vərəq	Sən.Nö	İmza	Tarix	Lənkəran rayonu, Siyavar kənd ərazisində tikilecək "Qamışlı" MMC-yə məxsus Nohur balıq yetişdirmə təsərrüfatı	Mərhələ	Vərəq	Vərəqlər
LBM	A. Aliyev					Balıq yetişdirmə yerləri	Köməkçi binanın planı Miqyas 1:80	İ.L	6
İşlədi	N. Məmmədov								
Yoxladı	T. İsmayılov								
Normanəz.	Y. Sitnikova								

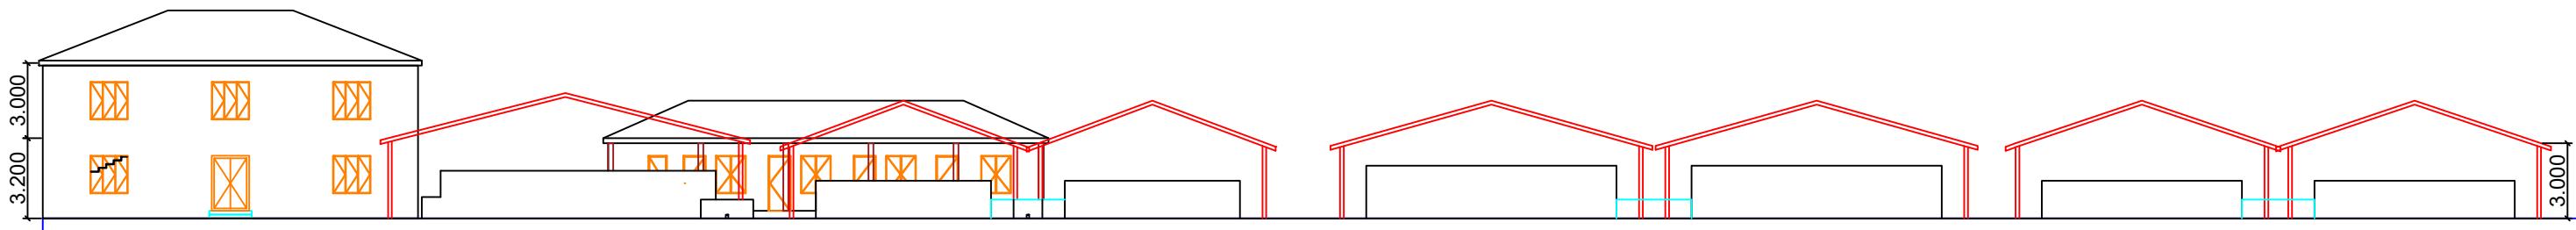


Razlaşdırılmışdır					
Vəzifə	Soyad	İmza	Tarix		

INVENTAR №	IMZA VƏ TARİX	INV.№ ƏVƏZİNƏ

Dəyiş	Dəy.say.	Vərəq	Sən.Nº	İmza	Tarix			
LBM	A. Aliyev					Balıq yetişdirmə yerləri		
İşlədi	N.Məmmədov							
Yoxladı	T. İsmayılov							
Normanəz.	Y. Sitnikova							
						Ön fasad Miqyas 1:265		

Lənkəran rayonu, Siyavar kənd ərazisində tikiləcək "Qamışlı"  
MMC-yə məxsus Nohur balıq yetişdirmə təsərrüfatı

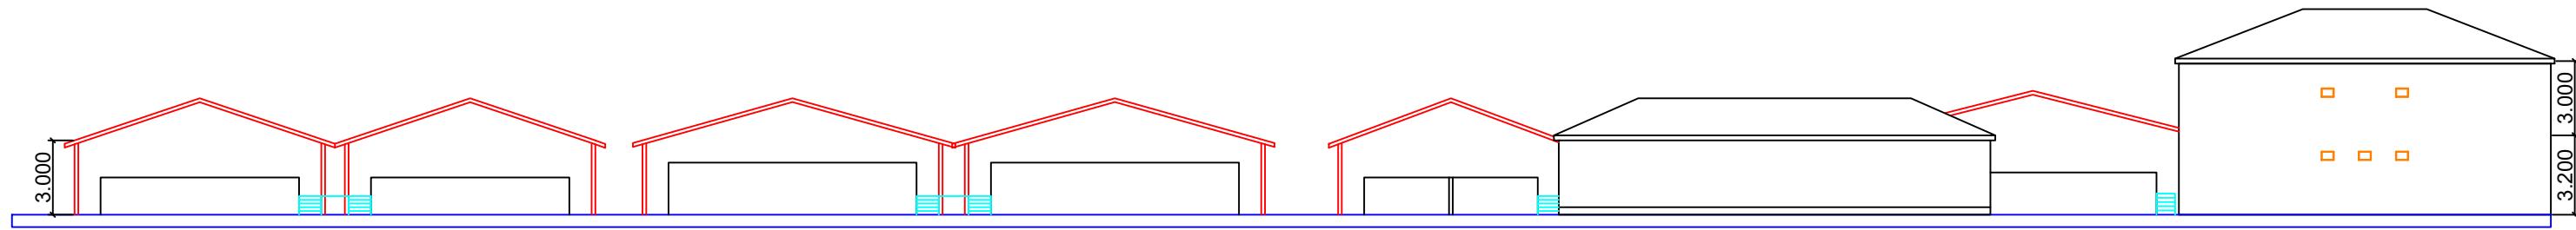


Razlaşdırılmışdır					
Vəzifə	Soyad	İmza	Tarix		

INVENTAR №	IMZA VƏ TARIX	INV.NƏ İVƏZİNƏ

Dəyiş	Dəy.say.	Vərəq	Sən.Nö	İmza	Tarix			
LBM	A. Aliyev					Balıq yetişdirmə yerləri		
İşlədi	N.Məmmədov							
Yoxladı	T. İsmayılov							
Normanəz.	Y. Sitnikova							
						Arxa fasad Miqyas 1:265		

Lənkəran rayonu, Siyavar kənd ərazisində tikiləcək "Qamışlı"  
MMC-yə məxsus Nohur balıq yetişdirmə təsərrüfatı

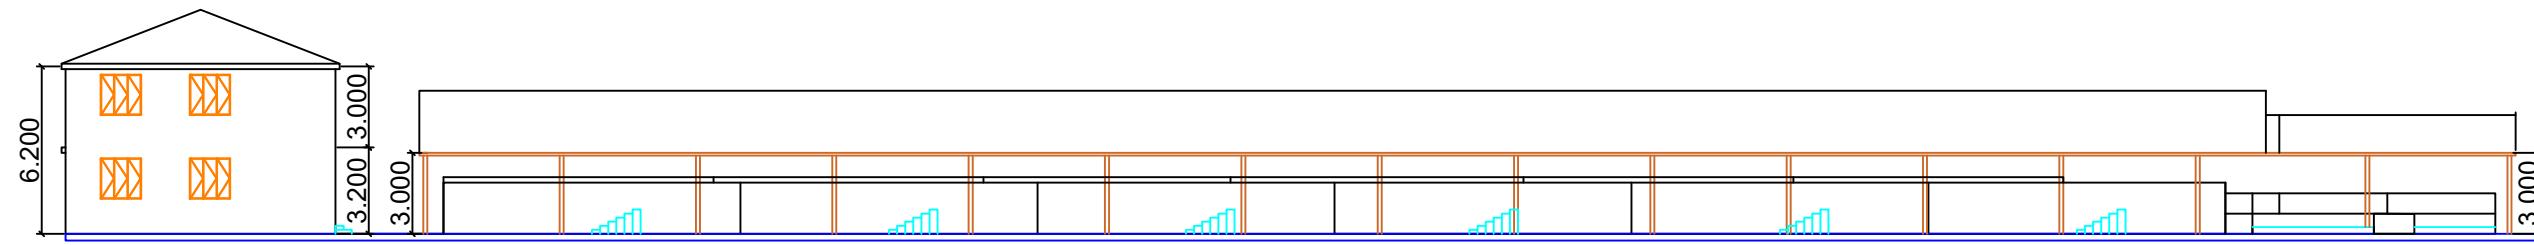


Razlaşdırılmışdır					
Vəzifə	Soyad	İmza	Tarix		

INVENTAR №	IMZA VƏ TARIX	INV.NƏ İVƏZİNƏ

Dəyiş	Dəy.say.	Vərəq	Sən.Nö	İmza	Tarix			
LBM	A. Aliyev					Balıq yetişdirmə yerləri		
İşlədi	N.Məmmədov							
Yoxladı	T. İsmayılov							
Normanəz.	Y. Sitnikova							
						Yan fasad - 1 Miqyas 1:280		

Lənkəran rayonu, Siyavar kənd ərazisində tikiləcək "Qamışlı"  
MMC-yə məxsus Nohur balıq yetişdirmə təsərrüfatı

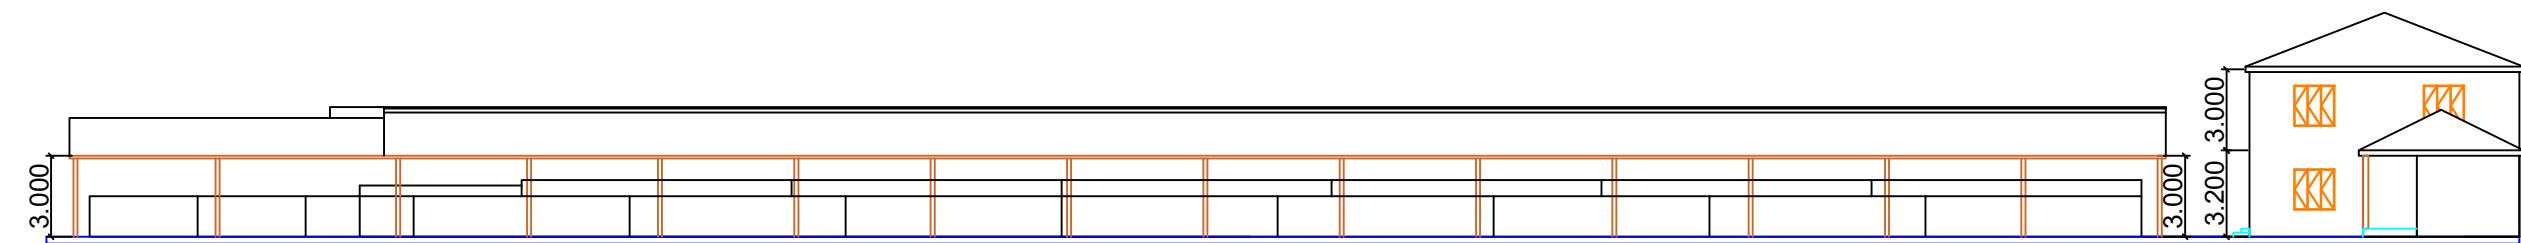


Razlaşdırılmışdır					
Vəzifə	Soyad	İmza	Tarix		

INVENTAR №	İMZA VƏ TARİX	INV.№ ƏVƏZİNƏ

Dəyiş	Dəy.say.	Vərəq	Sən.Nö	İmza	Tarix			
LBM	A. Aliyev					Balıq yetişdirmə yerləri		
İşlədi	N.Məmmədov							
Yoxladı	T. İsmayılov							
Normanəz.	Y. Sitnikova							
						Yan fasad - 2 Miqyas 1:280		

Lənkəran rayonu, Siyavar kənd ərazisində tikiləcək "Qamışlı"  
MMC-yə məxsus Nohur balıq yetişdirmə təsərrüfatı

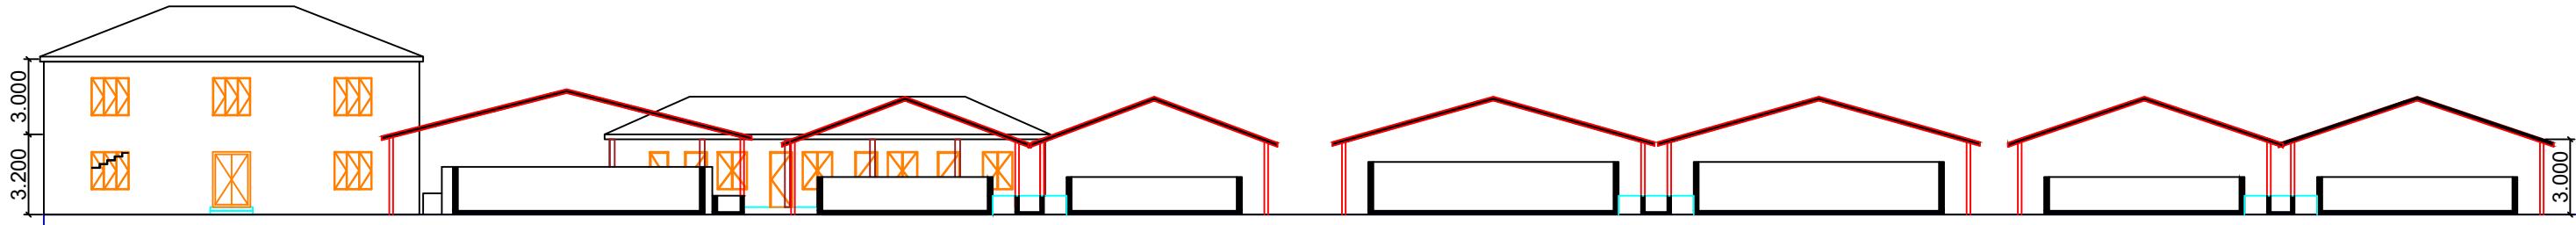

Dəyiş	Dəy.say.	Vərəq	Sən.No	İmza	Tarix	Lənkəran rayonu, Siyavar kənd ərazisində tikilecək "Qamışlı" MMC-yə məxsus Nohur balıq yetişdirmə təsərrüfatı
LBM	A. Aliyev	Balıq yetişdirmə yerləri				Mərhələ
İşlədi	N.Məmmədov					i.L
Yoxladı	T. İsmayılov	En kəsik Miqyas 1:265				11
Normanəz.	Y. Sitnikova					

Lənkəran rayonu, Siyavar kənd ərazisində tikiłcək "Qamışlı" MMC-yə məxsus Nohur balıq yetişdirmə təsərrüfatı

Balıq yetişdirmə yerləri

En kësik  
Miqyas 1:265

